

REPUBLIKA E KOSOVËS / REPUBLIC OF KOSOVO
Fondi i Kosovës për Eficiencë të Energjisë
Kosovo Energy Efficiency Fund

Angazhimi i Kompanive pâr kryerje të punëve ndërtimore pâr implementimin e masave të Eficiencës se Energjisë në ndërtesat shumë banesore sociale

Nr. Prokurimit : VET-FKEE2020-24-1699-5-1-C70

Kompania punekryese



ATC COM SHPK & DAJTING SHPK

nnpattcom@gmail.com

Emri i ndërtuesës:

**Ndertesa shume banesor Social I,
Klinë**

Faza e projektit:

Arkitektura

Emri i vizatimit:

Lokacioni i ndërtesës

Punuar nga:

BSc Liridon Sejdiu

Kontrolluar nga:

IDA. Njomza Hoti

Datë:

10/2023


Rishikim:

Shkalla e zvogëlimit:

P=1:100

Nr. i fases:


01

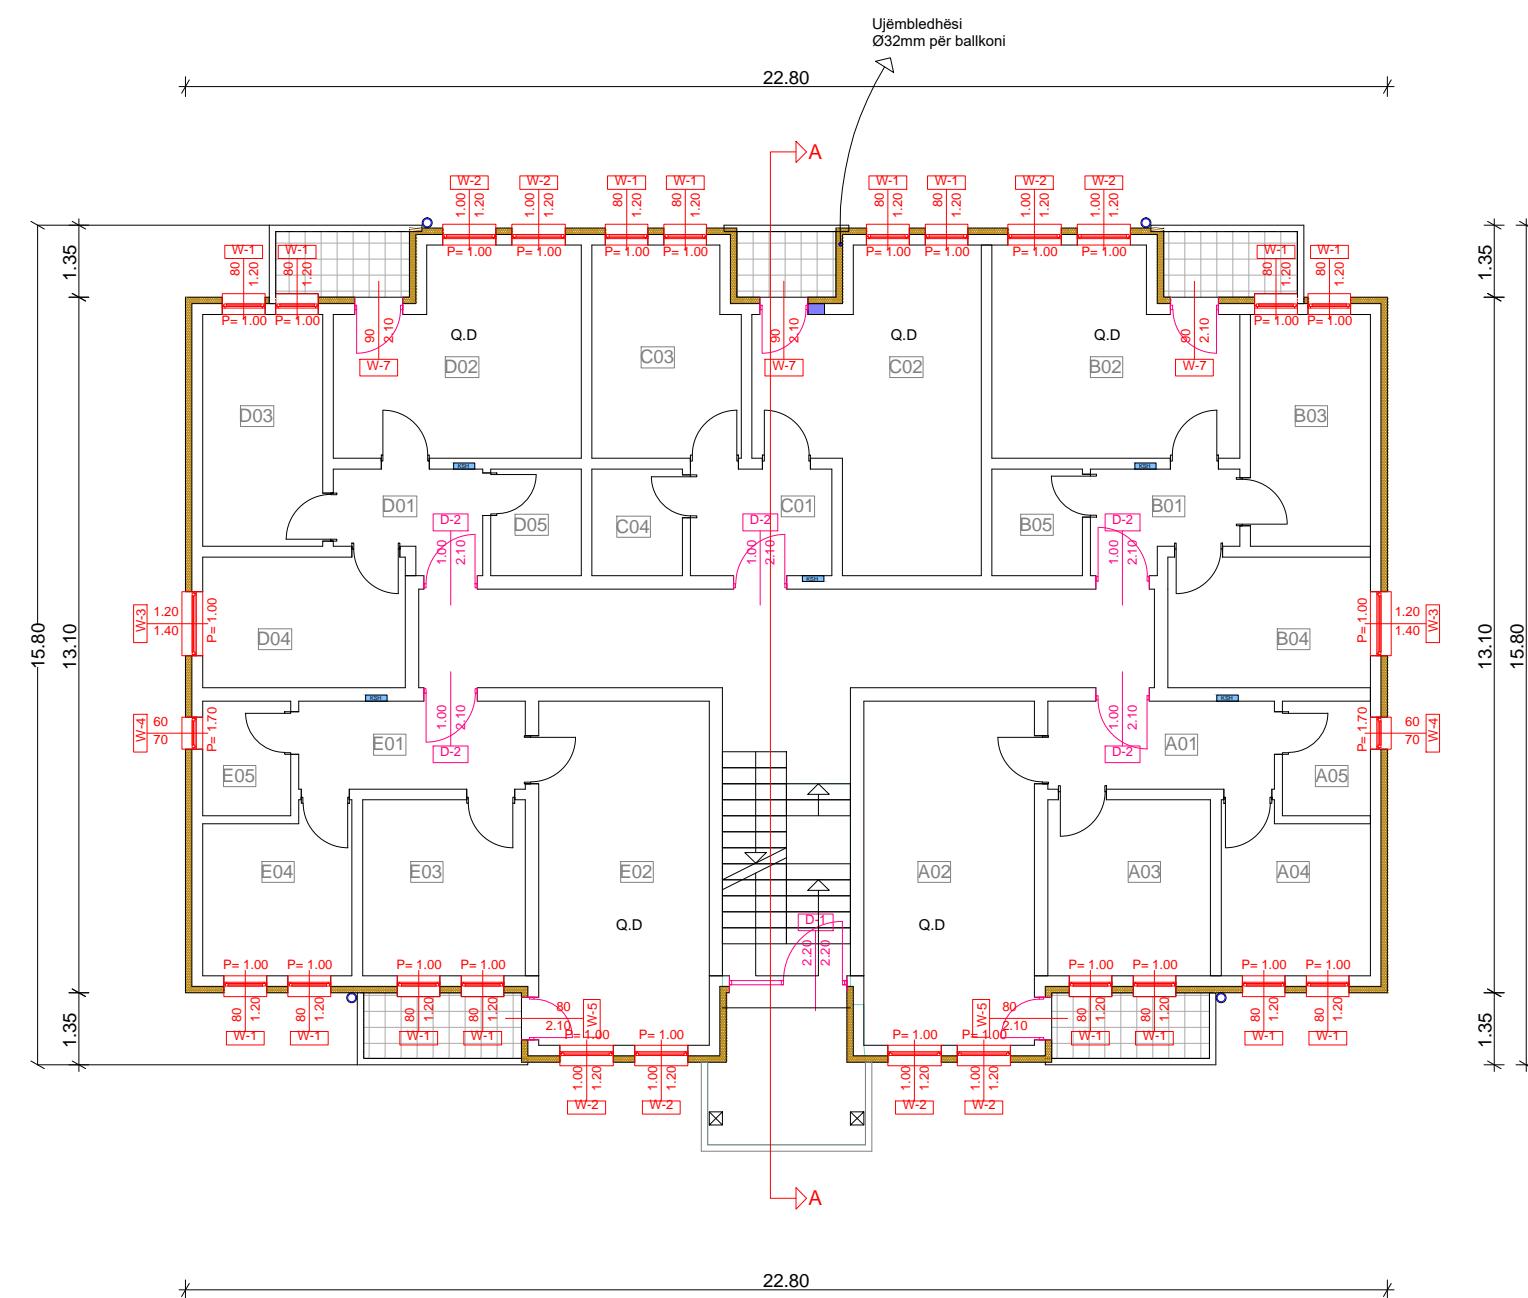

Përshkrimi renovimit

-  Termoizolimi i mureve me EPS t=12cm
 -  Ndërrimi i dritareve
 -  Ndërrimi i dyerave
 -  Muratim

 <p>FKEE FONDI I KOSOVËS PËR EFICIËNCË TË ENERGIJISË FONDI I KOSOVËS PËR EFICIËNCË TË ENERGIJISË Kosovo Energy Efficiency Fund</p>
<p>REPUBLIKA E KOSOVËS / REPUBLIC OF KOSOVO</p> <p>Fondi i Kosovës për Eficiencë të Energijsë Kosovo Energy Efficiency Fund</p>
<p>Projekti:</p> <p>Angazhimi i Kompanive pâr kryerje të punëve ndërtimore pér implementimin e masave të Eficiencës së Energjisë në ndërtesat shumë banesore sociale</p>
<p>Nr. Prokurimit : VET-FKEE2020-24-1699-5-1-1/C70 LOT 5</p> <p>Kompania punekryuese</p> <div style="display: flex; align-items: center;">  <div style="margin-left: 20px;"> ATC <small>ALL TYPES OF CONSTRUCTION</small> </div> <div style="margin-left: 20px;"> ATC COM SHPK & DAITING SHPK npnattcom@gmail.com </div> </div> <p>Emri i ndërtesës:</p> <p style="text-align: center;">Ndertesa shume banesor Social I, Klinë</p> <p>Faza e projektimit:</p> <p style="text-align: center;">Arkitektura</p> <p>Emri i vizatimit:</p> <p style="text-align: center;">Përdhesa</p> <p>Punuar nga: BSc Liridon Sejdiu</p> <p>Kontrolluar nga: IDA. Njomza Hoti</p> <p>Datë: 10/2023 Rishikim:</p> <p>Shkalla e zgjedhimit: P=1:100 Nr. i faqes: 02</p>

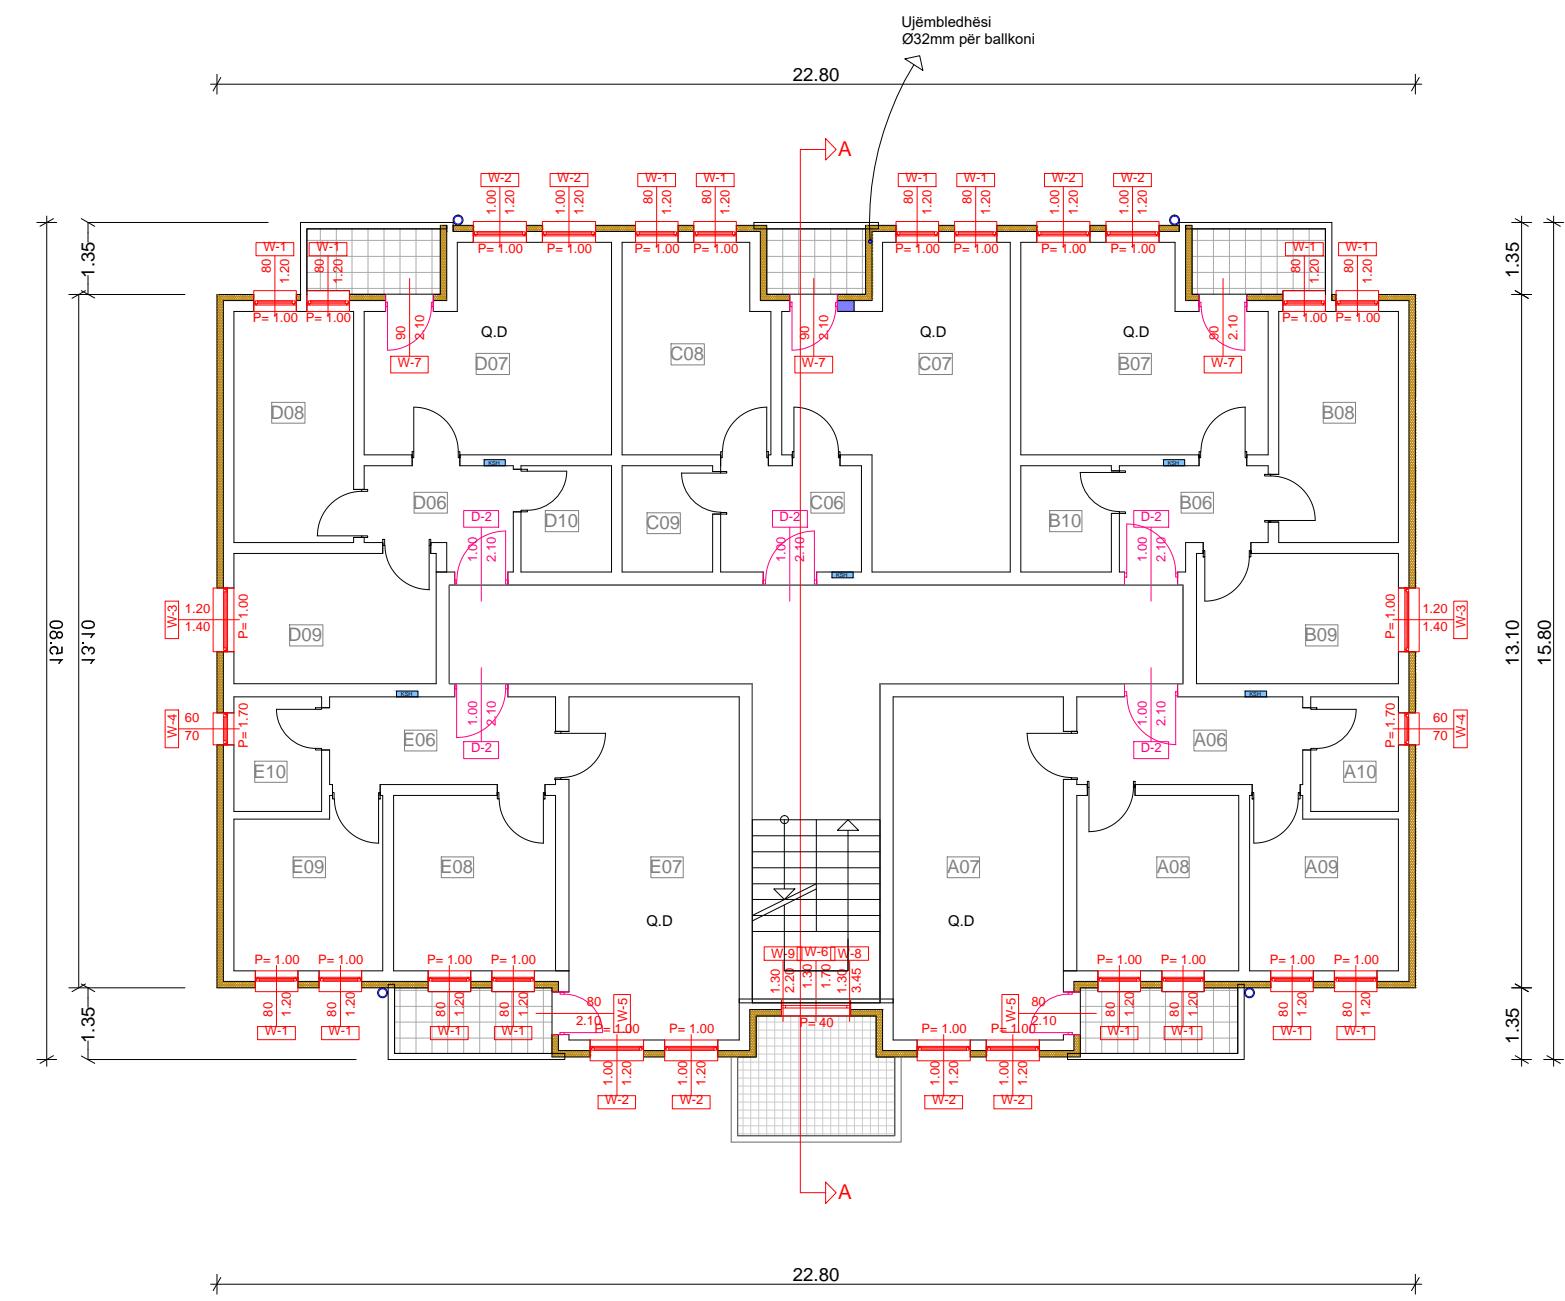

Përshkrimi renovimit

-  Termoizolimi i mureve me EPS t=12cm
 -  Ndërrimi i dritareve
 -  Ndërrimi i dyerve
 -  Renovimi i strehes te hryja
 -  Mur i ri



Projekti:
Angazhimi i Kompanive pâr kryerje të punëve ndërtimore pér implementimin e masave të Eficiencës së Energjisë në ndërtesat shumë banesore sociale

Nr. Prokurimit : VET-FKEE2020-24-1699-5-1-1/C70 LOT 5



ATC COM SHPK & DAJTING SHPK

Emri i ndertesës:
Ndertesa shume banesor Social I,

Faza e projektimit:

Emri i vizatimit:


Bryggar noga; Kontrollerar noga;

BSc Liridon Sejdiu	IDA. Njomza Ho
Datë:	10/2023

Shkalla e zvogëlimit: P=1:100	Nr. i faqes:
---	--------------

ANSWER



594x420mm

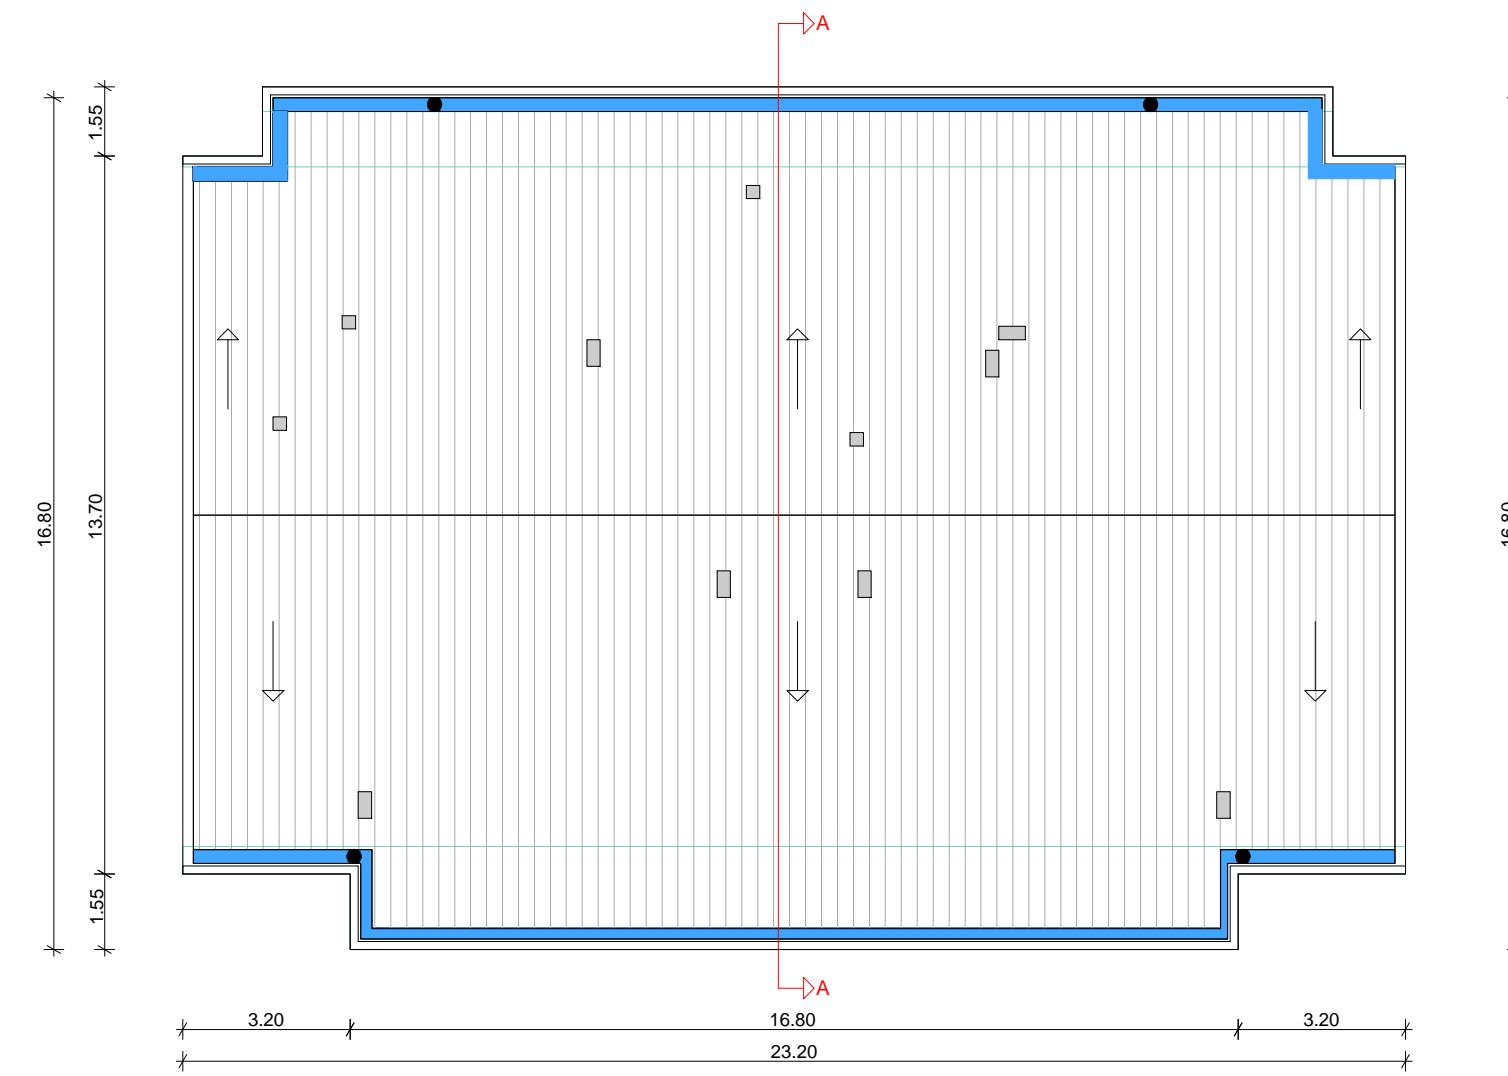

Përshtkimi renovimit

- Ndërrimi i mbulesës dhe termoizolimi i kulmit me EPS t=16cm
- Ndërrimi i ulluqeve horizontale
- Ndërrimi i ulluqeve vertikale

	FKEE FONDI KOSOVAR PER EFEKCIENË TË ENERGIJE [®] Fond i Kosovës per Eficiencë të Energjise Kosovo Energy Efficiency Fund
Projekti: Angazhimi i Kompanive për kryerje të punëve ndërtimore për implementimin e masave të Eficiencës se Energjisë ne ndertesat shumë banesore sociale	
Nr. Prokurimit : VET-FKEE2020-24-1699-5-1/C70 LOT 5 Kompania punëkryese ATC COM SHPK & DAJTING SHPK npatcom@gmail.com	
Emri i ndertesës: Ndertesa shume banesor Social I, Klinë	
Faza e projektit: Arkitektura	
Emri i vizatimit: Kulmi	
Punuar nga: BSc Liridon Sejdiu	Kontrolluar nga: IDA. Njomza Hoti
Dati: 10/2023	Rishikim:
Shkalla e zvogëlimit: P:1:100	Nr. i faqes: 04

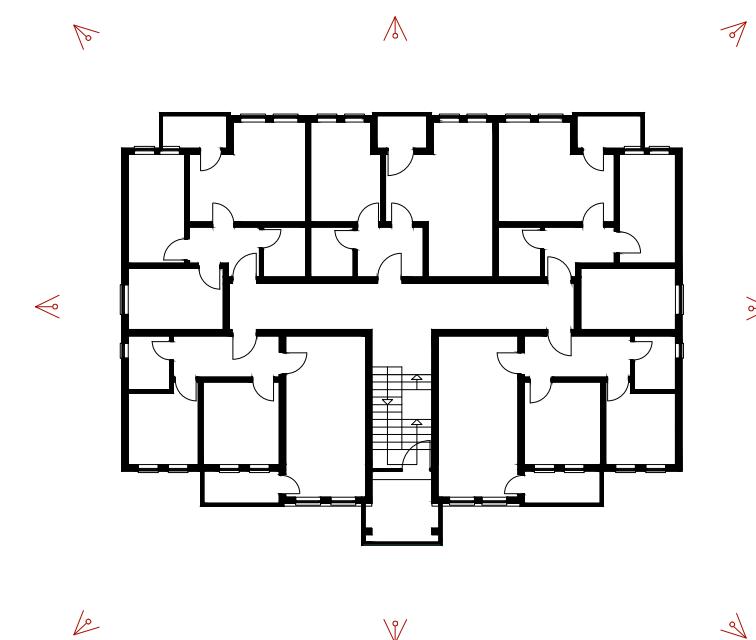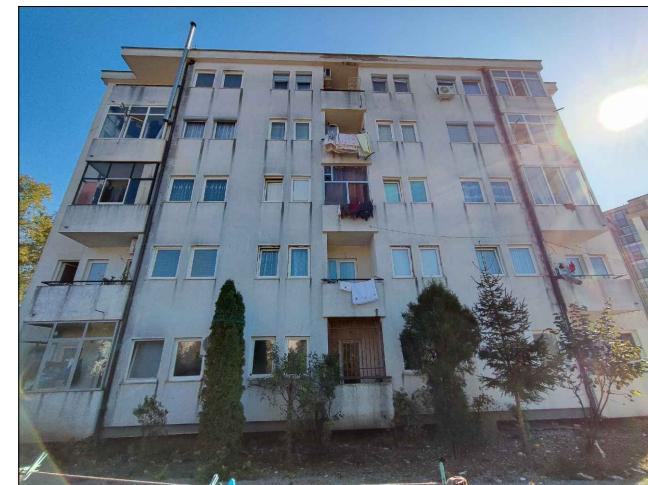

REPUBLIKA E KOSOVËS / REPUBLIC OF KOSOVO
Fondi i Kosovës për Eficiencë të Energjisë Kosovo Energy Efficiency Fund

Projekti:

Angazhimi i Kompanive për kryerje të punëve ndërtimore për implementimin e masave të Eficiencës se Energjisë në ndërtesat shumë banesore sociale

Nr. Prokurimit : VET-FKEE2020-24-1699-5-1-1/C70 LOT 5

Kompania punekryese



ATC COM SHPK & DAJTING SHPK

nnpatccom@gmail.com

Emri i ndërtesës:

**Ndertesa shume banesor Social I,
Klinë**

Faza e projektimit:

Arkitektura

Emri i vizitimit:

Fotot e ndërtesës

Punuar nga:

BSc Liridon Sejdiu

Kontrolluar nga:

IDA. Njomza Hoti

Datë:

10/2023


Rishikim:

Shkalla e zvogëlimit:

P=1:100

Nr. i fases:

05

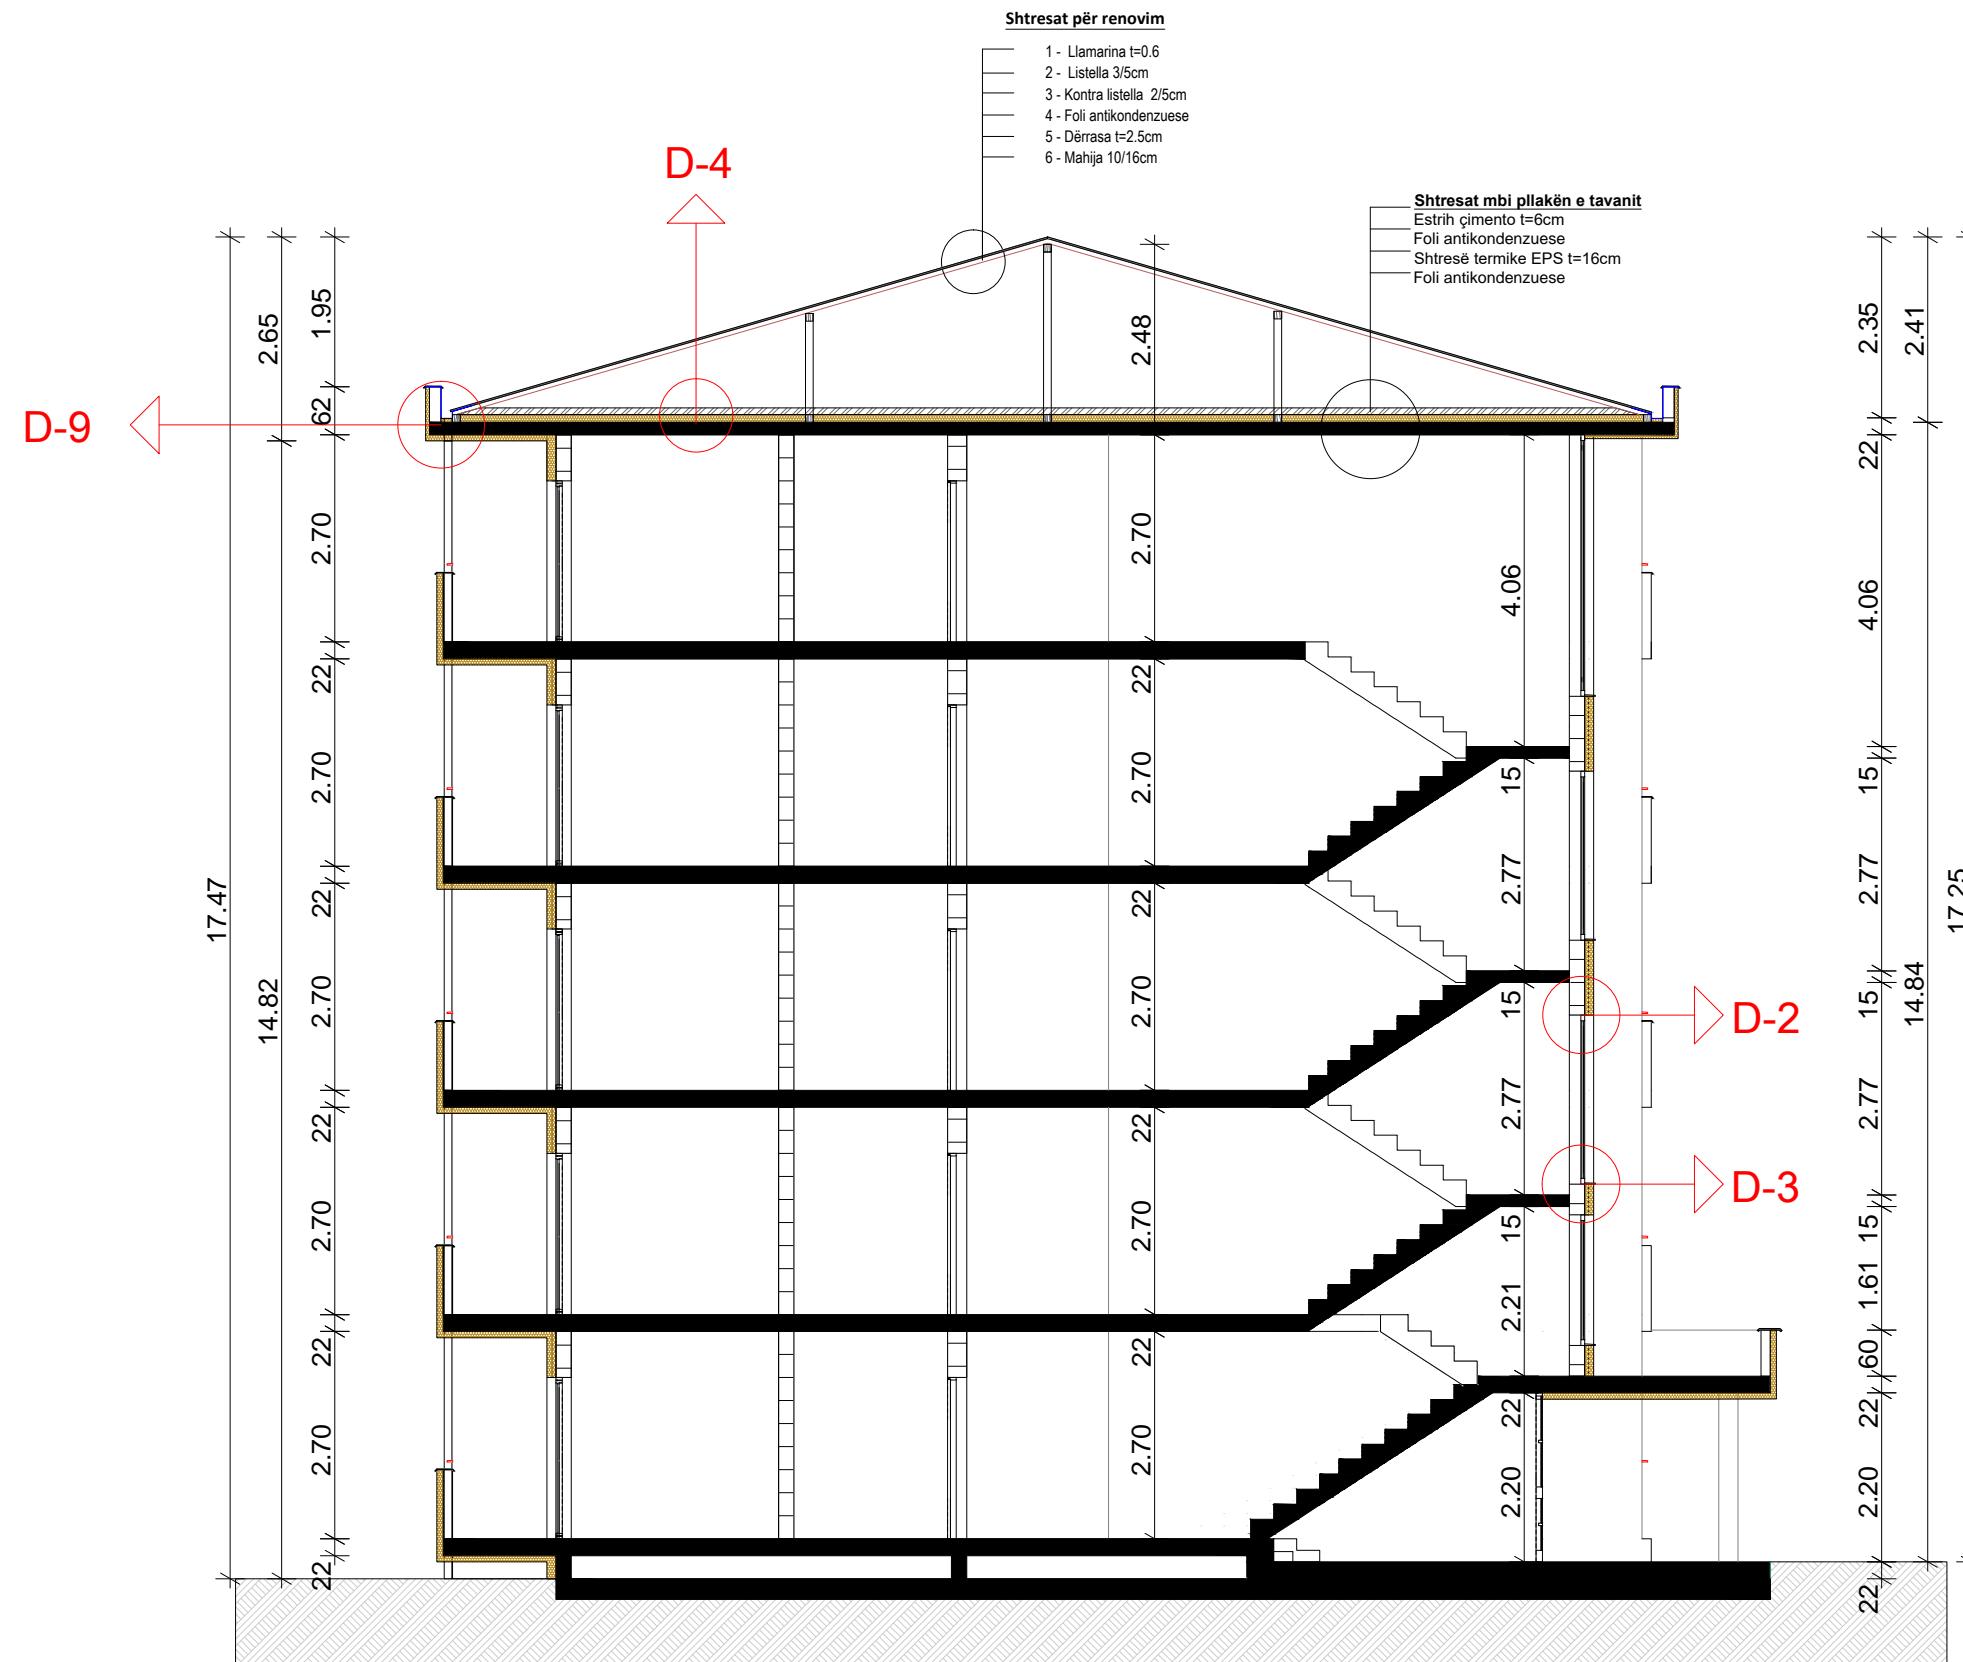

REPUBLIKA E KOSOVËS / REPUBLIC OF KOSOVO
Fondi i Kosovës për Eficiencë të Energjisë
Kosovo Energy Efficiency Fund

Projekti

Angazhimi i Kompanive păr kryerje të punëve ndërtimore pér implementimin e masave të Eficiencës se Enerqisë në ndërtesat shumë banesore sociale

Nr. Prokurimit : VET-FKEE2020-24-1699-5-1-1/C70 LOT 5

Kompania punekryse



TC.COM.SURK & DAITING SURK

THE COMMISSION & DASTING LTD

Emri i ndërtuesës:

Ndertesa shume banesor Social I, Klinë

Faza e projektimit:

Arkitektura

Emri i vizatimit:

Preria A-A

Punuar nga:

BSe Iriden Seidju

Kontrolluar nga:

IDA Niemza Hoti

11

10/2023

1000

Rishikim:

Shkalla e zvogëlim

kalla e zgjedhimit:


Nr. i fąges:



06




Përshkrimi i renovimit

Ndërrimi i dritareve
Ndërrimi i dyerive

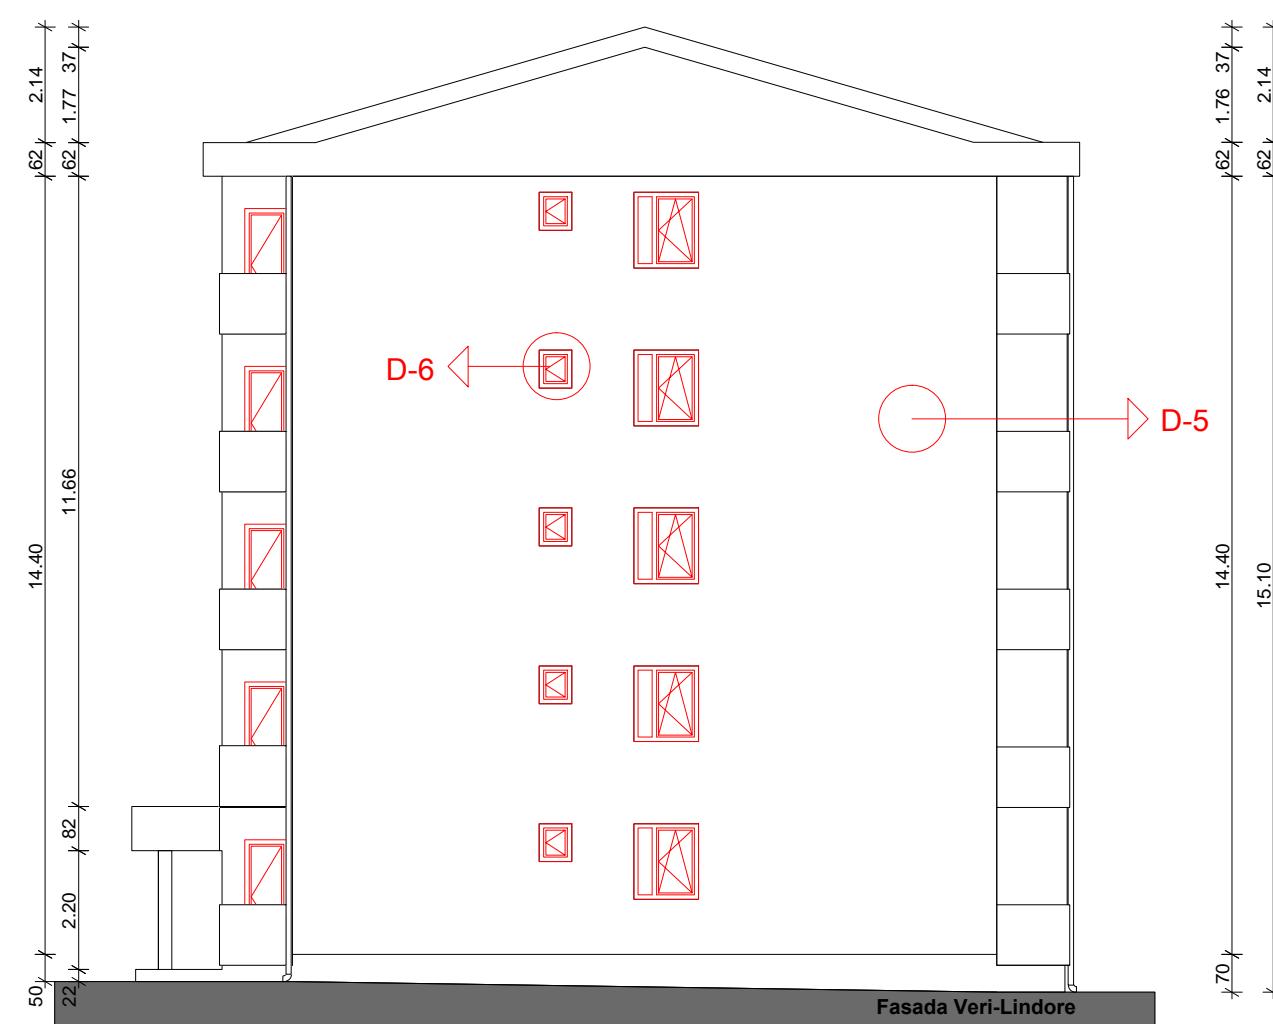


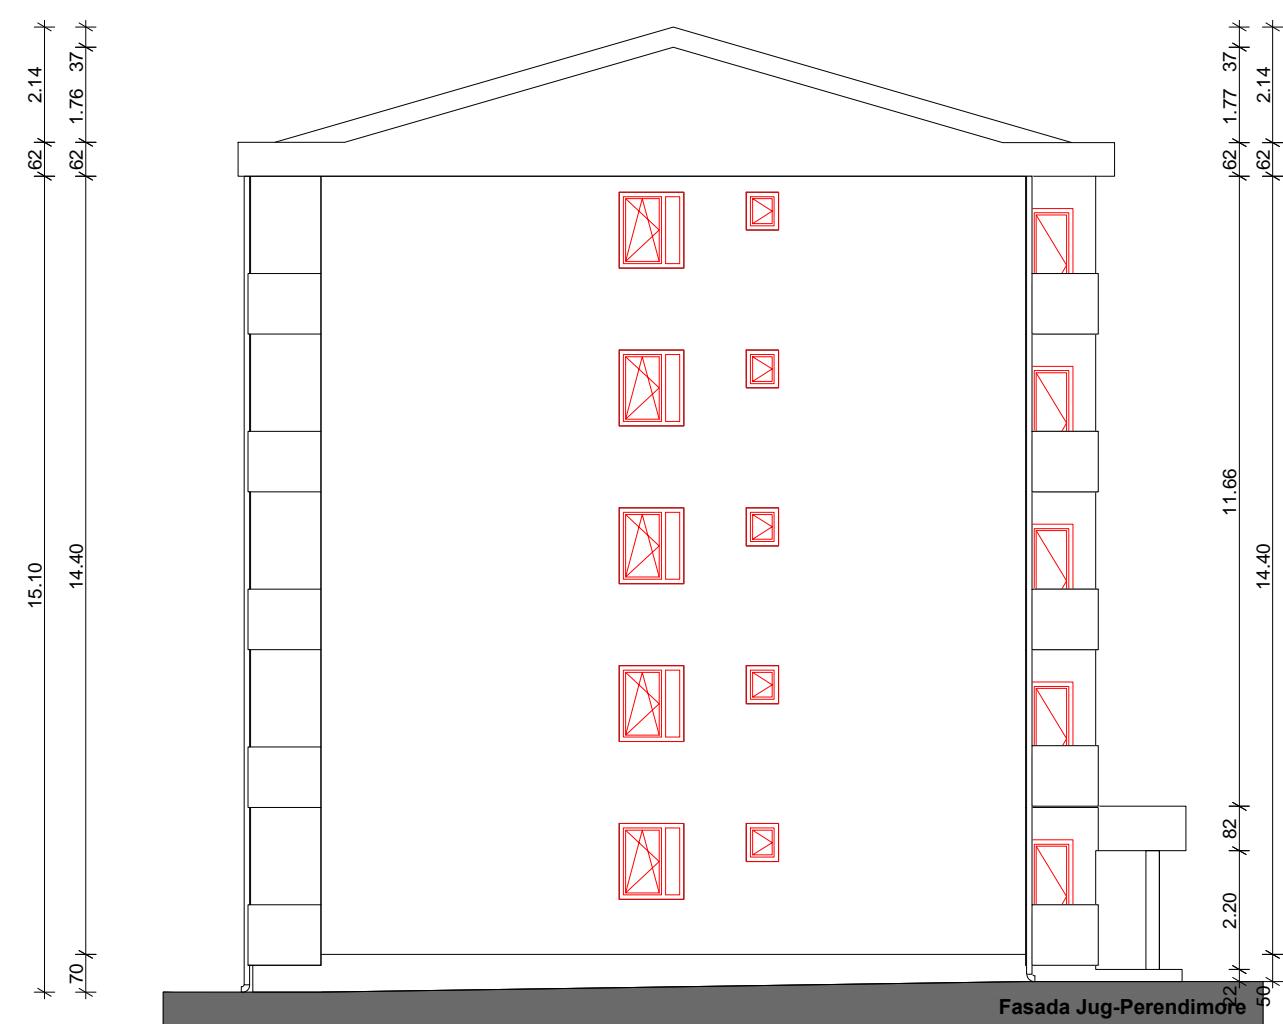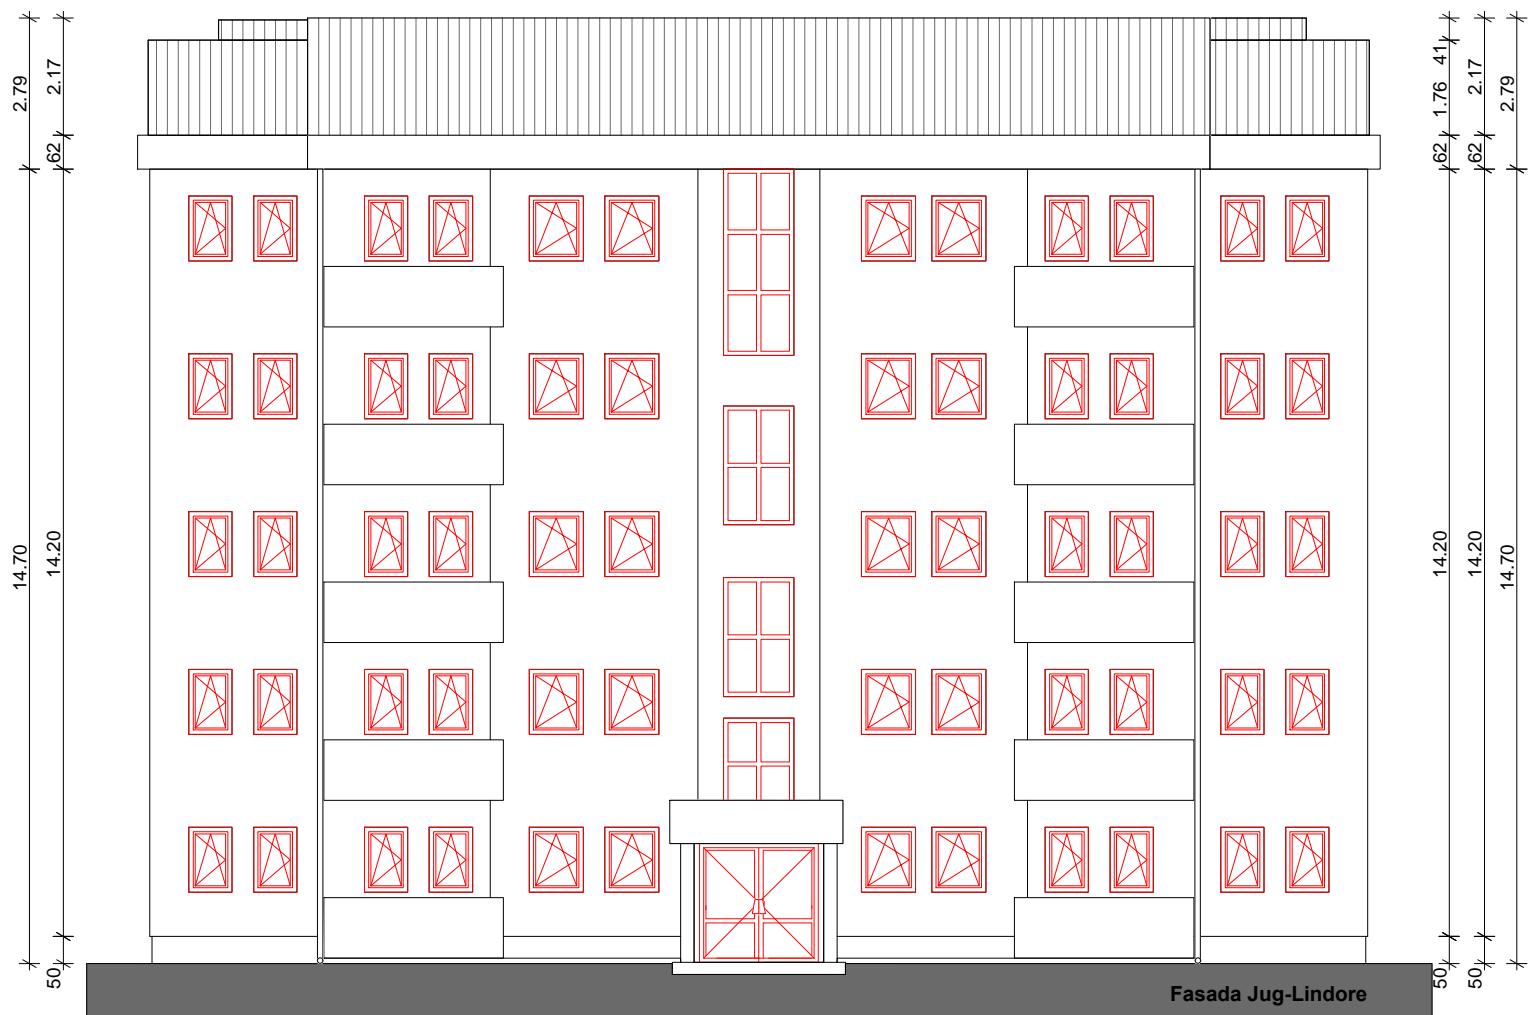


FKEE <small>KOSOVO ENERGY EFFICIENCY FUND</small>	
Projekti:	
Angazhimi i Kompanive pâr kryerie të punëve ndërtimore pâr implementimin e masave të Eficiencës se Enerjisë në ndërtesat shumë banesore sociale	
Nr. Prokurimit : VET-FKEE2020-24-1699-5-1/C70 LOT 5	
Kompania pune kryese	
	ATC COM SHPK & DAITING SHPK npatcom@gmail.com
Emri i ndërtueshës:	
Ndertesa shume banesor Social I, Klinë	
Faza e projektimit:	
Arkitektura	
Emri i vizatimit:	
Fasada Jugore & Perendimore	
Punuar nga: BSc Liridon Sejdiu	Kontrolluar nga: IDA. Njomza Hoti
Date: 10/2023	Rishikim:
Shkalla e zgjedhimit: P=1:100	Nr. i faqes: 08

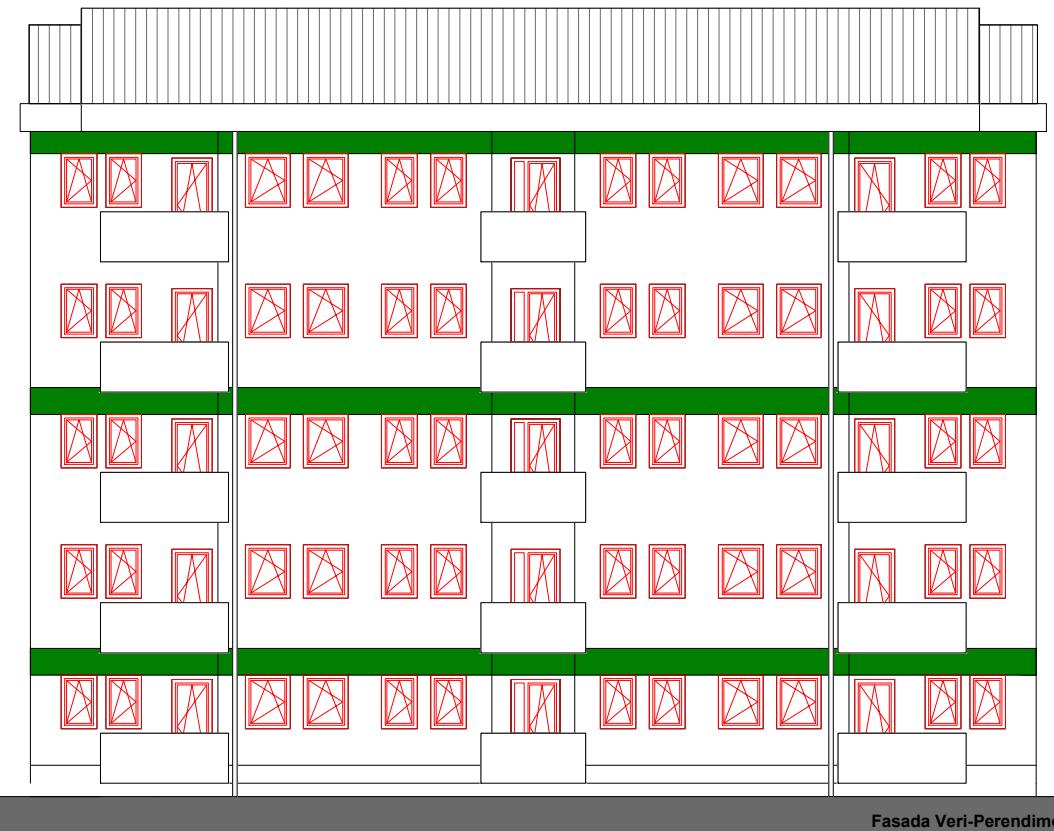


Fasada Veri-Perendimore

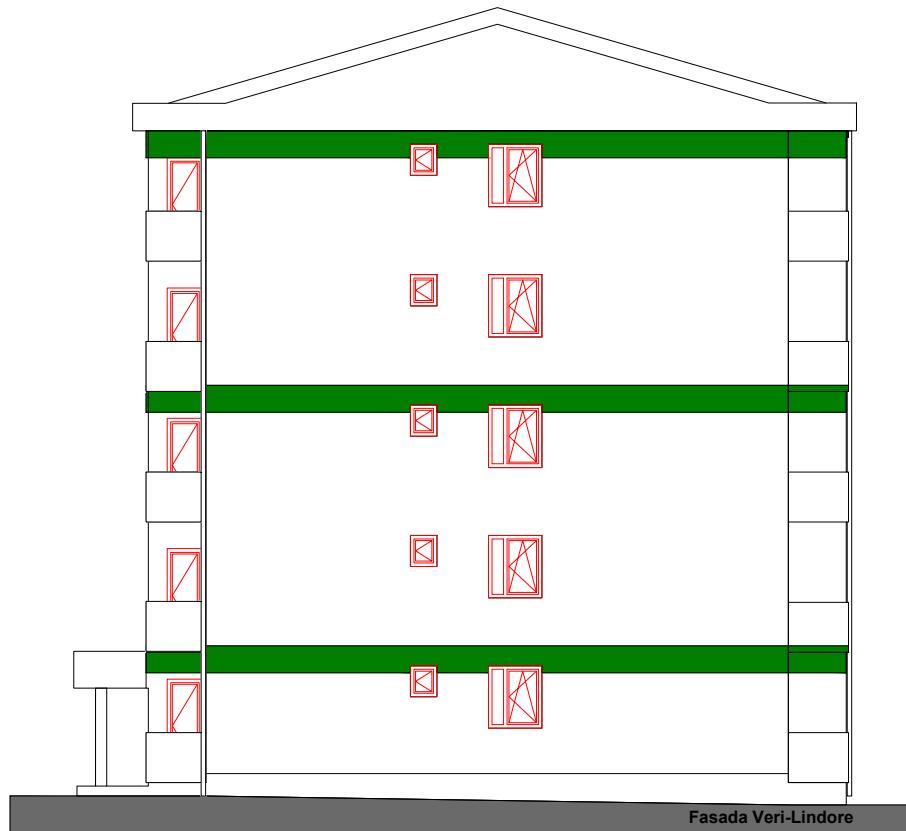

Fasada Veri-Lindore

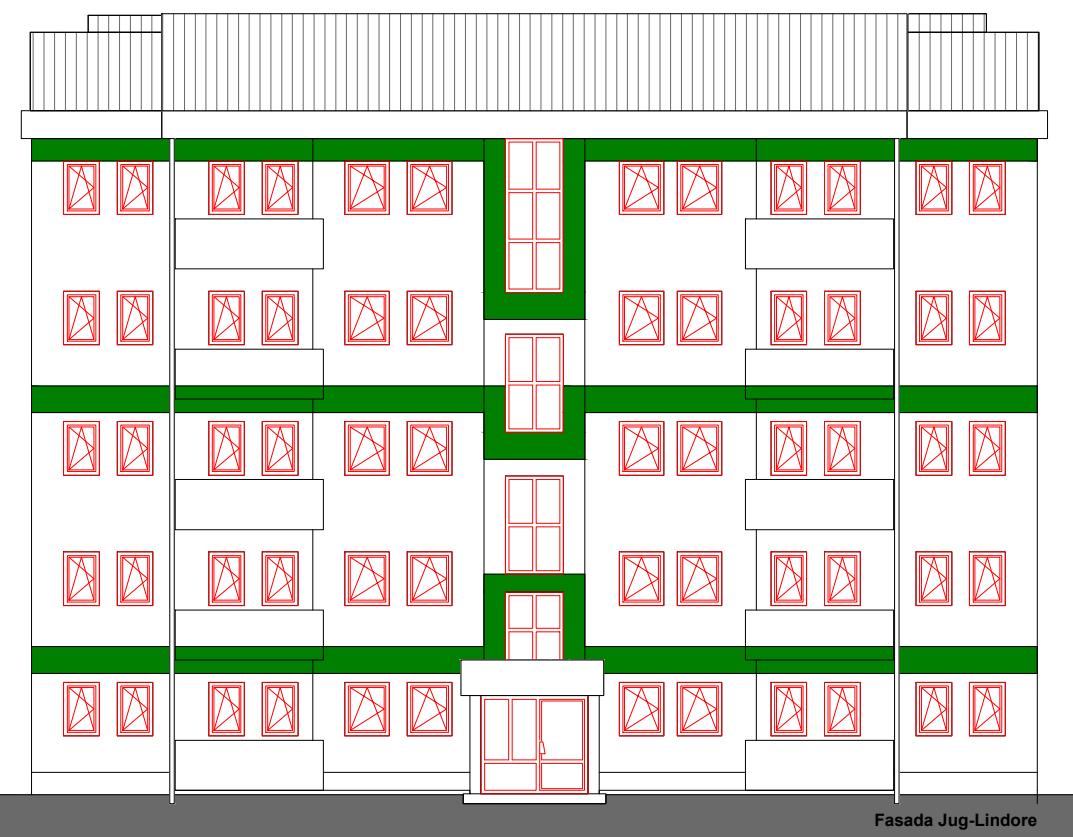

Fasada Jug-Lindore

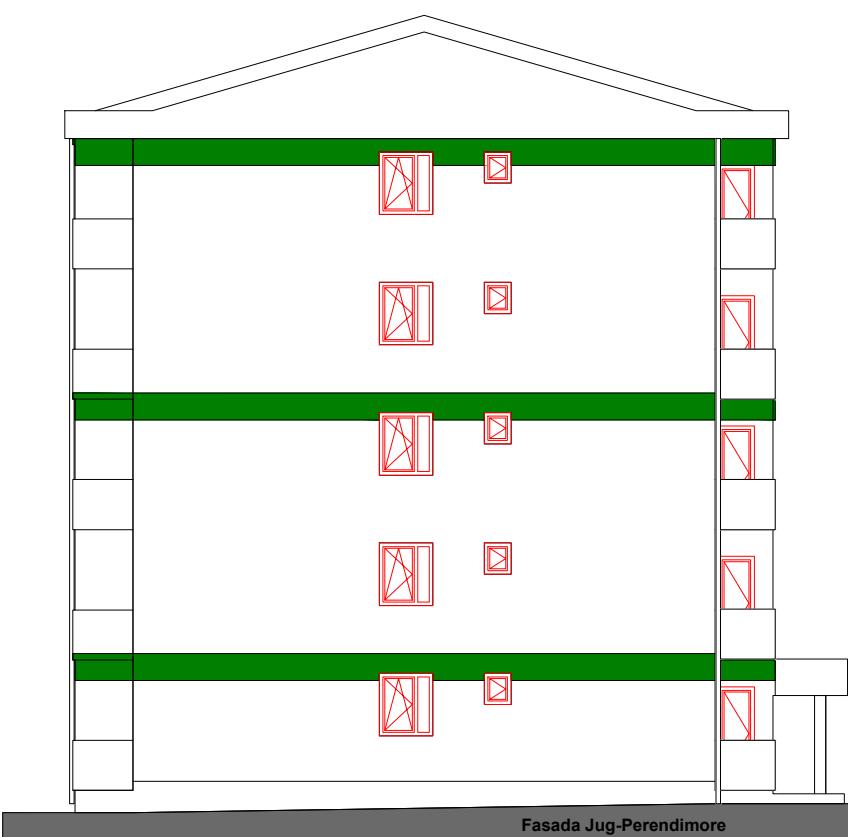

Fasada Jug-Perendimore

Përvizat e përkrahjeve

Termoizolimi i mureve me Lesh Guri $t=12\text{cm}$



Projekti:
Angazhimi i Kompanive pâr kryerie të punëve ndërtimore për implementimin e masave të Eficiencës se Energjisë në ndërtesat shumë banesore sociale

Nr. Prokurimi : VET-FKEE2020-24-1899-5-1-1C70 LOT 5
Kompania pune kyse



Emri i ndertesës:
Ndertesa shume banesor Social I, Klinë

Faza e projektimit:
Arkitektura

Emri i vizatimit:
Mbrojtja ndaj zjarrit

Punuari nga:	Kontrolluar nga:
BSc Liridon Sejdiu	IDA. Njomza Hoti

Date:	Rishikim:
10/2023	

Shkalla e zgjedhimit:	Nr. i fases:
P=1:100	09

Vërejtje: Masat mbrojtëse kundër zjarrit duhet të instalohen në tërë perimetrin e ndërtesës, si unazë me lesh guri dhe lartësi $h=60\text{cm}$ sipas paraqitjeve grafike

SKEMAT E DRITARET TË REJA

Pos_W-1	Pos_W-2	Pos_W-3	Pos_W-4
<p>Pozicioni: W-1, dim. 0.80x1.20m</p>	<p>Pozicioni: W-2, dim. 1.00x1.20m</p>	<p>Pozicioni: W-3, dim. 1.20x1.40m</p>	<p>Pozicioni: W-4, dim. 0.60x0.70m</p>
Sasia: 80	Sasia: 40	Sasia: 10	Sasia: 10

SKEMAT E DRITARET TË REJA

Pos_W-5	Pos_W-6	Pos_W-7	Pos_W-8
<p>Pozicioni: W-5, dim. 0.80x2.10m</p>	<p>Pozicioni: W-6, dim. 1.30x1.70m</p>	<p>Pozicioni: W-7, dim. 0.90x2.10m</p>	<p>Pozicioni: W-8, dim. 1.30x3.45m</p>
Sasia: 10	Sasia: 1	Sasia: 15	Sasia: 1

SKEMAT E DRITARET TË REJA		SKEMAT E DYERVE TË JASHTME		
Pos_W-9	Pos_D-2	Pos_D-1		
<p>Pozicioni: W-9, dim. 1.30x2.20m</p>	<p>Pozicioni: D-2, dim. 1.00x2.10m</p>	<p>Pozicioni: D-1, dim. 2.20x2.20m</p>		
Sasia: 2	Sasia: 25	Sasia: 1		



Projekti:	Angazhimi i Kompanive për kryerje të punave ndërtimore për implementimin e masave të Eficiencës se Energjisë në ndërtesa shumë banesore sociale
Nr. Prokurimi:	VET-FKEE2020-24-1699-5-1-I/C70 LOT 5
Kompania punëkuese	ATC COM SHPK & DAJTING SHPK npatcom@gmail.com
Emri i ndertesës:	Ndertesa shume banesor Social I, Klinë
Faza e projektit:	Arkitektura
Emri i vizitimit:	Skema e dyerve dhe dritarëve
Puruar nga:	Kontrolluar nga: BSc Liridon Sejdiu IDA. Njomza Hoti
Date:	Rishikim: 10/2023 01
Shkalla e zvogëlimit:	Nr. i faqes: P= 1:50 10