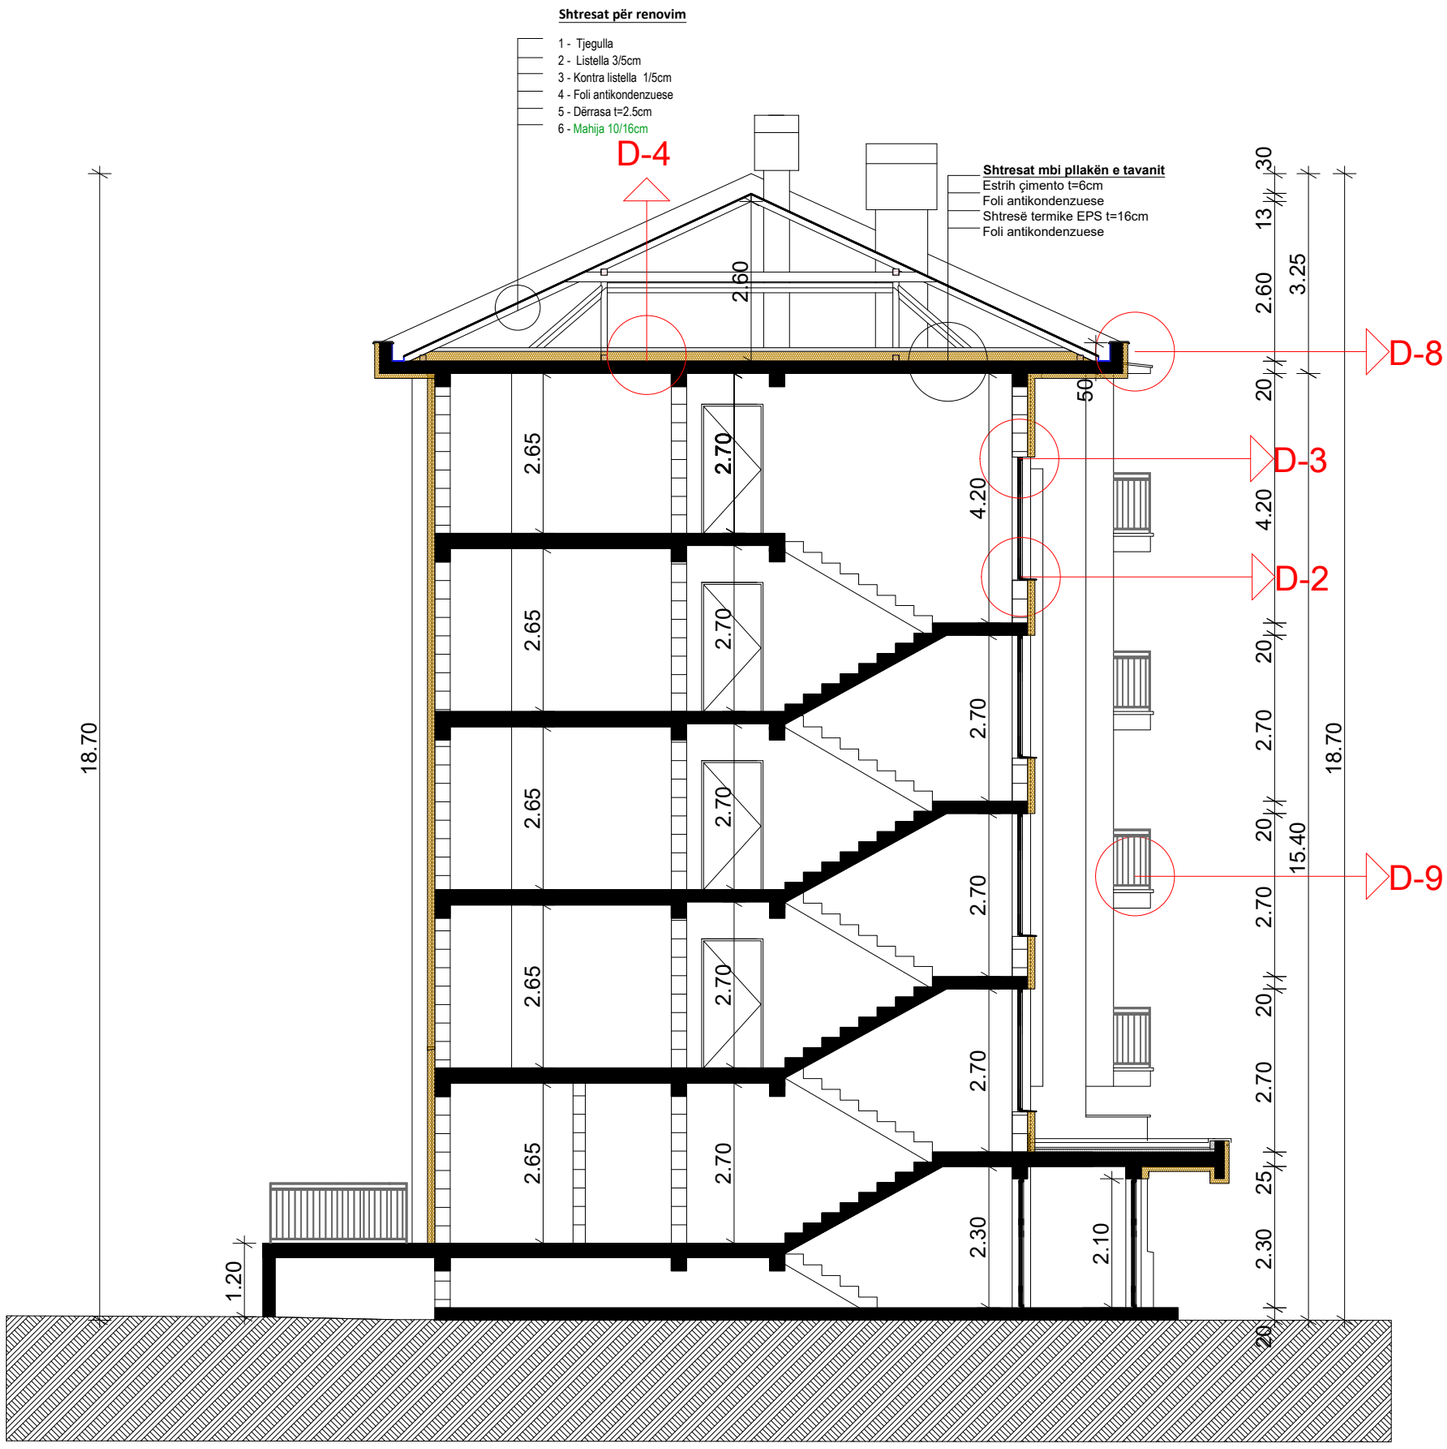

REPUBLIKA E KOSOVËS / REPUBLIC OF KOSOVO
Fondi i Kosovës për Efiçiencë të Energjisë
Kosovo Energy Efficiency Fund

Projekti:

Angazhimi i Kompanive për kryerje të punëve ndërtimore për implementimin e masave të Eficiencës se Energjisë në ndërtesat shumë banesore sociale

Nr. i kontratës: VET-FKEE2020-23-3696-2-1-1/C35_Lot 5

ATC COM SHPK & DAJTING SHPK
nnpatccom@gmail.com

Emri i ndërtesës:
Ndërtesa shumë banesore sociale III, Klinë - Lot 5

Faza e projektimit:
Arkitektura

Emri i vizatimit:
Prerja A-A

Punuar nga:	Kontrolluar nga:
BSc Liridon Sejdiu	**IDA. Njomza Hoti**
Datë: **08/2025**	Rishikim:
Shkalla e zvogëlimit: P=1:100	Nr. i faqes: **07**