

REPUBLIKA E KOSOVËS / REPUBLIC OF KOSOVO
Fondi i Kosovës për Eficiencë të Energjisë
Kosovo Energy Efficiency Fund

Angazhimi i Kompanive pâr kryerje të punëve ndërtimore pâr implementimin e masave të Eficiencës se Energjisë në ndërtesat shumë banesore sociale

Nr. Prokurimit : VET-FKEE2020-24-1699-5-1-C70 Lot 5

Kompania punekryese



ATC COM SHPK & DAJTING SHPK

nnpattcom@gmail.com

Emri i ndërtuesës:

**Ndertesa shume banesor Social I,
Klinë**

Faza e projektit:

Arkitektura

Emri i vizatimit:

Lokacioni i ndërtesës

Punuar nga:
BSc Liridon Sejdiu

Kontrolluar nga:
IDA. Njomza Hoti


Datë:
08/2025

Rishikim:

Shkalla e zvogëlimit:
P=1:100

Nr. i fases:


01

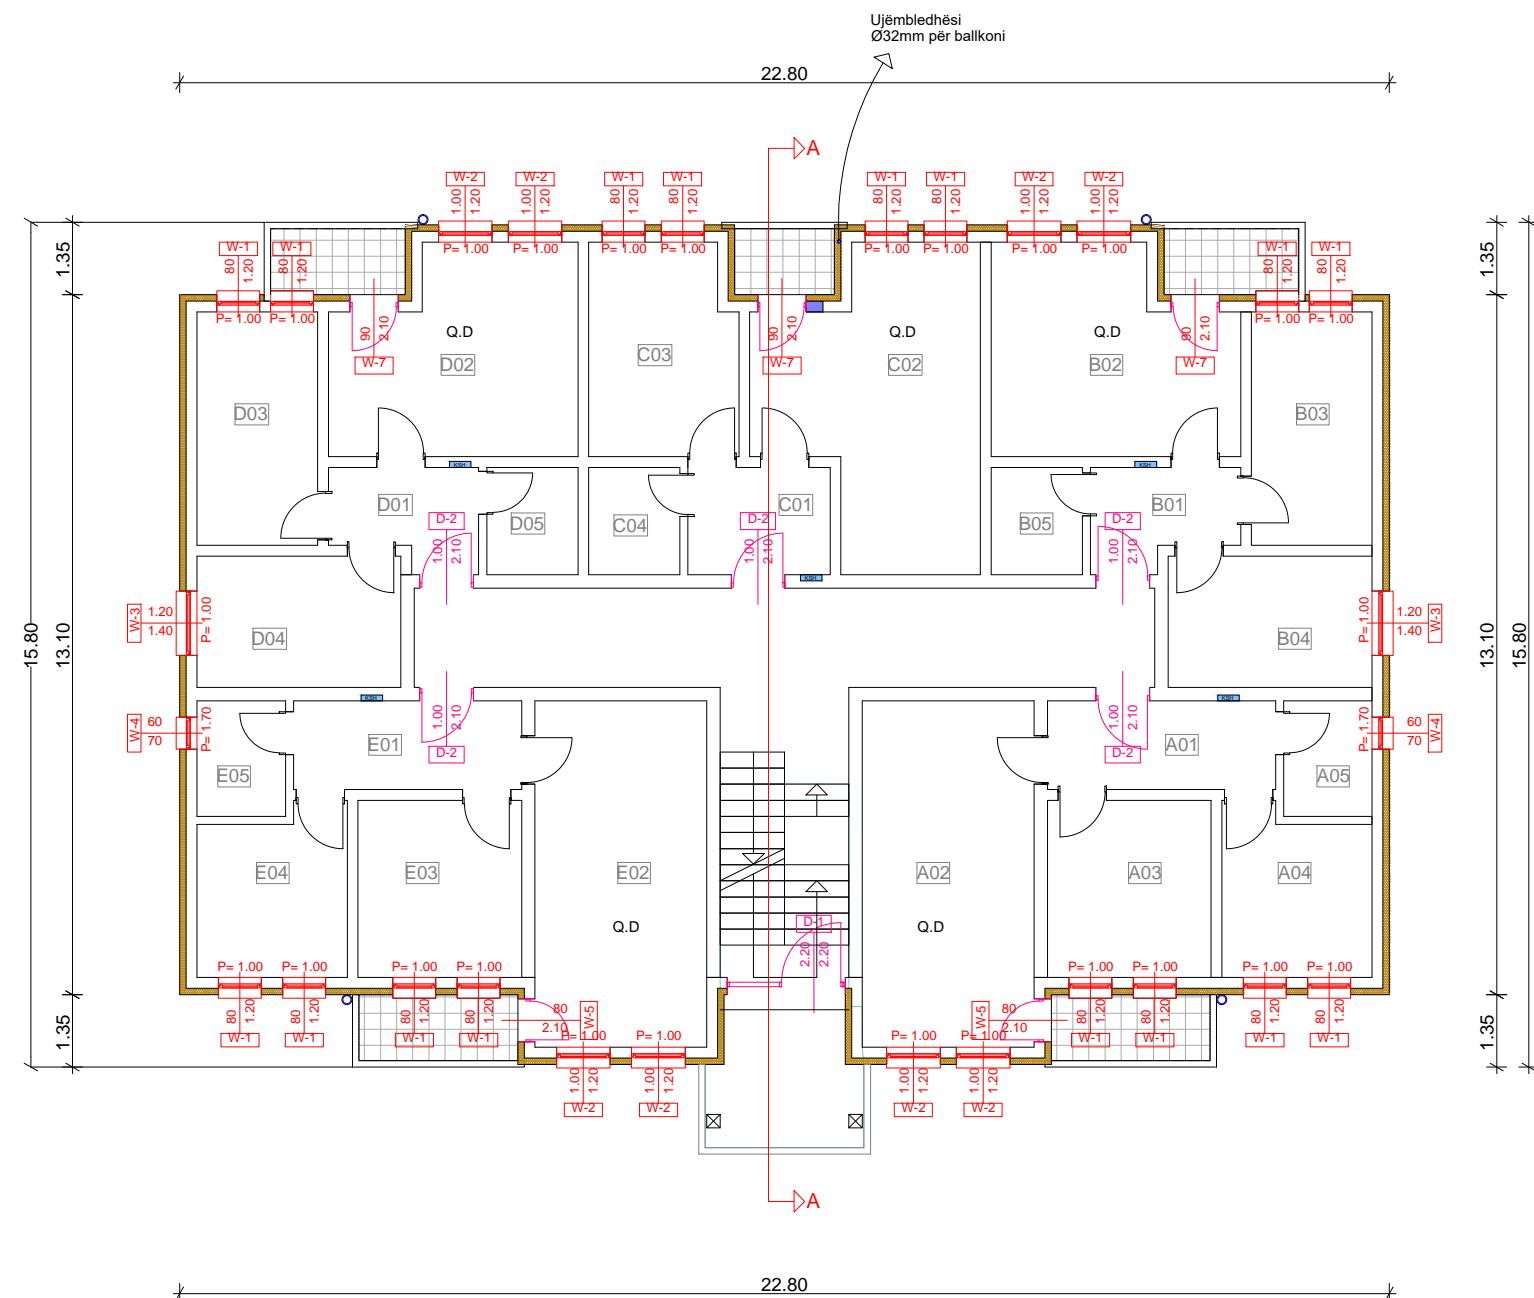

Përshkrimi renovimit

-  Termoizolimi i mureve me EPS t=12cm
 -  Ndërimi i dritareve
 -  Ndërrimi i dyerve
 -  Muratim

 FKEE <small>FONDI I KOSOVËS PËR EKSPERIMENTIMIN DHE INOVACIONIN NË SEKTORIN E ENERGIJES UNIVERSITETI TE TIRANA</small>
REPUBLIKA E KOSOVËS / REPUBLIC OF KOSOVO Fondi i Kosovës për Eficiencë të Energjisë Kosovo Energy Efficiency Fund

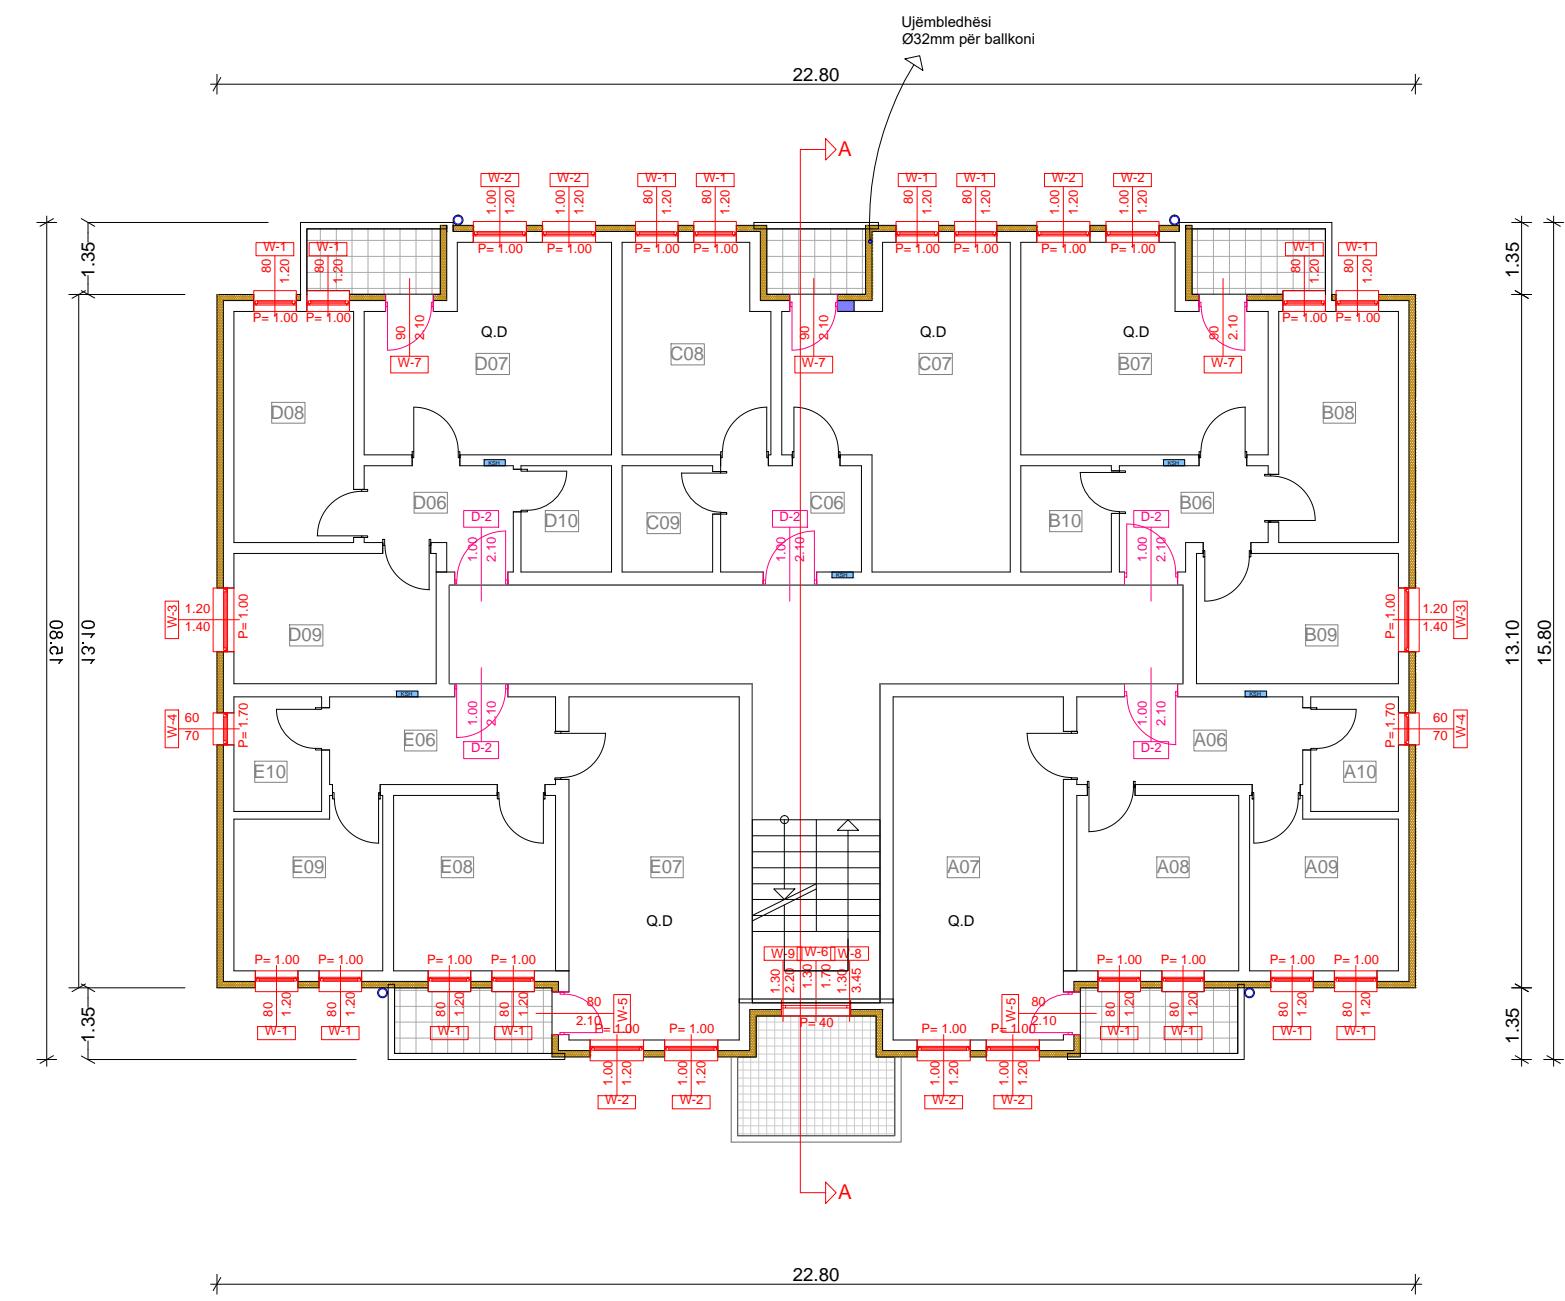

Përshkrimi renovimit

-  Termoizolimi i mureve me EPS t=12cm
 -  Ndërrimi i dritareve
 -  Ndërrimi i dyerve
 -  Renovimi i strehes te hryja
 -  Mur i ri

Projekti:
Angazhimi i Kompanive pâr kryerje të punëve ndërtimore pér implementimin e masave të Eficiencës se Energjisë në ndërtesa shumë banesore sociale

Nr. Prokurimit : VET-EKEE2020-24-1699-5-1-1/C70 LOT 5



ATC COM SHPK & DAJTING SHPK

Emri i ndërtesës:

Ndertesa shume banesor Social I,

Faza e projektimit:

1

Kati I - IV

Punuar nga:
BSc Liridon Seidiu



Kontrolluar nga:
IDA Niomza Hoti

DATA

Date.	08/2025	KUASHKIMI:
Shkalla e zvogëlimit:	Nr. i faqes:	

P=1:100

03

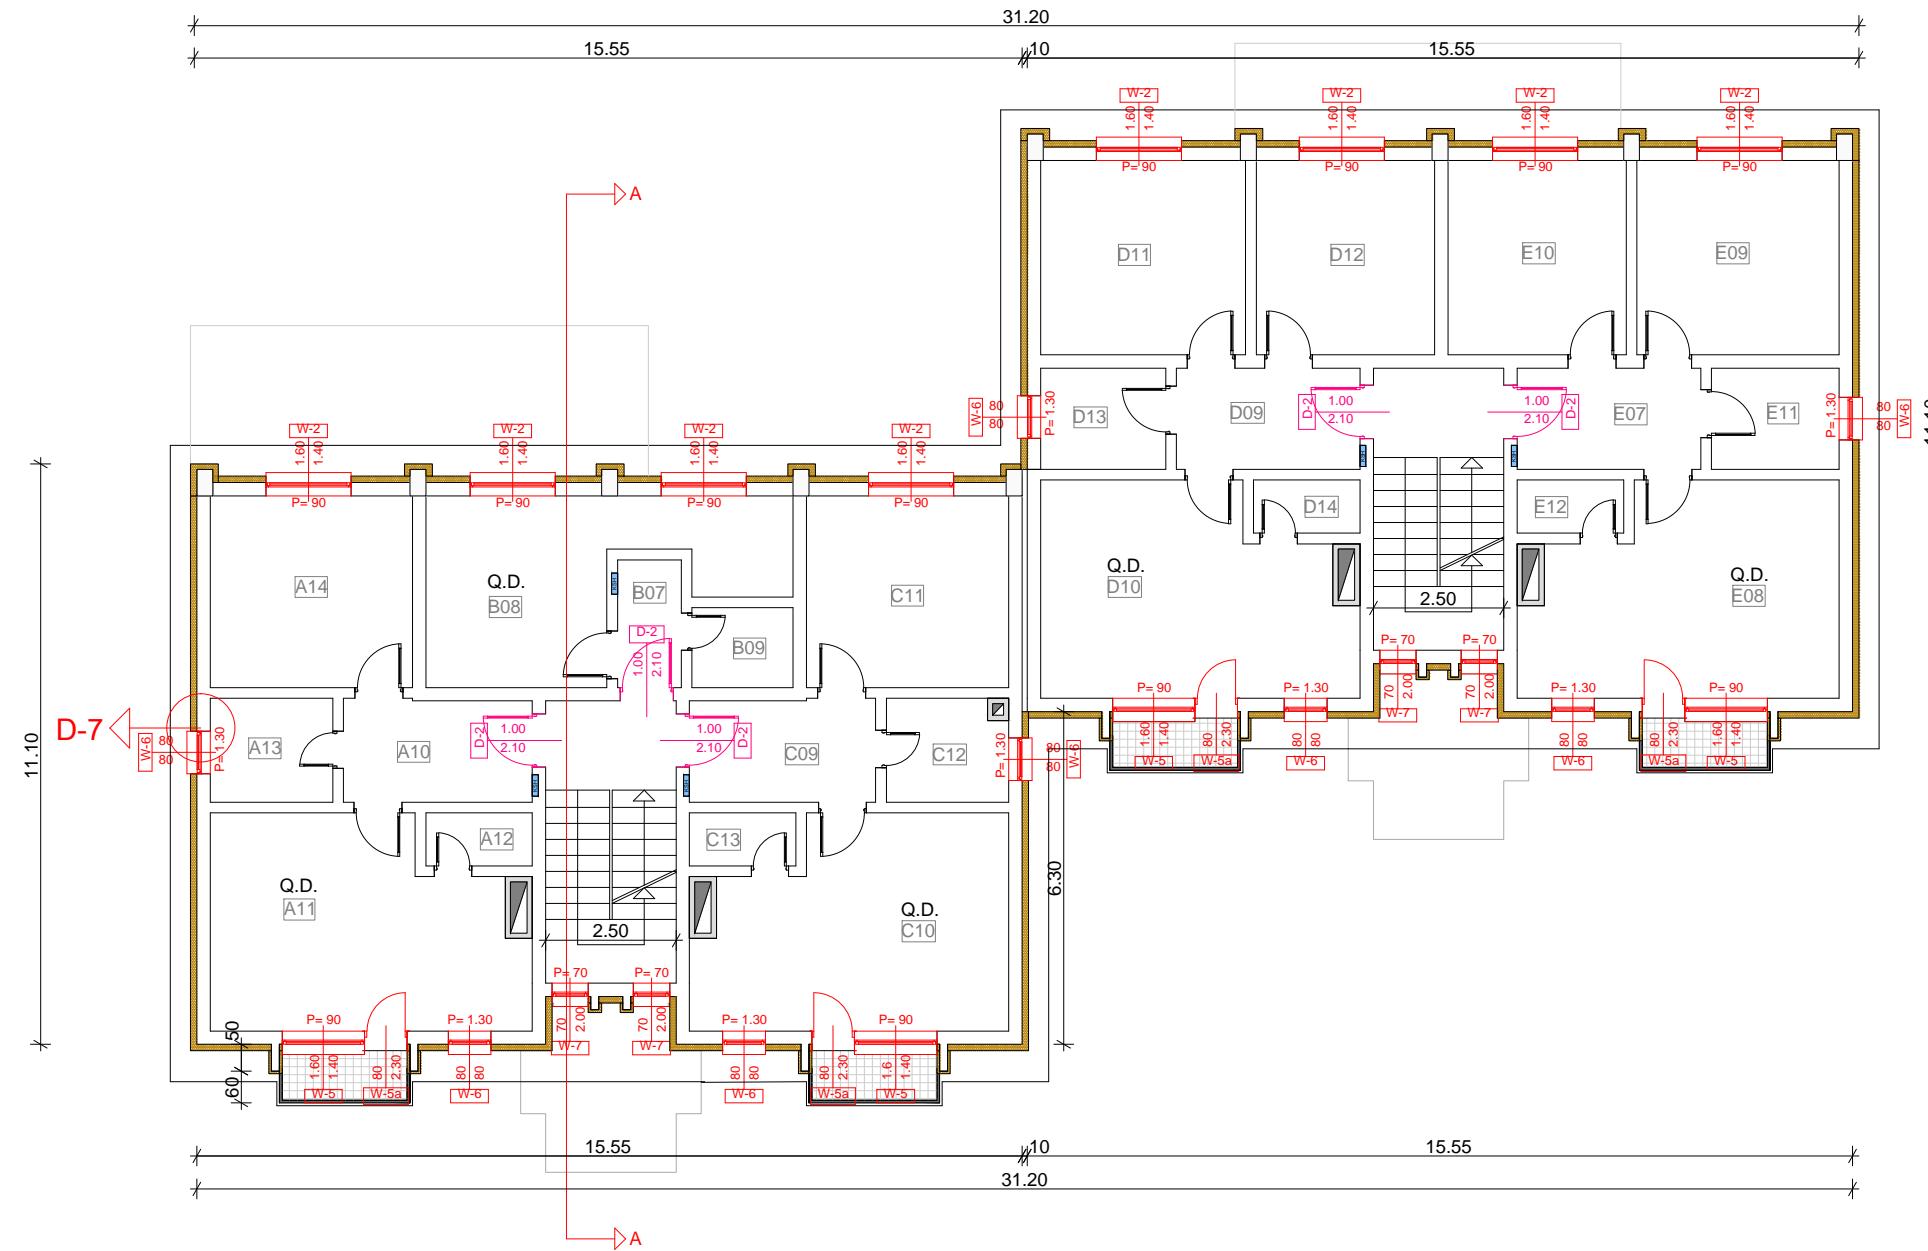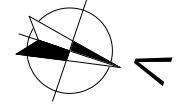

Përshkrimi i renovimit

-  Termoizolimi i mureve me EPS t=12cm
 -  Ndërrimi i dritareve
 -  Ndërrimi i dyverve
 -  Renovimi i ballkoneve



Projekti:
Angazhimi i Kompanive pâr kryerje të punëve ndërtimore pér implementimin e masave të Eficiencës se Enerjisë në ndërtesat shumë hanesore sociale



ATC COM SHPK & DAJTING SHPK

Ndërtesa shumë-banesore sociale II_15,

Faza e projektimit:


Emri i vizatimit:

Punuar nga:
PC. Lihiwa Saiti

Kontrolluar nga:
IDA. Niamea Uati

Datě: 10/2023	Rishikim:
------------------	-----------



P=1:100 04

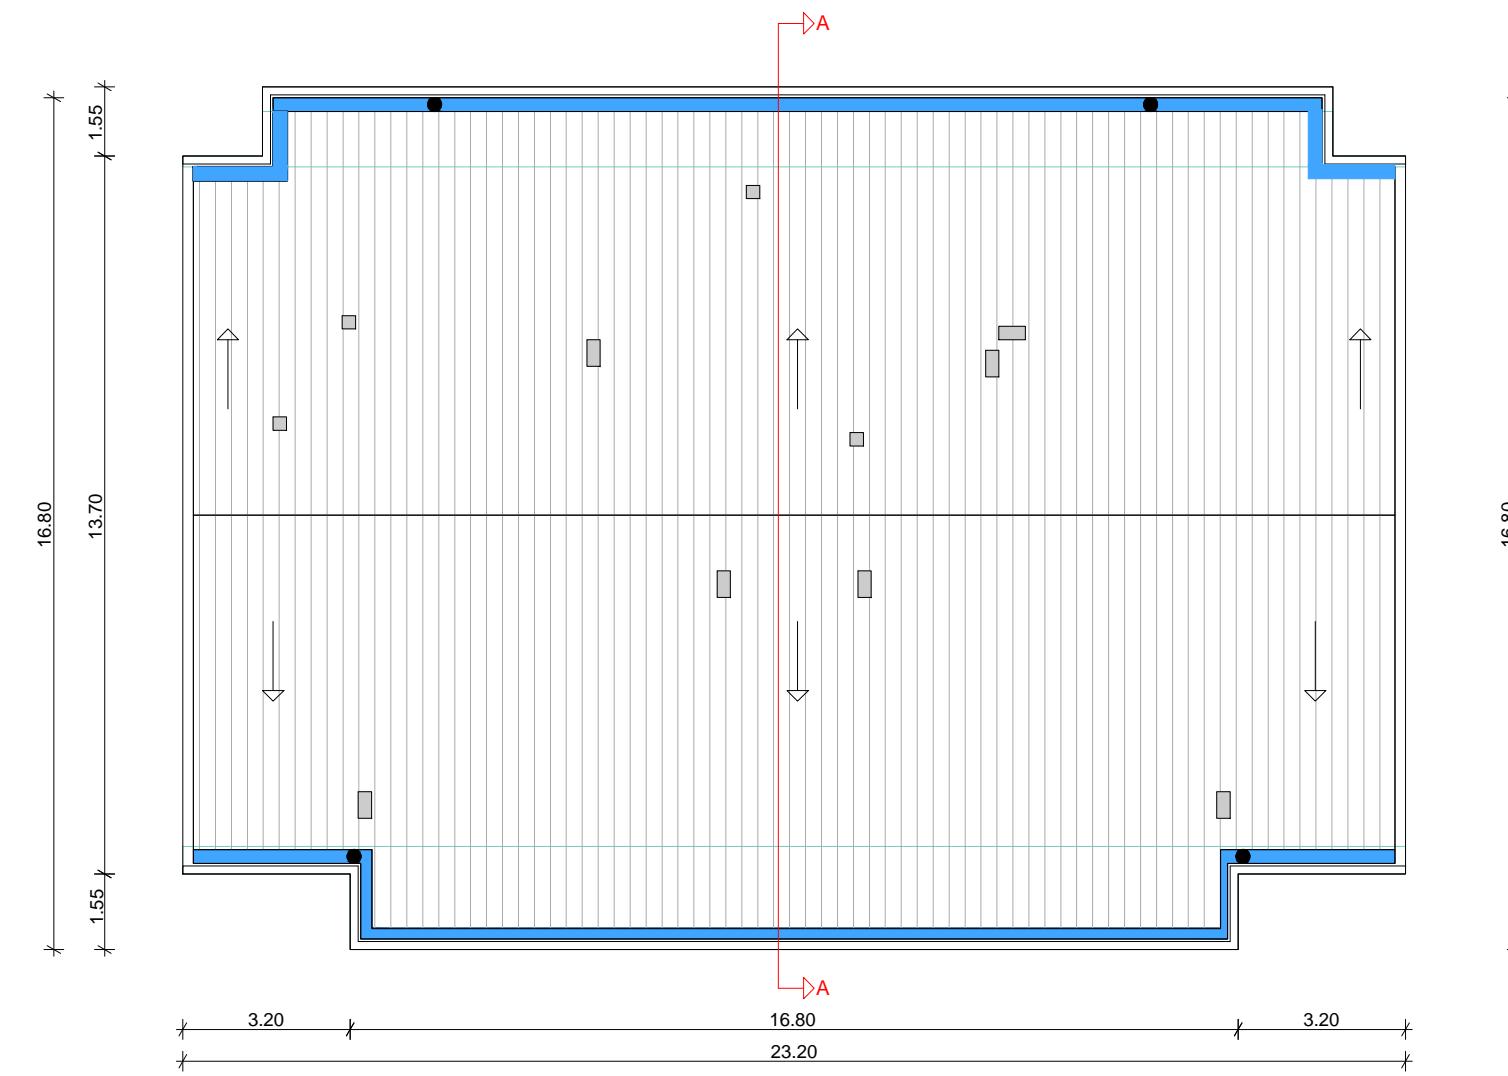

Përvizimi renovimit

- Ndërrimi i mbulesës dhe termoizolimi i kulmit me EPS t=16cm
- Ndërrimi i ulluqeve horizontale
- Ndërrimi i ulluqeve vertikale

	FKEE FONDI KOSOVAR PER EFEKËNCË TË ENERGIJE [®] Fond i Kosovës per Eficiencë të Energjise Kosovo Energy Efficiency Fund
Projekti: Angazhimi i Kompanive për kryerje të punëve ndërtimore për implementimin e masave të Eficiencës se Energjisë ne ndertesat shumë banesore sociale	
Nr. Prokurimit : VET-FKEE2020-24-1699-5-1/C70 LOT 5	
Kompania punëkryese	
	ATC COM SHPK & DAJTING SHPK npatcom@gmail.com
Emri i ndertesës: Ndertesa shume banesor Social I, Klinë	
Faza e projektit: Arkitektura	
Emri i vizatimit: Kulmi	
Punuar nga: BSc Liridon Sejdiu	Kontrolluar nga: IDA. Njomza Hoti
Dati: 08/2025	Rishikim:
Shkalla e zvogëlimit: P:1:100	Nr. i faqes: 04

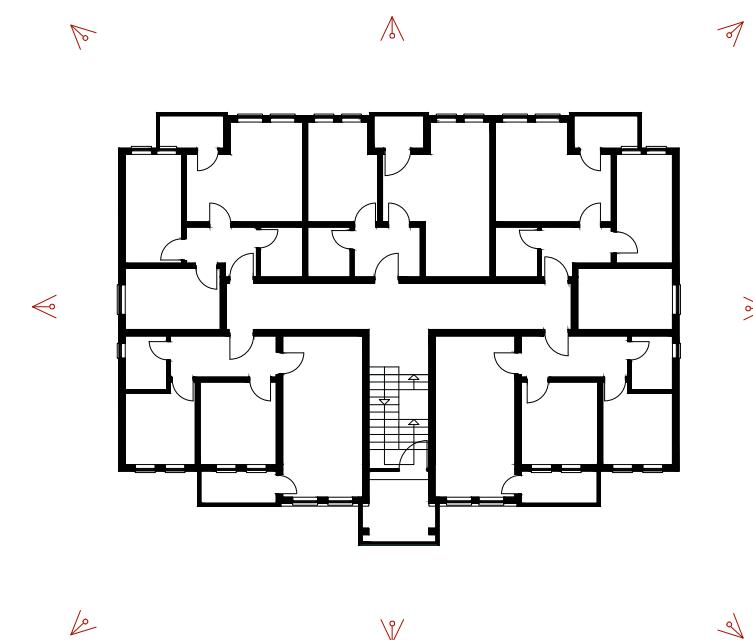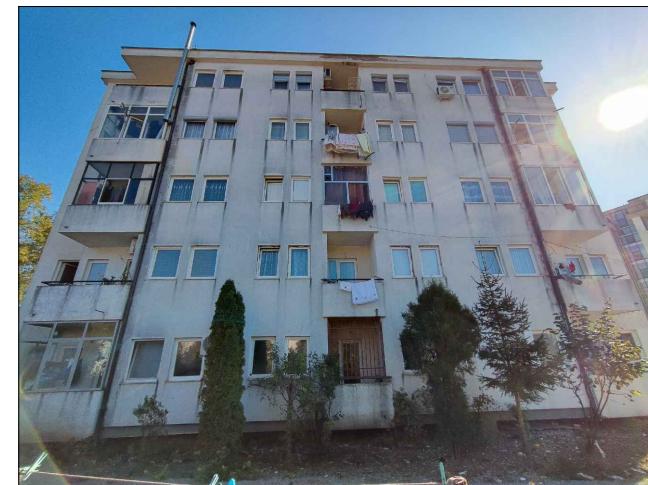

	FKEE FONDI I KOMBËTARE I EKSEGJECUTIVIT TË ENERGIJES KOSOVSKI FONDI ZA ENERGETIKU PËR SHQIPSHOR Kosovo Energy Efficiency Fund
REPUBLIKA E KOSOVËS / REPUBLIC OF KOSOVO	
Fondi i Kosovës për Eficiencë të Energjisë	
Kosovo Energy Efficiency Fund	

Projekti:

Angazhimi i Kompanive për kryerje të punëve ndërtimore për implementimin e masave të Eficiencës se Energjisë në ndërtesat shumë banesore sociale

Nr. Prokurimit : VET-FKEE2020-24-1699-5-1-1/C70 LOT 5

Kompania punekryese



ATC COM SHPK & DAJTING SHPK

nnpatccom@gmail.com

Emri i ndërtesës:

**Ndertesa shume banesor Social I,
Klinë**

Faza e projektimit:

Arkitektura

Emri i vizitimit:

Fotot e ndërtesës

Punuar nga:

BSc Liridon Sejdiu

Kontrolluar nga:

IDA. Njomza Hoti

Datë:

08/2025


Rishikim:

Shkalla e zvogëlimit:

P=1:100

Nr. i fases:

05

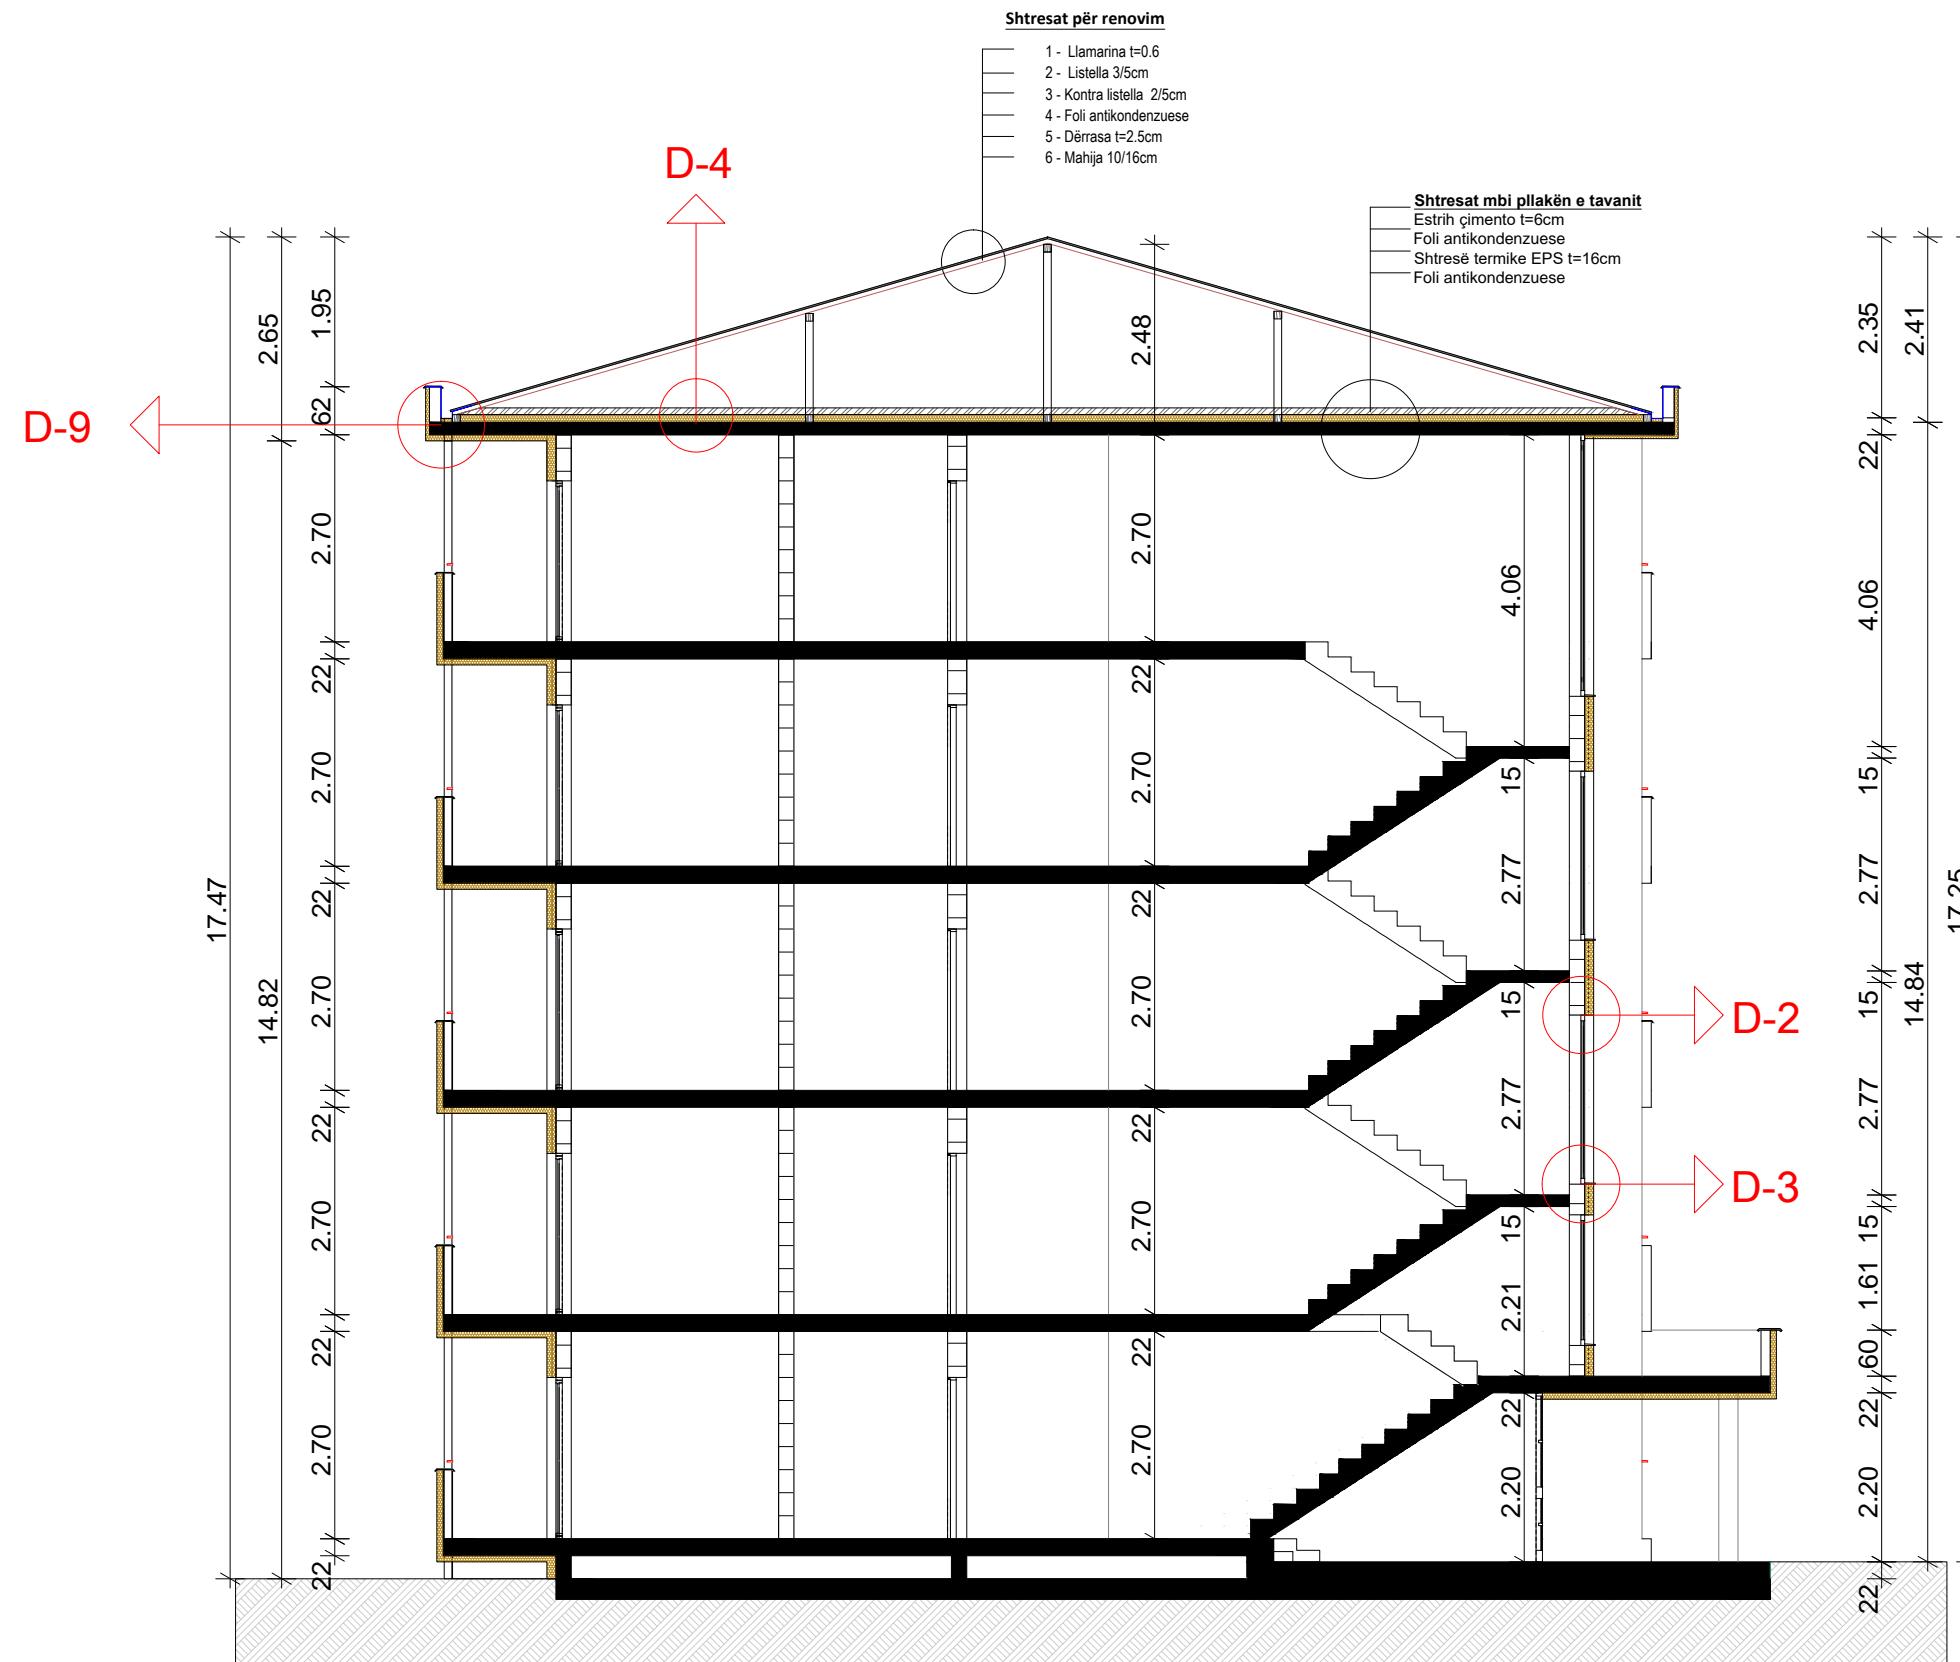

REPUBLIKA E KOSOVËS / REPUBLIC OF KOSOVO
Fondi i Kosovës për Eficiencë të Energjisë
Kosovo Energy Efficiency Fund

Projekti

Angazhimi i Kompanive păr kryerje të punëve ndërtimore pér implementimin e masave të Eficiencës se Enerqisë në ndërtesat shumë banesore sociale

Nr. Prokurimit : VET-FKEE2020-24-1699-5-1-1/C70 LOT 5

Kompania punekryse



ATC.COM SLIPK & DAITING SLIPK

AT&T COMM R&D ASTORIA

Emri i ndërtuesës:

Ndertesa shume banesor Social I, Klinë

Faza e projektimit

Arkitektura

Emri i vizitimit:

Preria A-A

Punuar nga:
BSc Liridon Seidiu

Kontrolluar nga:
IDA. Njomza Hoti

Datë: 08/

Rishikim:

Shkalla e zvogëlimit:

Nr. i faqes:


ANSWER



— 1 —







Përshkrimi i renovimit

 Ndërrimi i dritareve
 Ndërrimi i dyerive

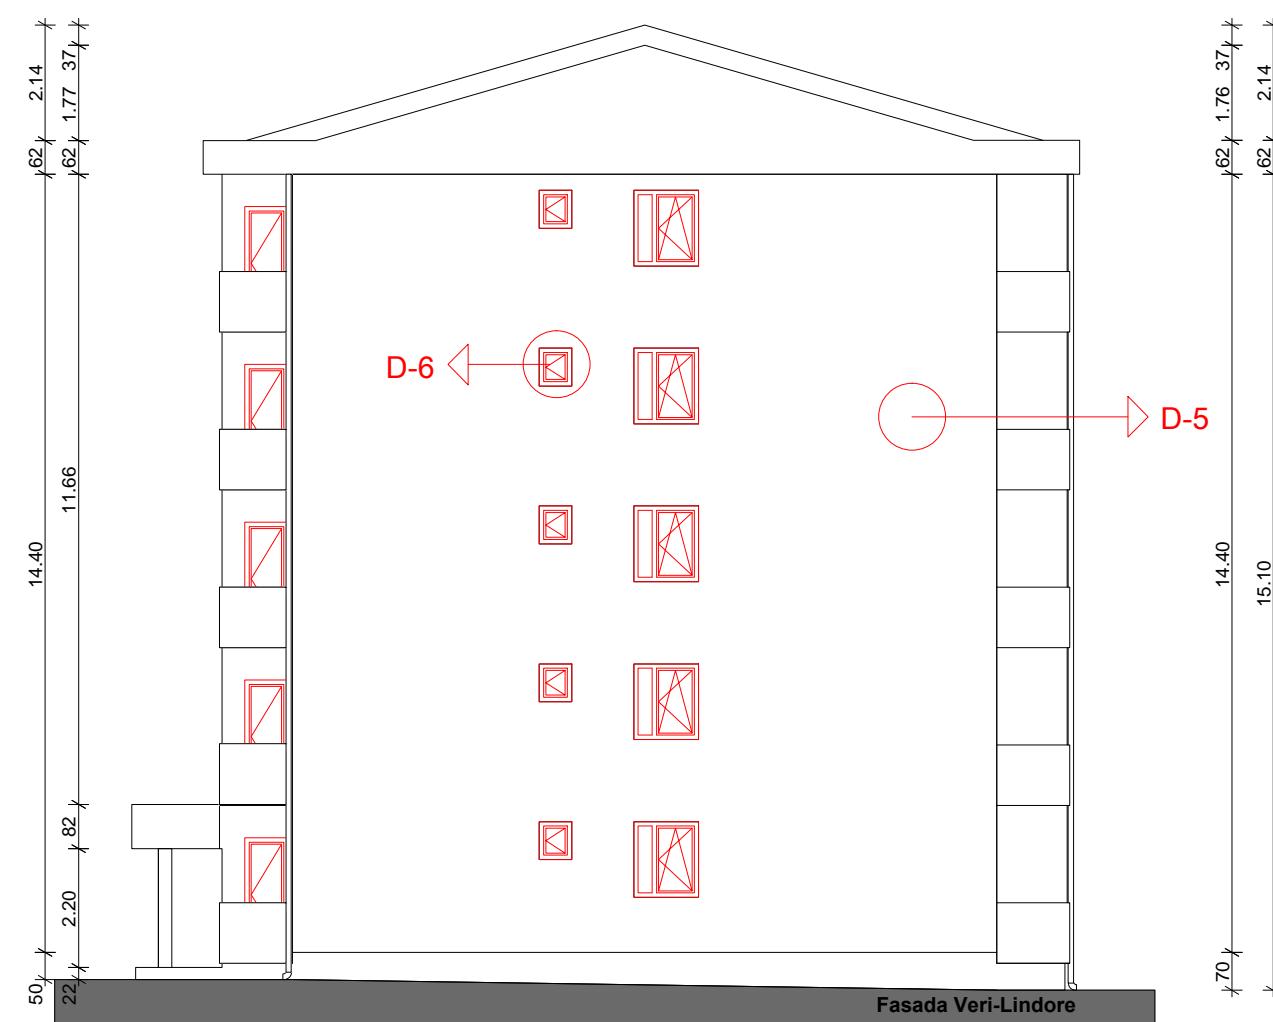

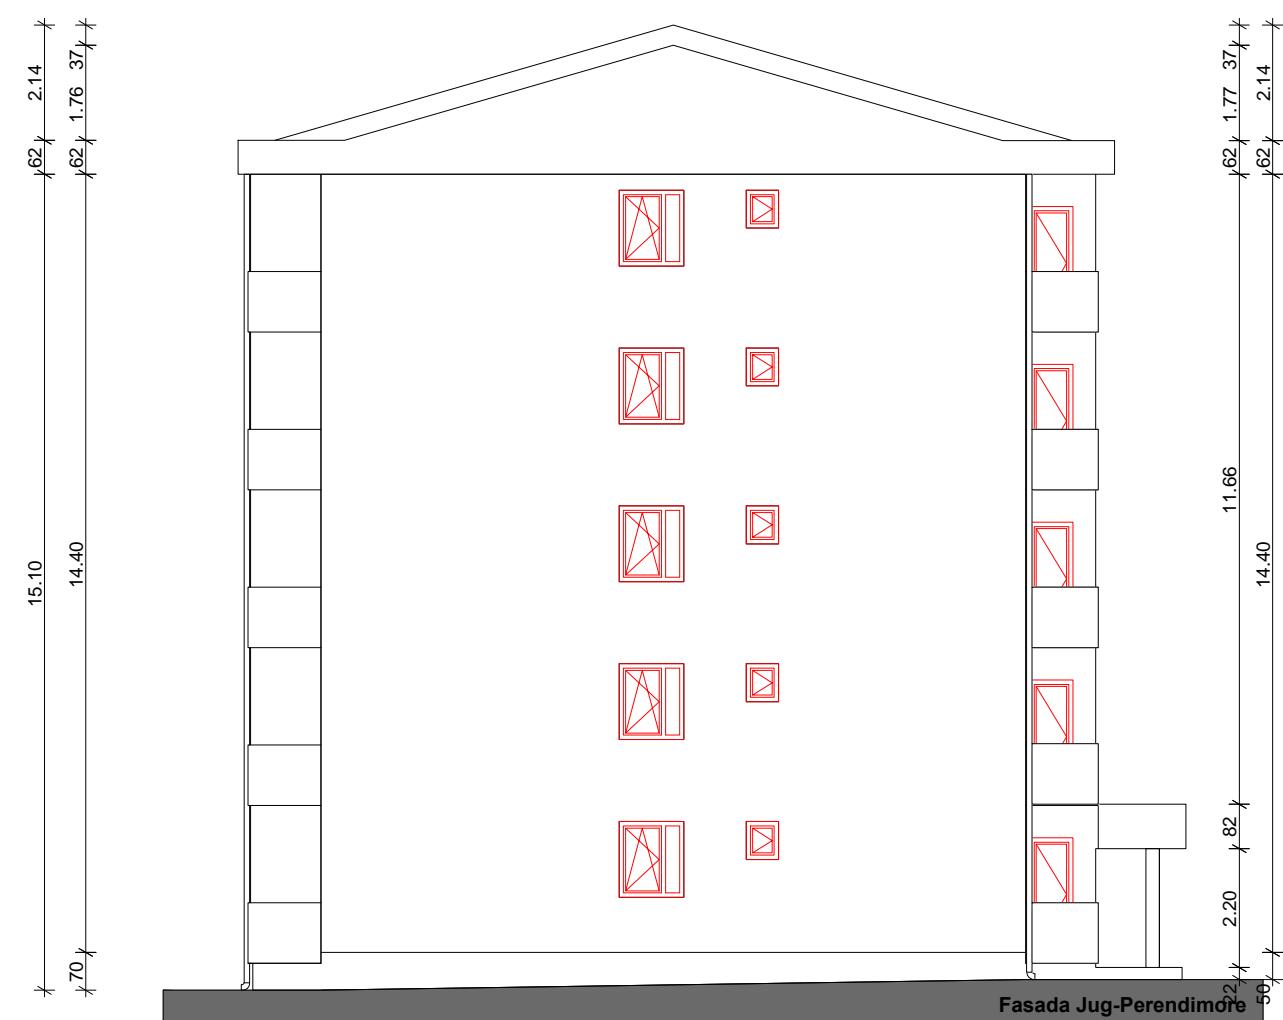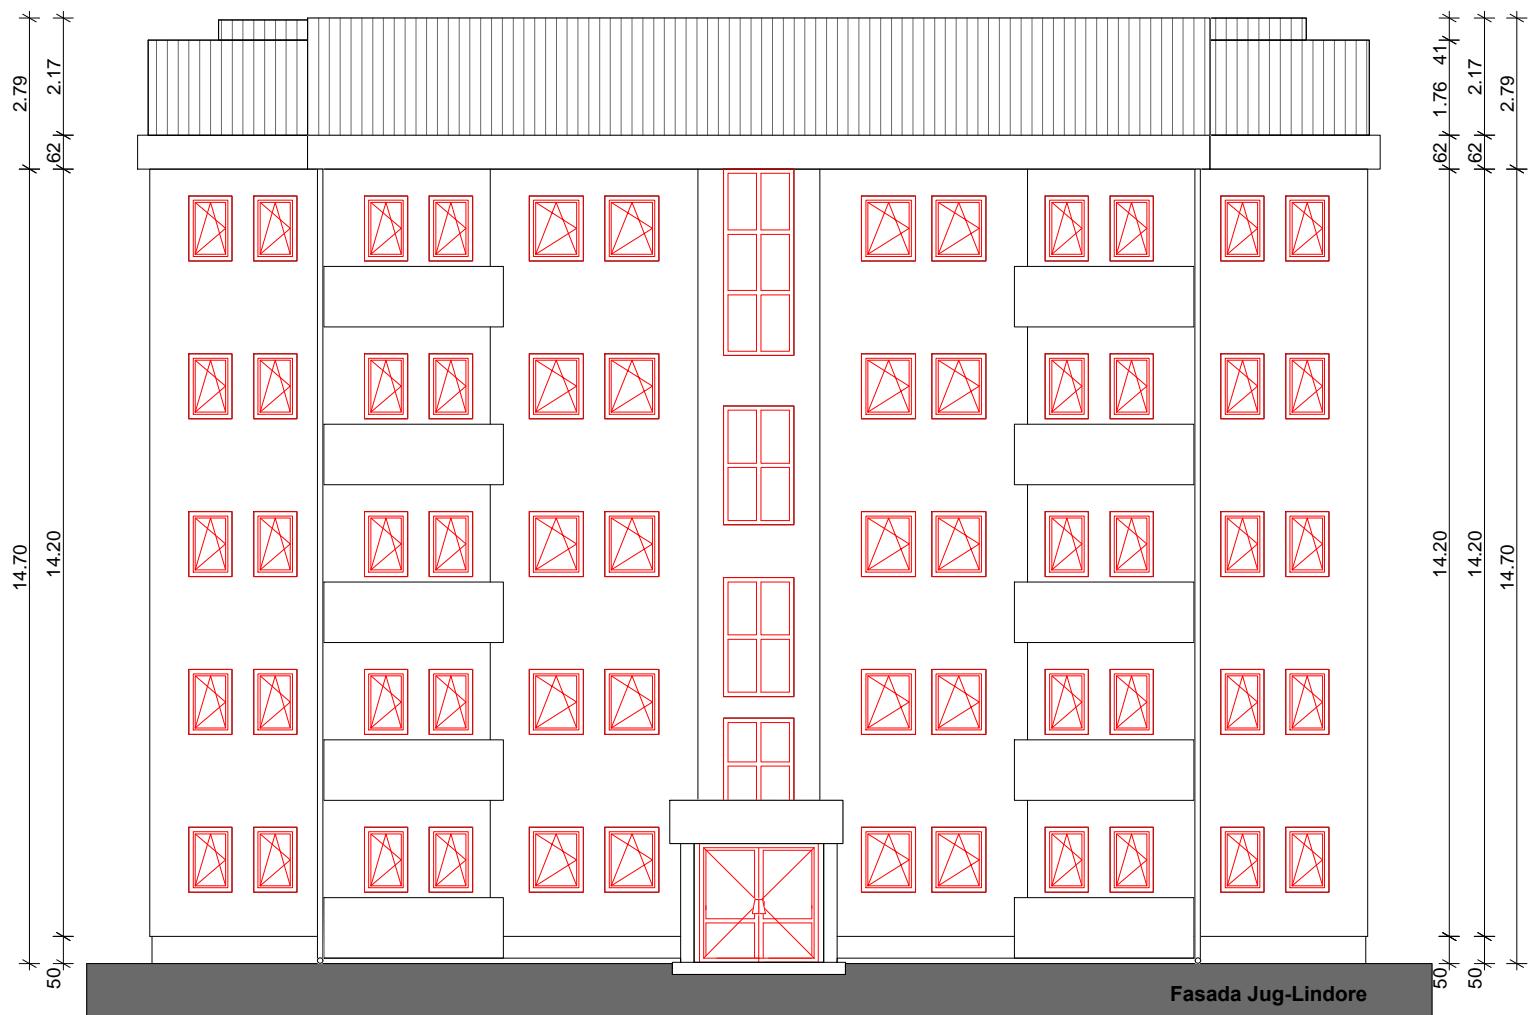

FKEE <small>KOSOVO ENERGY EFFICIENCY FUND</small>	
Projekti:	
Angazhimi i Kompanie pâr kryerie tê punëve ndërtimore pâr implementimin e masave të Eficiencës se Enerjise në ndërtesat shumë banesore sociale	
Nr. Prokurimit : VET-FKEE2020-24-1699-5-1/C70 LOT 5	
Kompania pune kryese	
	ATC COM SHPK & DAITING SHPK npatcom@gmail.com
Emri i ndërtueshës:	
Ndertesa shume banesor Social I, Klinë	
Faza e projektimit:	
Arkitektura	
Emri i vizatimit:	
Fasada Jugore & Perendimore	
Punuar nga:	Kontrolluar nga:
BSc Liridon Sejdiu	IDA. Njomza Hoti
Date:	Rishikim:
08/2025	
Shkalla e zgjedhimit:	Nr. i fakes:
P=1:100	08

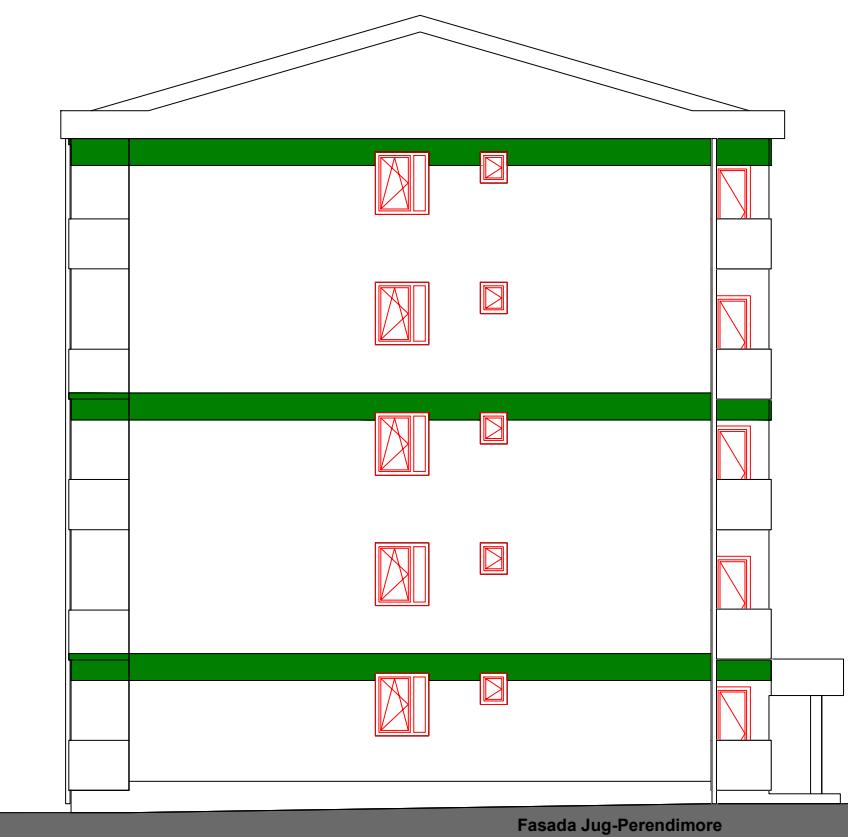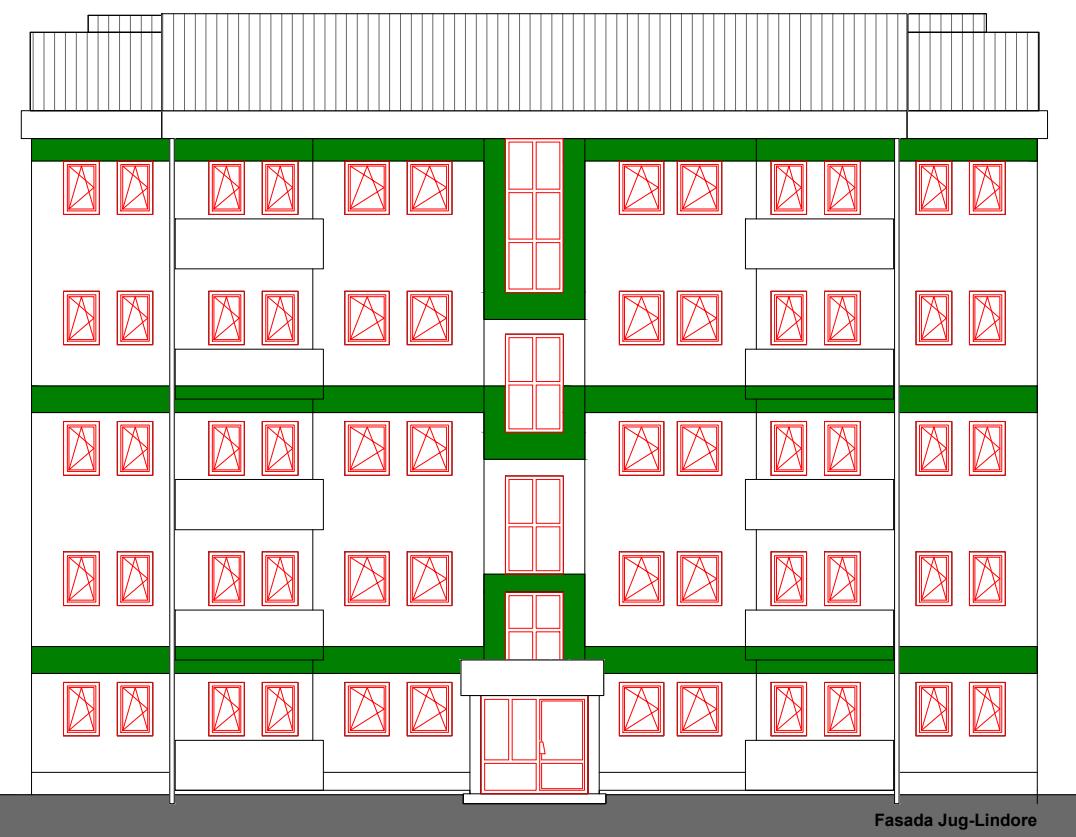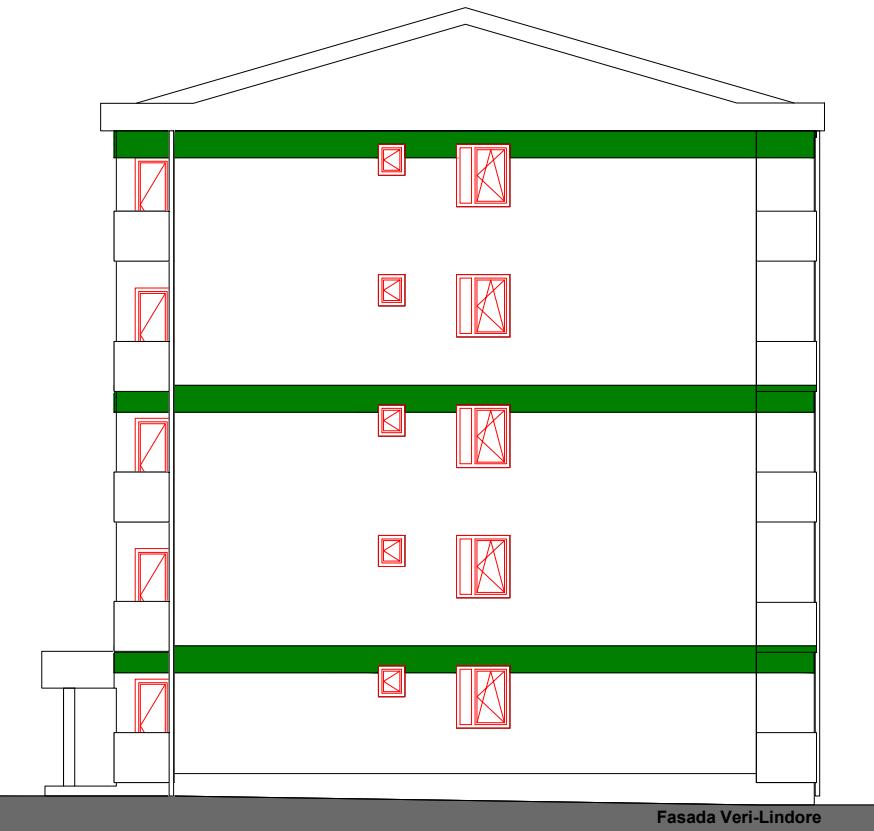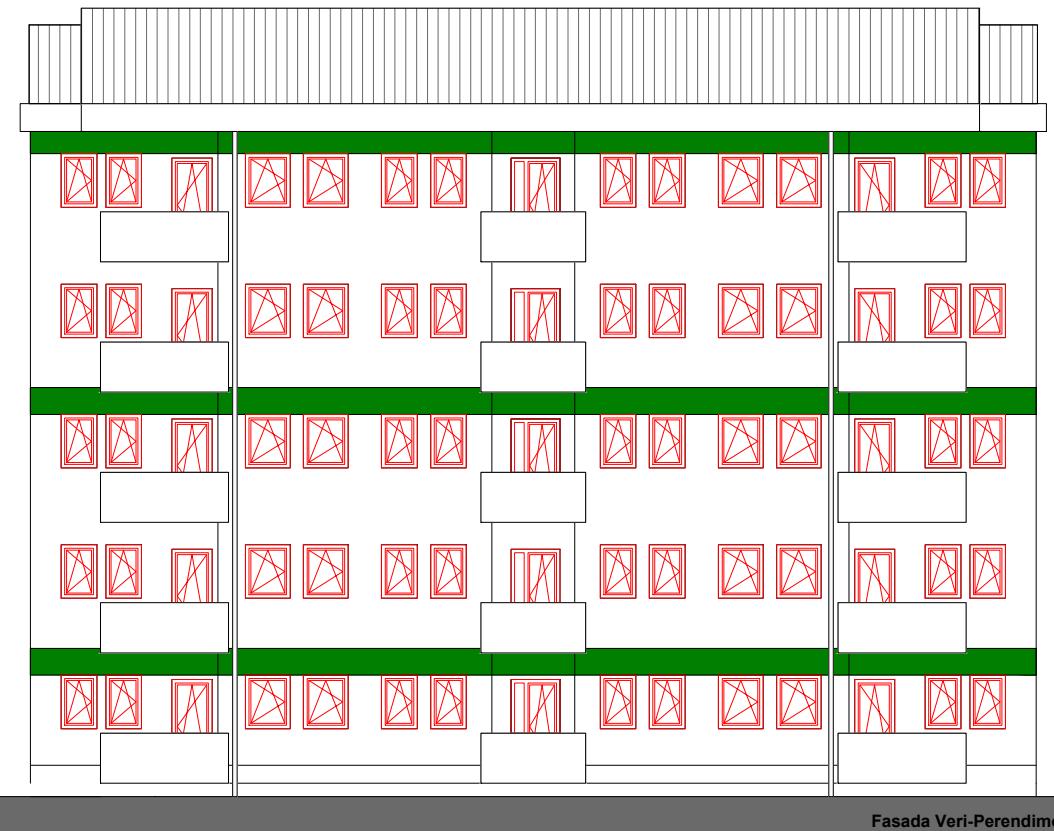

Përvizat e përkrahjeve

Termoizolimi i mureve me Lesh Guri $t=12\text{cm}$



Projekti:
Angazhimi i Kompanive pâr kryerie të punëve ndërtimore pâr implementimin e masave të Eficiencës se Energjisë në ndërtesat shumë banesore sociale

Nr. Prokurimi : VET-FKEE2020-24-1899-5-1-1C70 LOT 5
Kompania pune kyrese
ATC ALL TRADES OF CONSTRUCTION
ATC COM SHPK & DAITING SHPK
npatcom@gmail.com

Emri i ndërtuesit:
Ndertesa shume banesor Social I, Klinë

Faza e projektimit:
Arkitektura

Emri i vizatimit:
Mbrojtja ndaj zjarrit

Punuar nga:	Kontrolluar nga:
BSc Liridon Sejdiu	IDA. Njomza Hoti

Date:	08/2025	Rishikim:	
Shkalla e zgjedhimit:		Nr. i fases:	09
P=1:100			

Vërejtje: Masat mbrojtëse kundër zjarrit duhet të instalohen në têrë perimetrin e ndërtesës, si unazë me lesh guri dhe lartësi $h=60\text{cm}$ sipas paraqitjeve grafike

SKEMAT E DRITARET TË REJA

Pos_W-1	Pos_W-2	Pos_W-3	Pos_W-4
<p>Pozicioni: W-1, dim. 0.80x1.20m</p>	<p>Pozicioni: W-2, dim. 1.00x1.20m</p>	<p>Pozicioni: W-3, dim. 1.20x1.40m</p>	<p>Pozicioni: W-4, dim. 0.60x0.70m</p>
Sasia: 80	Sasia: 40	Sasia: 10	Sasia: 10

SKEMAT E DRITARET TË REJA

Pos_W-5	Pos_W-6	Pos_W-7	Pos_W-8
<p>Pozicioni: W-5, dim. 0.80x2.10m</p>	<p>Pozicioni: W-6, dim. 1.30x1.70m</p>	<p>Pozicioni: W-7, dim. 0.90x2.10m</p>	<p>Pozicioni: W-8, dim. 1.30x3.45m</p>
Sasia: 10	Sasia: 1	Sasia: 15	Sasia: 1

SKEMAT E DYERVE TË JASHTME

Pos_W-9	Pos_D-2	Pos_D-1
<p>Pozicioni: W-9, dim. 1.30x2.20m</p>	<p>Pozicioni: D-2, dim. 1.00x2.10m</p>	<p>Pozicioni: D-1, dim. 2.20x2.20m</p>
Sasia: 2	Sasia: 25	Sasia: 1



Projekti:
Angazhimi i Kompanive për kryerje të punave ndërtimore për implementimin e masave të Eficiencës se Energjisë në ndërtesa shumë banesore sociale

Nr. Prokurimi: VET-FKEE2020-24-1699-5-1-I/C70 LOT 5
Kompania punëkryese
ATC ALL TYPES OF CONSTRUCTION
ATC COM SHPK & DAJTING SHPK
npatcom@gmail.com

Emri i ndertesës:
Ndertesa shume banesor Social I, Klinë

Faza e projektit:
Arkitektura

Emri i vizitimit:
Skema e dyerve dhe dritarëve

Puruar nga:	Kontrolluar nga:
BSc Liridon Sejdiu	IDA. Njomza Hoti
Date:	Rishikim:
08/2025	01
Shkalla e zvogëlimit:	Nr. i faqes:
P= 1:50	10