
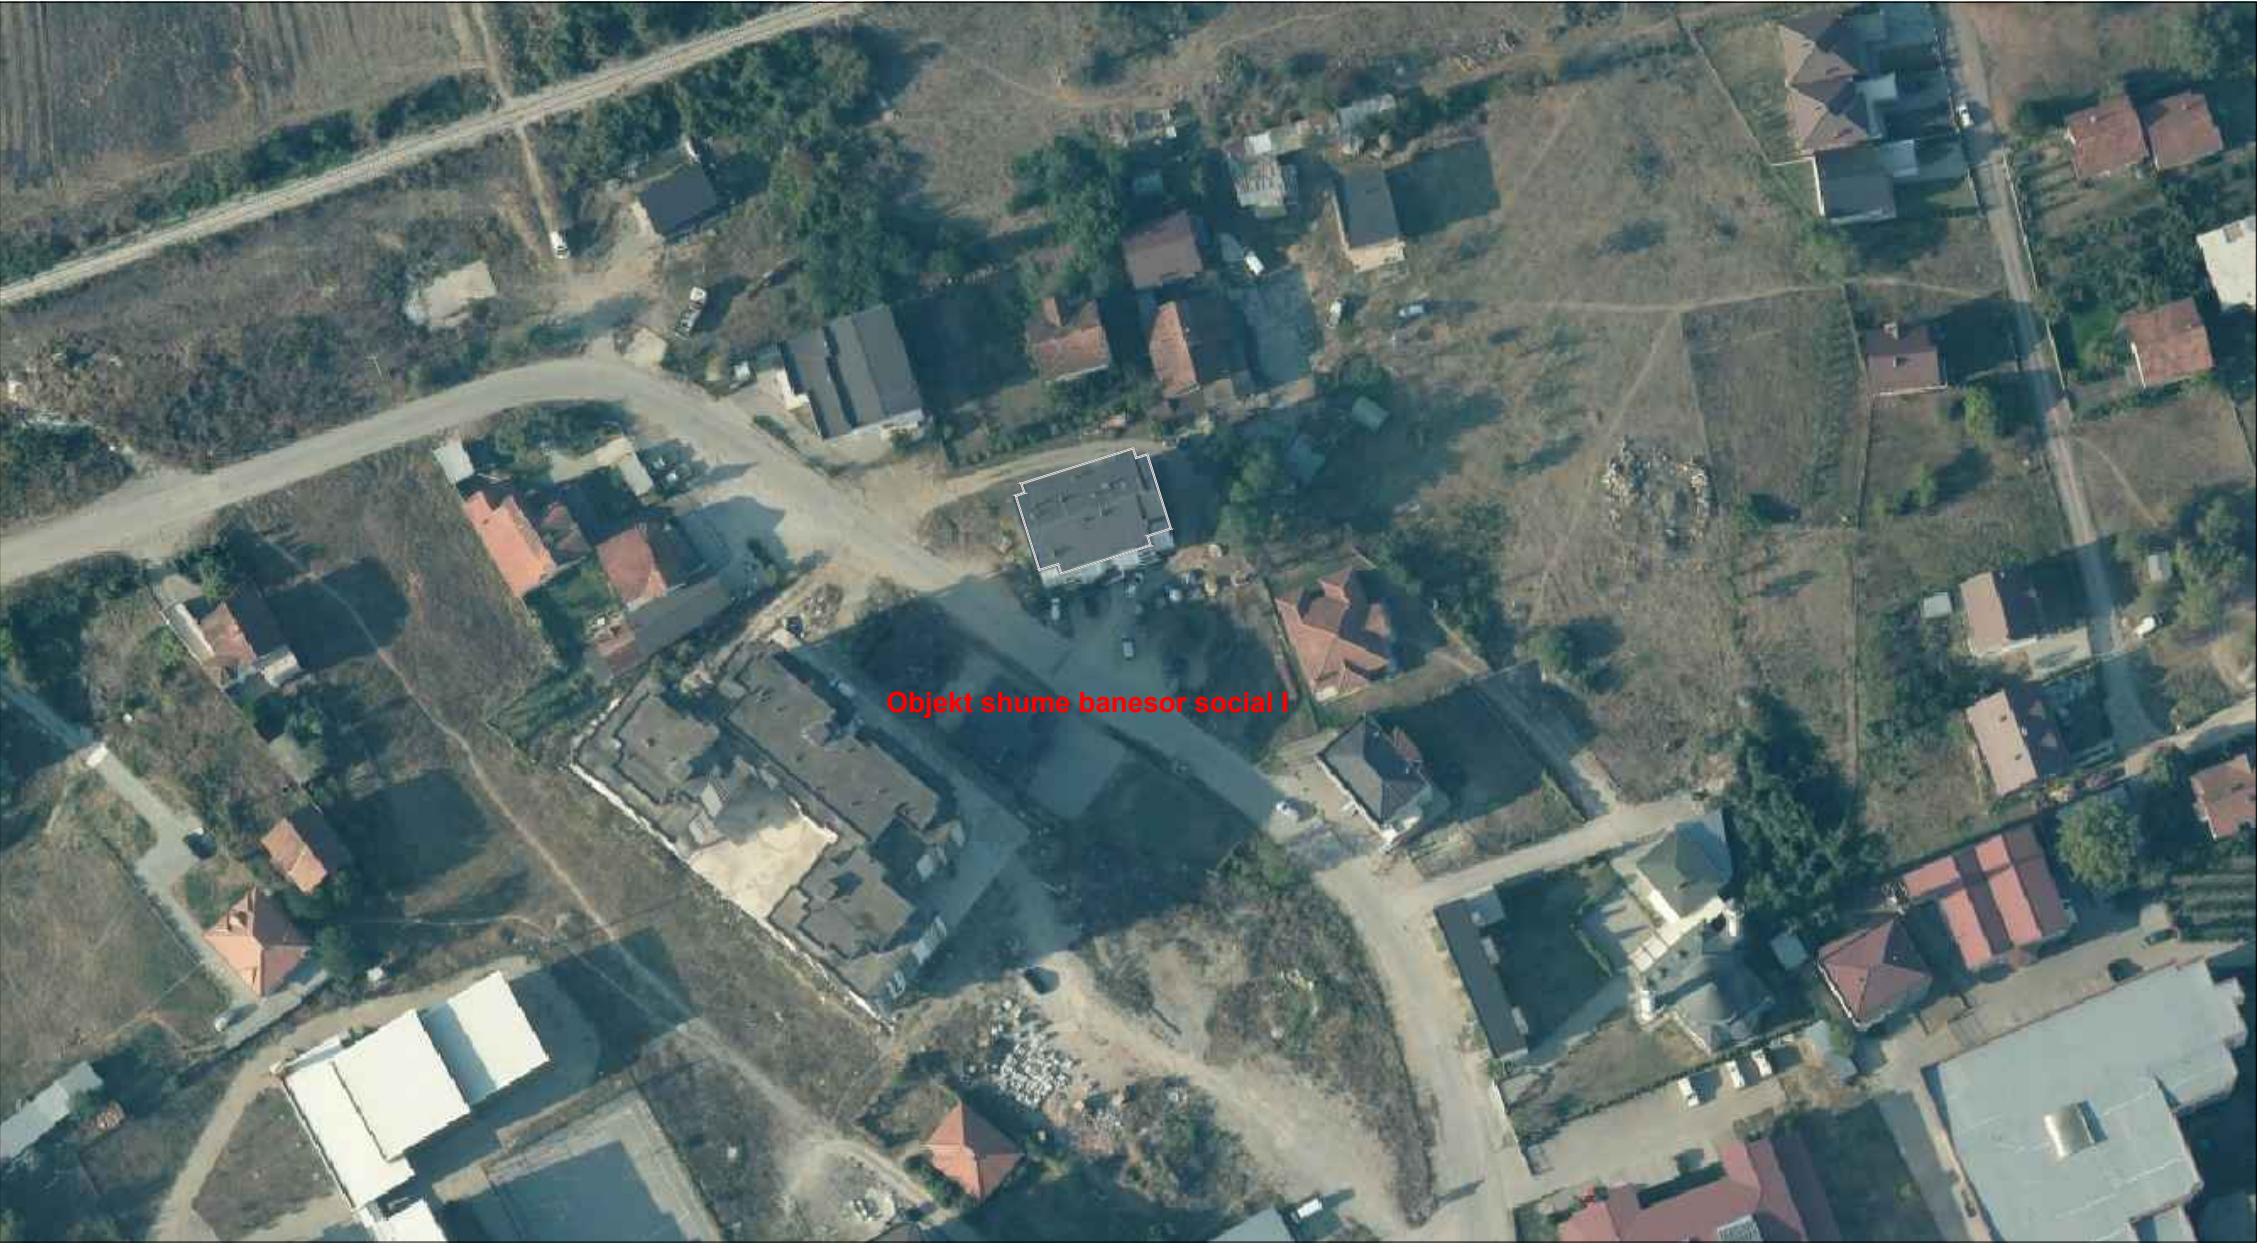


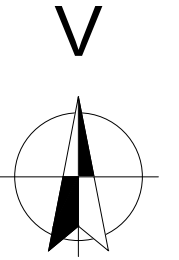

REPUBLIKA E KOSOVËS / REPUBLIC OF KOSOVO
Fondi i Kosovës për Eficiencë të Energjisë
Kosovo Energy Efficiency Fund

Angazhimi i Kompanive për kryerje të punëve ndërtimore për
implementimin e masave të Eficiencës së Energjisë në ndërtesat
shumë banesore sociale

Nr. Prokurimit : VET-FKEE2020-24-1699-5-1-1/C70 Lot 5

Kompania punekryese



ATC COM SHPK & DAITING SHPK
nnpatccom@gmail.com

Emri i ndërtesës:

**Ndertesha shume banesor Social I,
Klinë**

Faza e projektimit:

Arkitektura

Emri i vizatimit:

Lokacioni i ndërtesës

Punuar nga:

BSc Liridon Sejdiu

Kontrolluar nga:

IDA. Njomza Hoti

Data:

08/2025



Rishikim:

Shkalla e zvogëlimit:

P=1:100

Nr. i faqes:



01

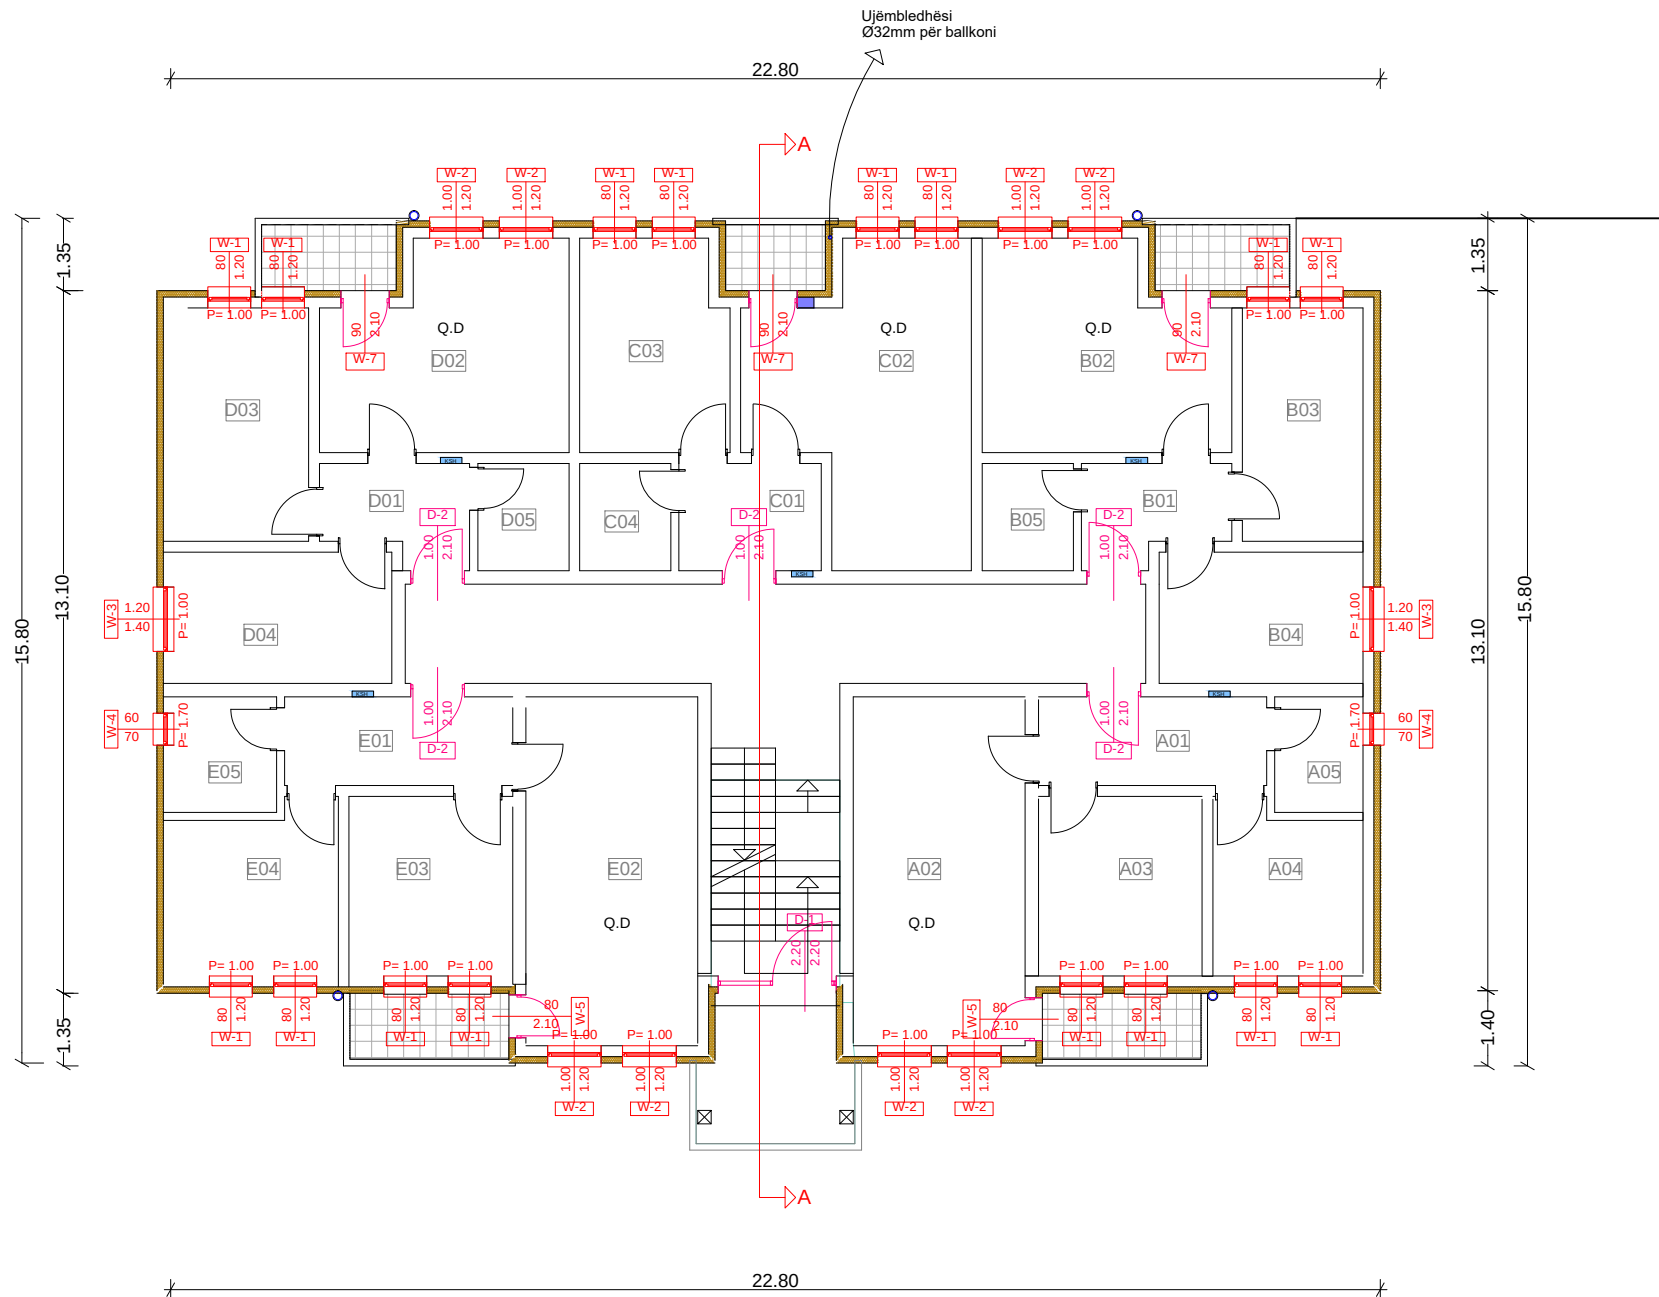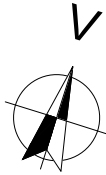

Përshkrimi renovimit

- Termoizolimi i mureve me EPS t=12cm
- Ndërrimi i dritareve
- Ndërrimi i detyrë
- Muratim



 REPUBLIKA E KOSOVËS / REPUBLIC OF KOSOVO Fondi i Kosovës për Eficiencë të Energjisë Kosovo Energy Efficiency Fund	
Projekti: Angazhimi i Kompanive për kryerje të punëve ndërtimore për implementimin e masave të Eficiencës së Energjisë në ndërtesat shumë banesore sociale	
Nr. Prokurimit : VET-FKEE2020-24-1699-S-1-UC70 LOT 5 Kompania punëkryese  ALL TYPES OF CONSTRUCTION CO. LTD. ATC COM SHPK & DATING SHPK nnpattcom@gmail.com	
Emri i ndërtesës: Ndertesa shume banesor Social I, Klinë	
Faza e projektimit: Arkitektura	
Emri i vizatimit: Përdhesa	
Punuar nga: BSc Liridon Sejdiu	Kontrolluar nga: IDA. Njoma Hoti
Date: 08/2025	Rishikim:
Shkalla e zvogëlimit: P=1:100	Nr. i faqes: 02

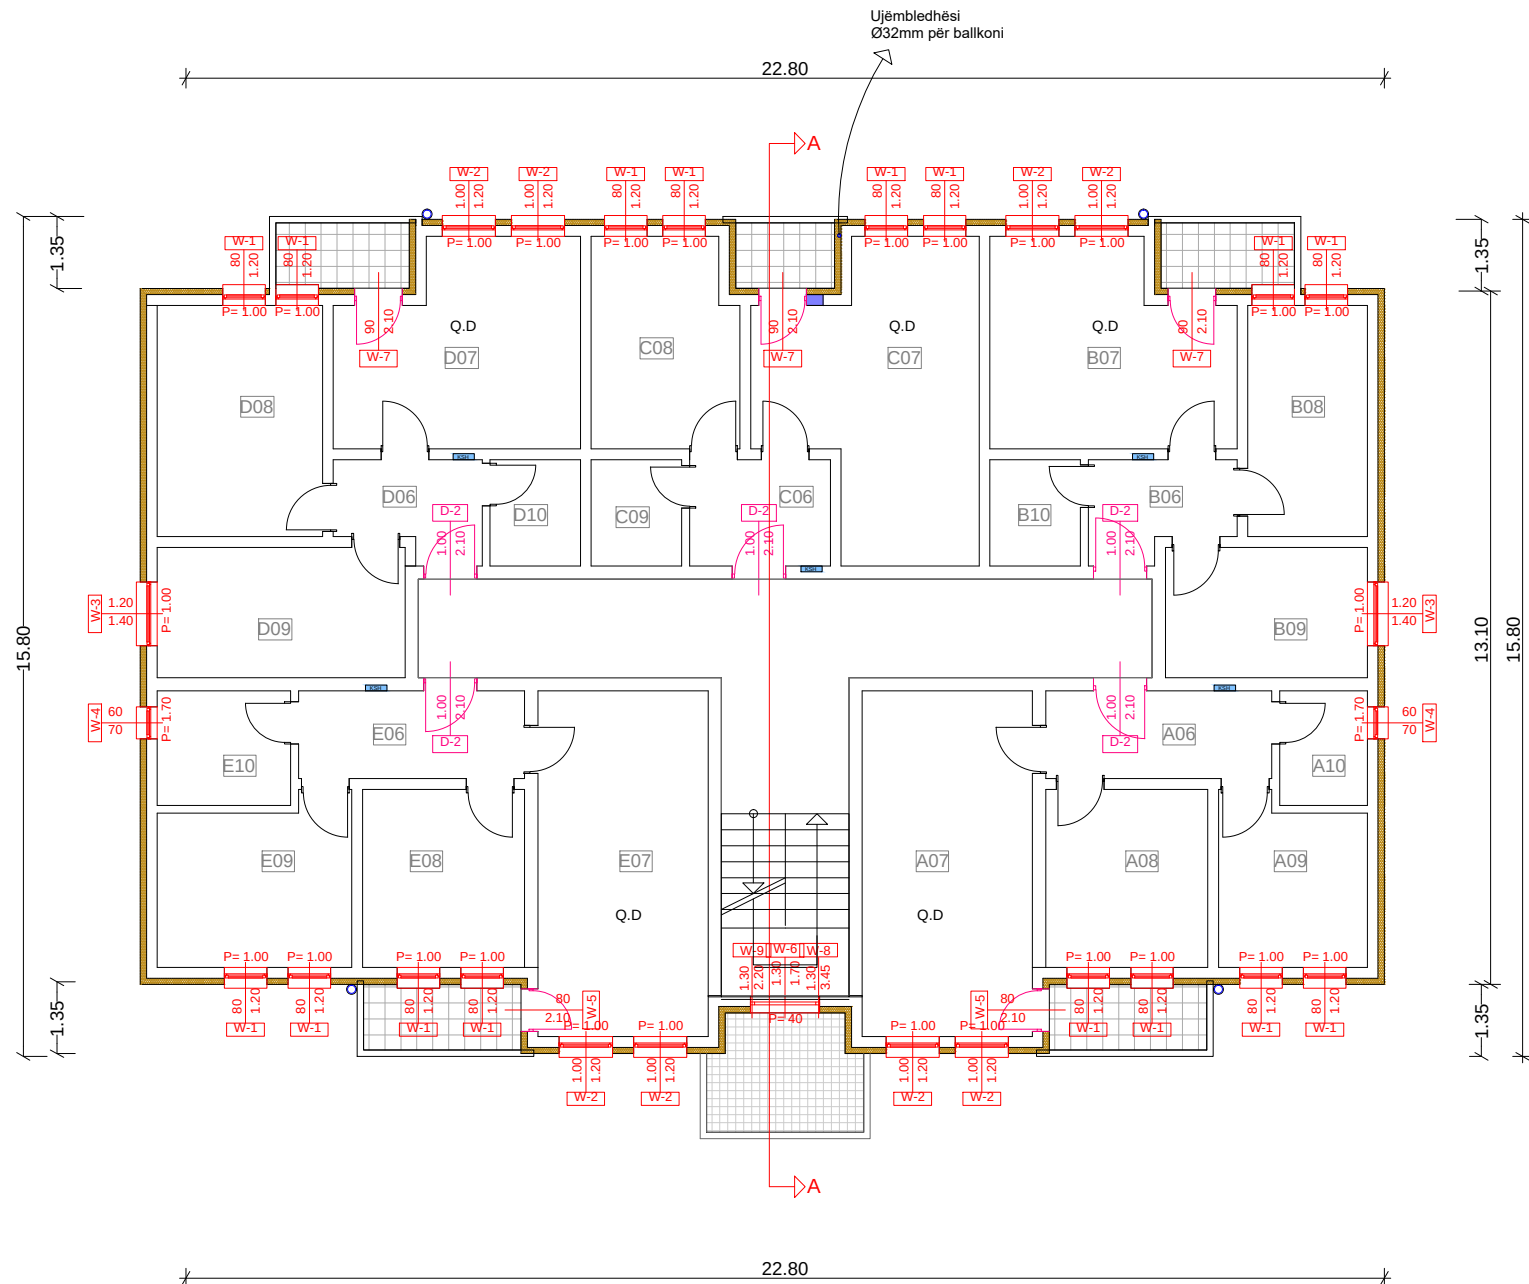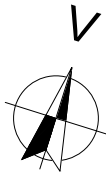

Përshkrimi renovimit

- Termoizolimi i mureve me EPS t=12cm
- Ndërrimi i dritareve
- Ndërrimi i dyerve
- Renovimi i strehes te hryja
- Mur i ri



 REPUBLIKA E KOSOVËS / REPUBLIC OF KOSOVO Fondi i Kosovës për Eficiencë të Energjisë Kosovo Energy Efficiency Fund	
Projekti: Angazhimi i Kompanive për kryerje të punëve ndërtimore për implementimin e masave të Eficiencës së Energjisë në ndërtesat shumë banesore sociale	
Nr. Prokurimit : VET-FKEE2020-24-1699-S-1-UC70 LOT 5 Kompania punëkryese  ATC COM SHPK & DAJTING SHPK nnpstccom@gmail.com	
Emri i ndërtesës: Ndertesa shume banesor Social I, Klinë	
Faza e projektimit: Arkitektura	
Emri i vizatimit: Kati I - IV	
Punuar nga: BSc Liridon Sejdiu	Kontrolluar nga: IDA. Njomza Hoti
Date: 08/2025	Rishikim:
Shkalla e zvogëlimit: P=1:100	Nr. i faqes: 03

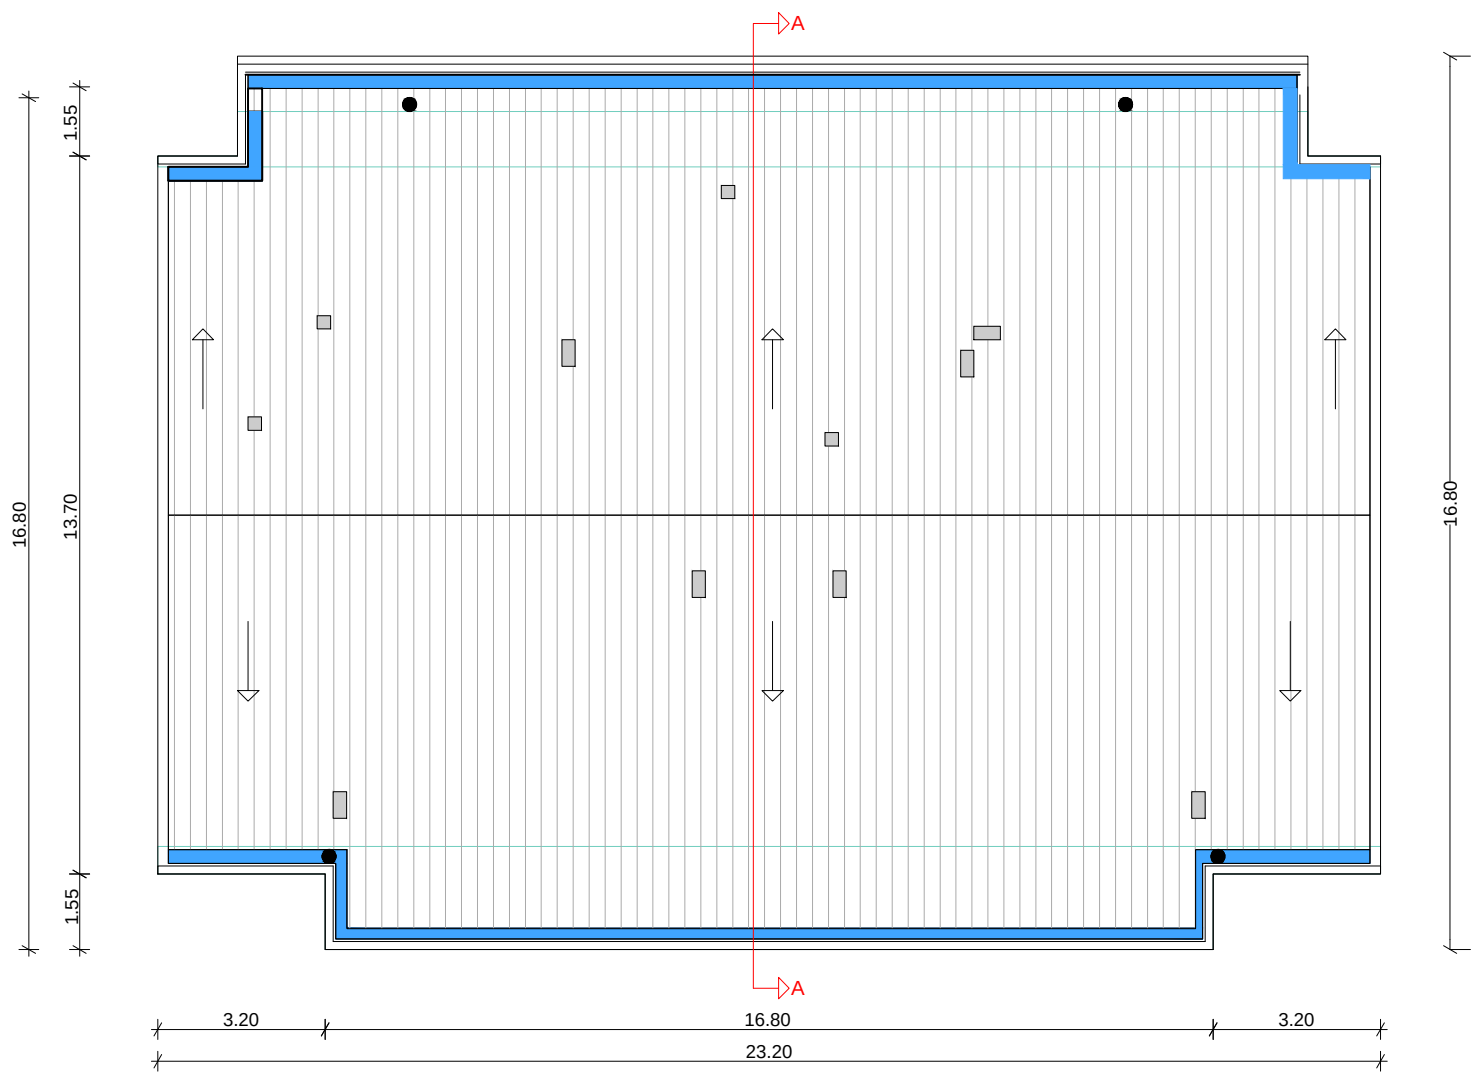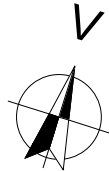

Përshkrimi renovimit

-  Ndërrimi i mbulesës dhe termoizolimi i kulmit me EPS t=16cm
-  Ndërrimi i ulluqeve horizontale
-  Ndërrimi i ulluqeve vertikale

 REPUBLIKA E KOSOVËS / REPUBLIC OF KOSOVO Fondi i Kosovës për Eficiencë të Energjisë Kosovo Energy Efficiency Fund	
Projekti: Angazhimi i Kompanive për kryerje të punëve ndërtimore për implementimin e masave të Eficiencës së Energjisë në ndërtesat shumë banesore sociale	
Nr. Prokurimit : VET-FKEE2020-24-1699-S-1-UC70 LOT 5 Kompania punëkryese  ATC COM SHPK & DAJTING SHPK nnpstccom@gmail.com	
Emri i ndërtesës: Ndertesa shume banesor Social I, Klinë	
Faza e projektimit: Arkitektura	
Emri i vizatimit: Kulmi	
Punuar nga: BSc Liridon Sejdiu	Kontrolluar nga: IDA. Njomza Hoti
Date: 08/2025	Rishikim:
Shkalla e zvogëlimit: P=1:100	Nr. i faqes: 04

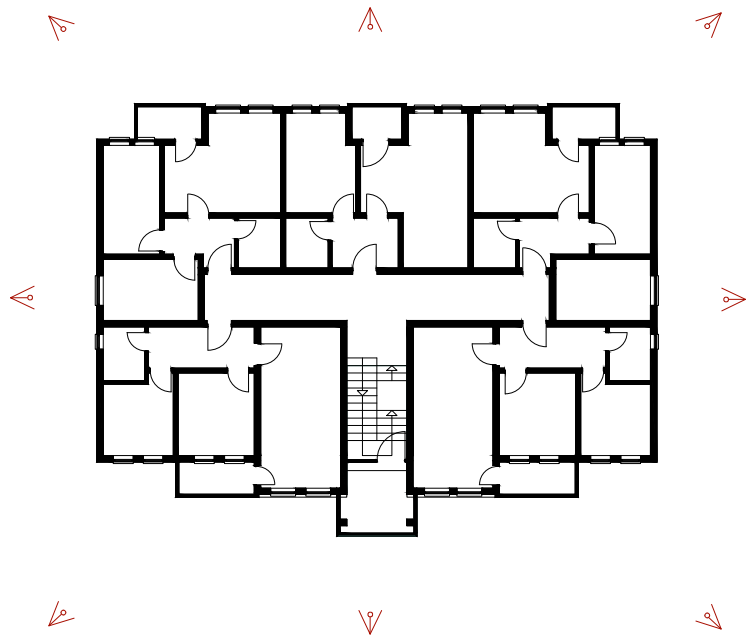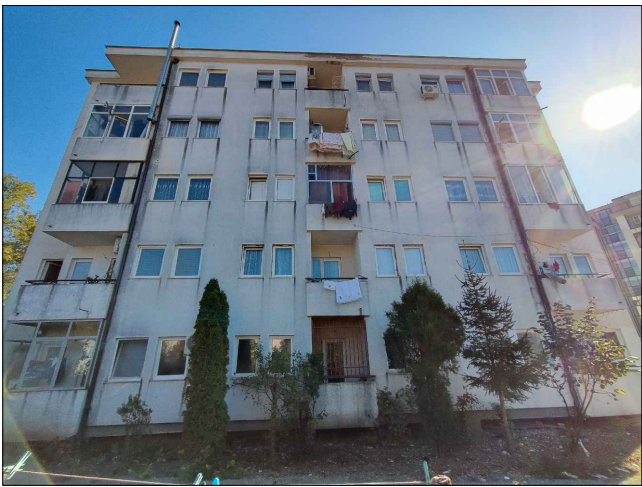



REPUBLICA E KOSOVËS / REPUBLIC OF KOSOVO
Fondi i Kosovës për Eficiencë të Energjisë
Kosovo Energy Efficiency Fund

Projekti:

Angazhimi i Kompanive për kryerje të punëve ndërtimore për implementimin e masave të Eficiencës së Energjisë në ndërtesat shumë banesore sociale

Nr. Prokurimit : VET-FKEE2020-24-1699-5-1-1/C70 LOT 5



Kompania punekryese

ATC COM SHPK & DAJTING SHPK
nnpatccom@gmail.com

Emri i ndërtesës:

**Ndertesa shume banesor Social I,
Klinë**


Faza e projektimit:


Arkitektura

Emri i vizatimit:

Fotot e ndërtesës

Punuar nga: BSc Liridon Sejdiu	Kontrolluar nga: IDA. Njomza Hoti
Datë: 08/2025	Rishikim:
Shkalla e zvogëlimit: P=1:100	Nr. i faqes: 05

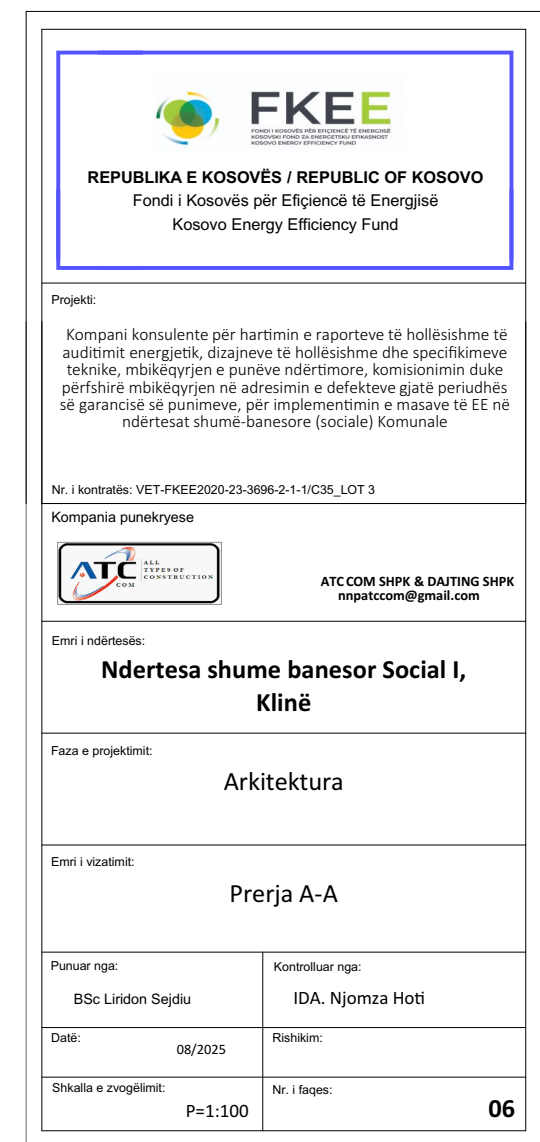

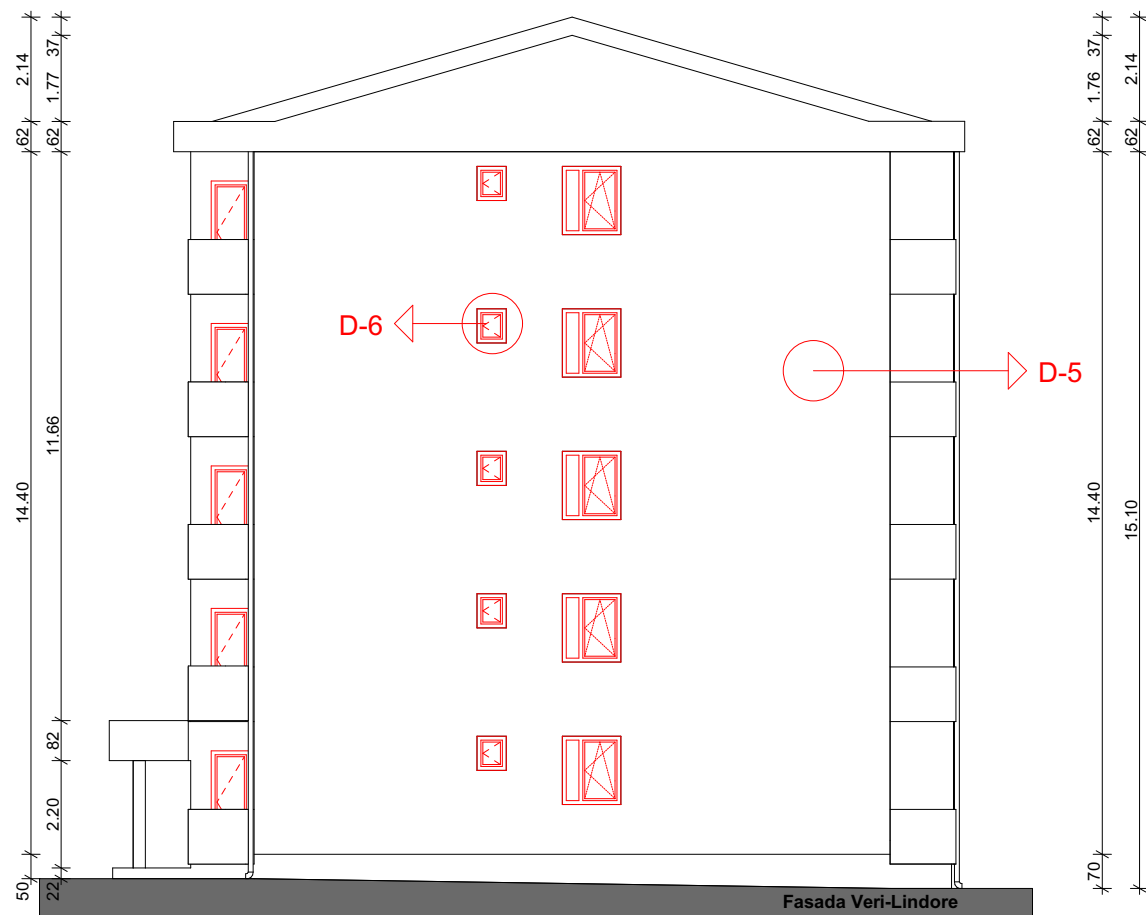

Përshkrimi i renovimit

- Ndërimi i dritareve
- Ndërimi i dyerve

**FKEE**
FOND I KOSOVËS PËR EFICIENCË TË ENERGJISË

REPUBLIKA E KOSOVËS / REPUBLIC OF KOSOVO
Fondi i Kosovës për Eficienë të Energjisë
Kosovo Energy Efficiency Fund

Projekti:
Kompani konsulente për hartimin e raporteve të hollësishme të auditimit energjetik, dizajneve të hollësishme dhe specifikimeve teknike, mbikëqyrjen e punëve ndërtimore, komisionimin duke përfshirë mbikëqyrjen në adresimin e defekteve gjatë periudhës së garancisë së punimeve, për implementimin e masave të EE në ndërtesat shumë-banësore (sociale) Komunale

Nr. i kontratës: VET-FKEE2020-23-3896-2-1-1/C35_LOT 3

**ATC**
ATC CONSULTING

ATCCOM SHPK & DAITING SHPK
mpatcom@gmail.com

Emri i ndërtesës:
Ndertesa shume banesor Social I, Klinë

Faza e projektimit:
Arkitektura

Emri i vizatimit:
Fasada Veriore & Lindore

Punuar nga:
BSc Liridon Sejdiu

Kontrolluar nga:
IDA. Njomza Hoti



Data:
08/2025

Rishikim:

Shkalla e zvogëlimit:
P=1:100

Nr. i faqes:
07




520x420mm

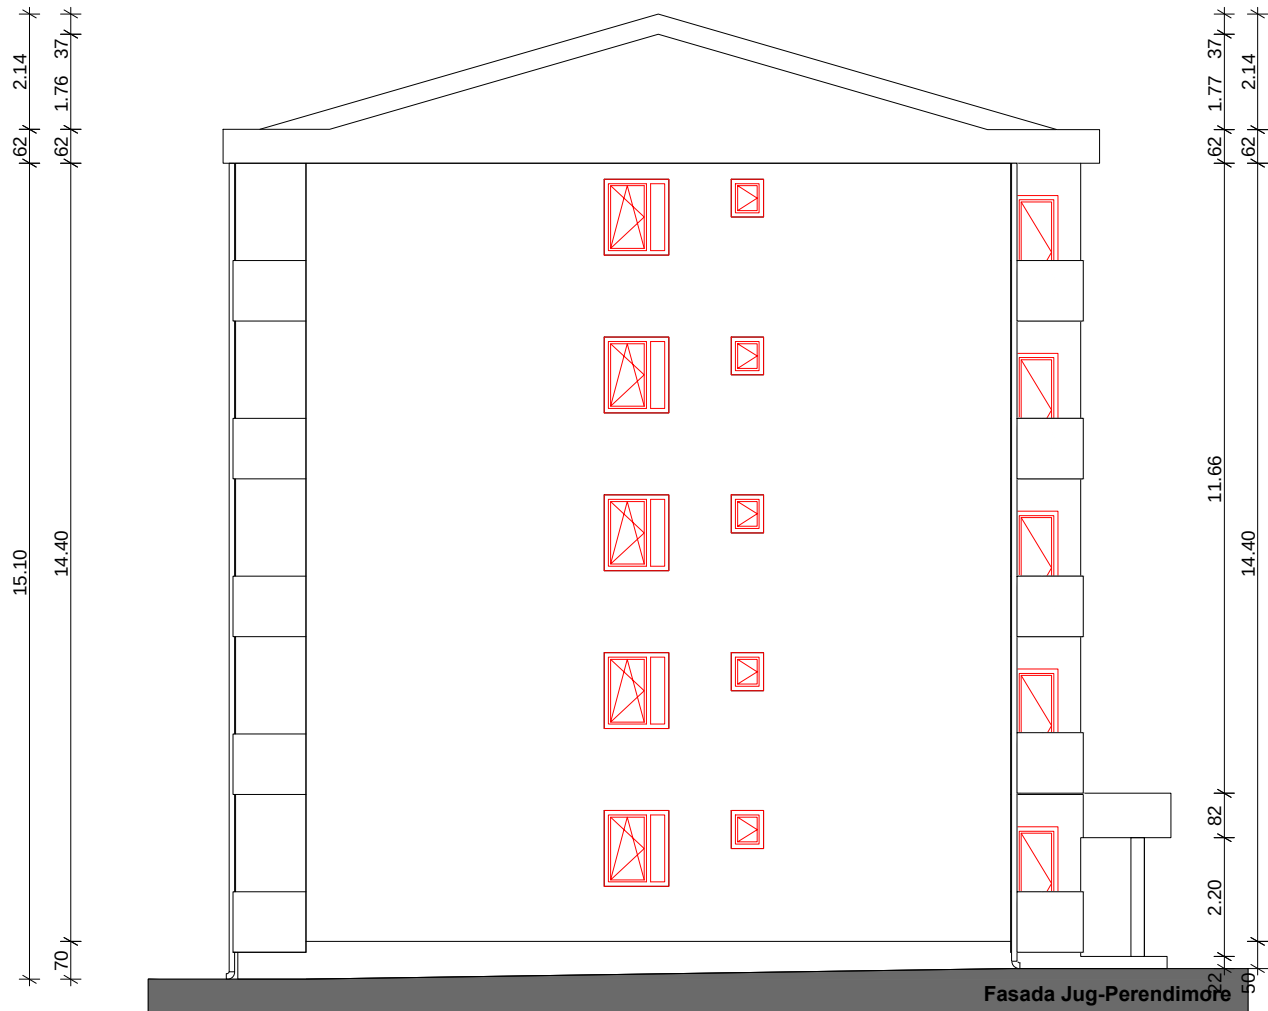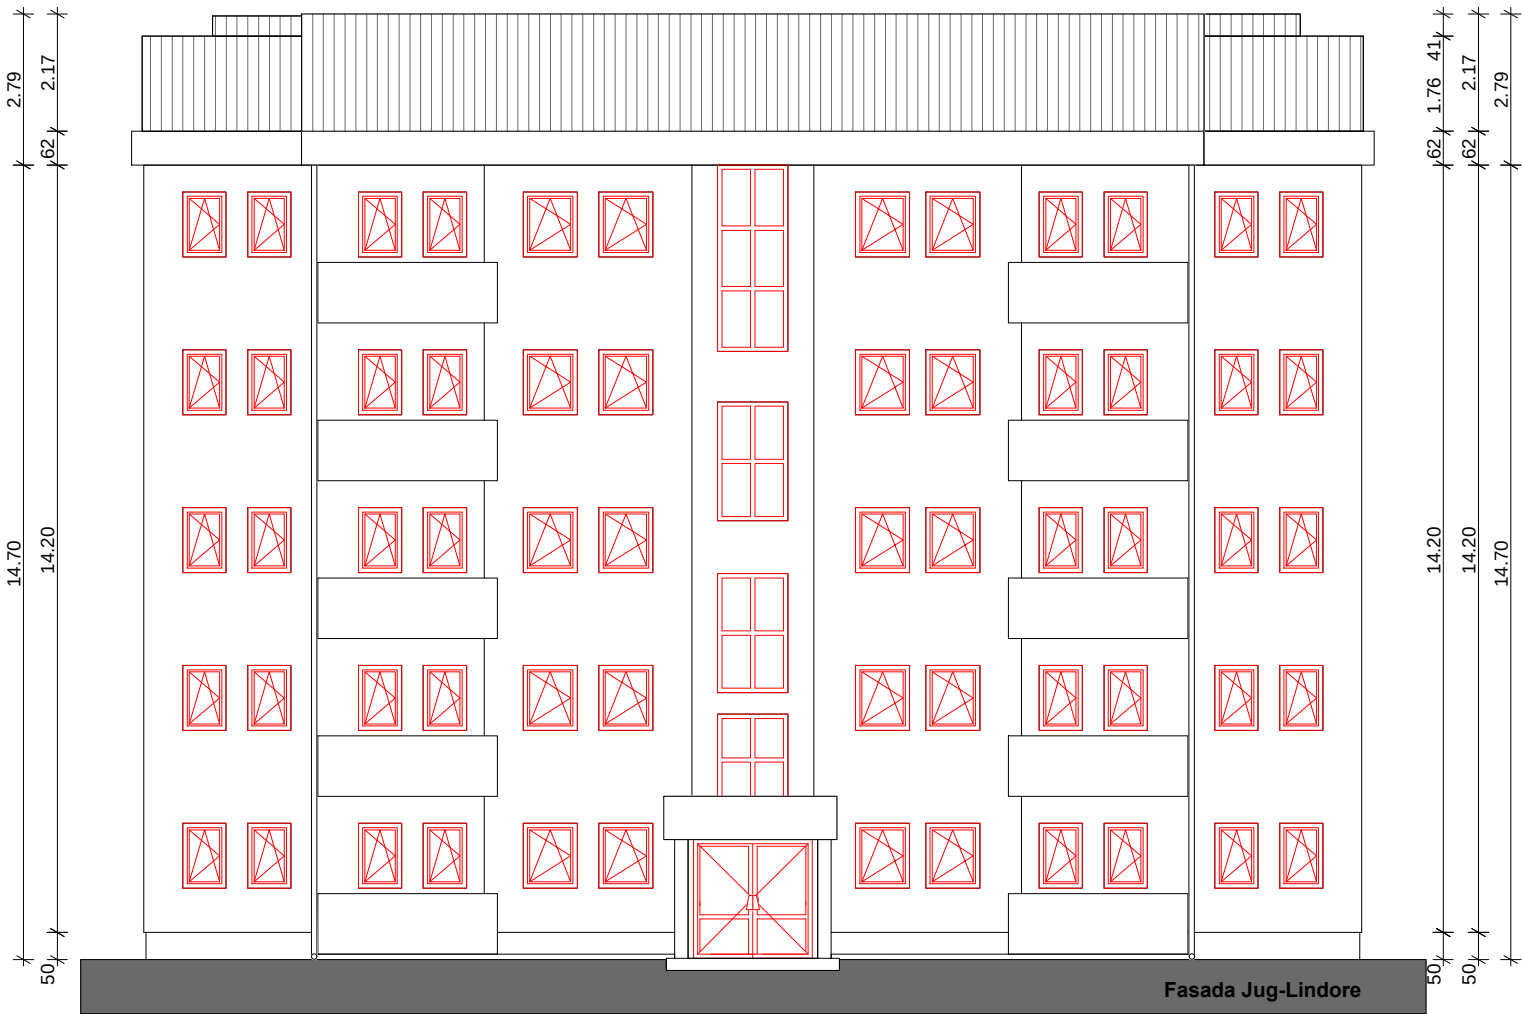

Përshkrimi i renovimit

- Ndërrimi i dritareve
- Ndërrimi i dyerve

 REPUBLIKA E KOSOVËS / REPUBLIC OF KOSOVO Fondi i Kosovës për Eficiencë të Energjisë Kosovo Energy Efficiency Fund	
Projekti: Angazhimi i Kompanive për kryerje të punëve ndërtimore për implementimin e masave të Eficiencës së Energjisë në ndërtësat shumë banesore sociale	
Nr. Prokurimit : VET-FKEE2020-24-1699-S-1-1/C70 LOT 5 Kompania punekryese  ATC COM SHPK & DAIJING SHPK nnpatcom@gmail.com	
Emri i ndërtësës: Ndertesa shume banesor Social I, Klinë	
Faza e projektimit: Arkitektura	
Emri i vizatimit: Fasada Jugore & Perendimore	
Punuar nga: BSc Liridon Sejdiu	Kontrolluar nga: IDA. Njomza Hoti
Date: 08/2025	Rishikim:
Shkalla e zvogëlimit: P=1:100	Nr. i faqes: 08

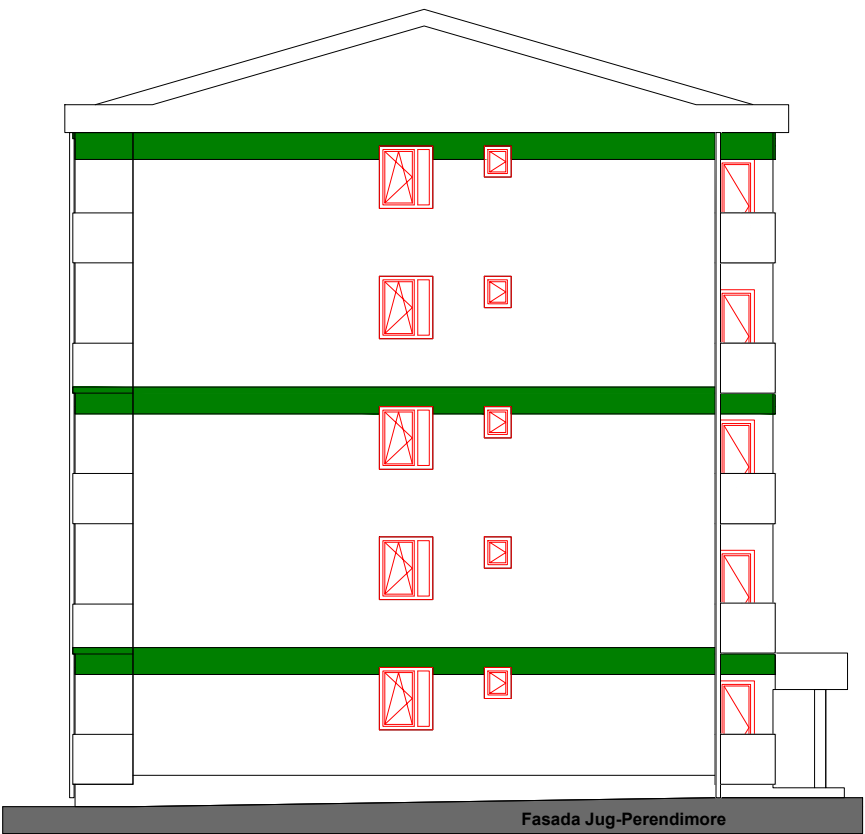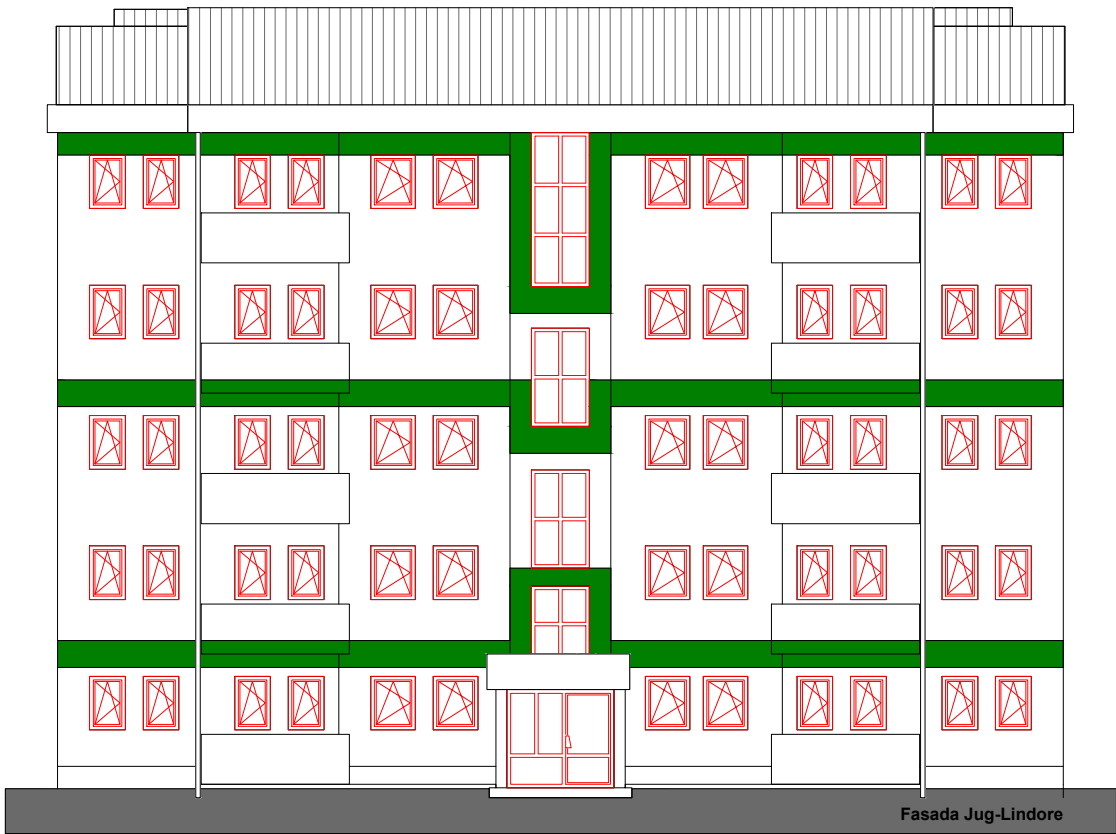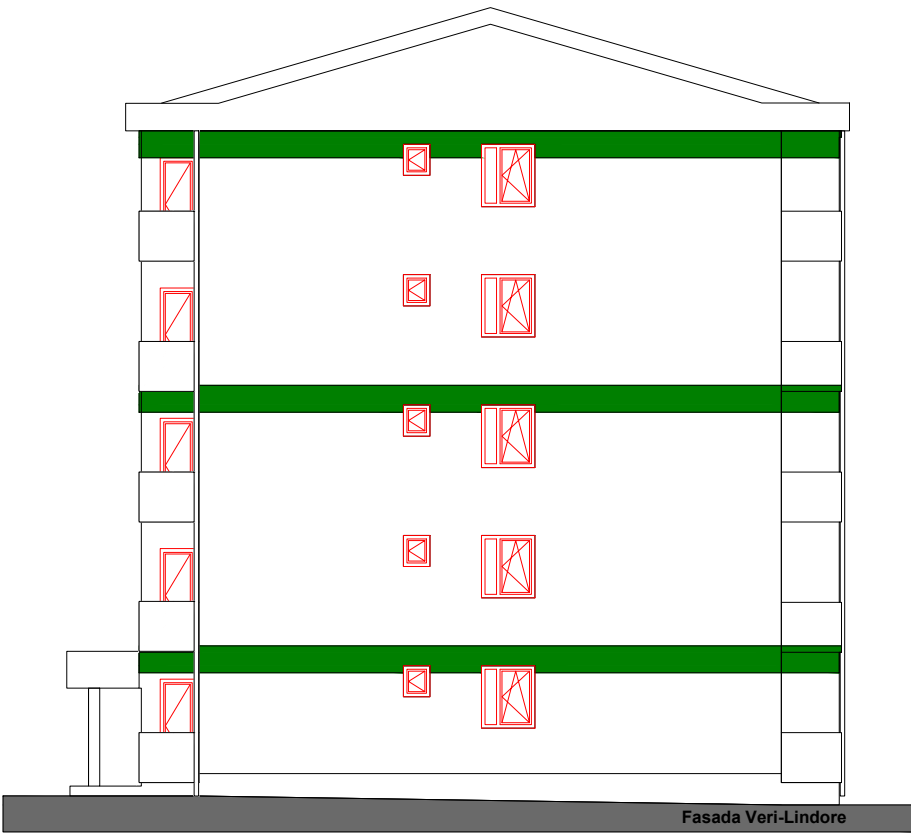

Vërejtje: Masat mbrojtëse kundër zjarrit duhet të instalohen në tërë perimetrin e ndërtesës, si unazë me lesh guri dhe lartësi h=60cm sipas paraqitjeve grafike

Përshkrimi renovimit

Termoizolimi i mureve me Lesh Guri t=12cm

 REPUBLIKA E KOSOVËS / REPUBLIC OF KOSOVO Fondi i Kosovës për Eficiencë të Energjisë Kosovo Energy Efficiency Fund	
Projekt: Angazhimi i Kompanive për kryerje të punëve ndërtimore për implementimin e masave të Eficiencës së Energjisë në ndërtesat shumë banesore sociale	
Nr. Prokurimit : VET-FKEE2020-24-1699-S-1-1/C70 LOT 5 Kompania punëkryese  ATC ALL EYES OF CONSTRUCTION ATC COM SHPK & DAIJING SHPK nnpatcom@gmail.com	
Emri i ndërtesës: Ndertesa shume banesor Social I, Klinë	
Faza e projektimit: Arkitektura	
Emri i vizatimit: Mbrojtja ndaj zjarrit	
Punuar nga: BSc Liridon Sejdiu	Kontrolluar nga: IDA. Njomza Hoti
Date: 08/2025	Rishikim:
Shkalla e zvogëlimit: P=1:100	Nr. i faqes: 09

SKEMAT E DRITARET TË REJA							
Pos_W-1		Pos_W-2		Pos_W-3		Pos_W-4	
Pozicioni: W-1, dim. 0.80x1.20m	Sasia: 80	Pozicioni: W-2, dim. 1.00x1.20m	Sasia: 40	Pozicioni: W-3, dim. 1.20x1.40m	Sasia: 10	Pozicioni: W-4, dim. 0.60x0.70m	Sasia: 10
SKEMAT E DRITARET TË REJA							
Pos_W-5		Pos_W-6		Pos_W-7		Pos_W-8	
Pozicioni: W-5, dim. 0.80x2.10m	Sasia: 10	Pozicioni: W-6, dim. 1.30x1.70m	Sasia: 1	Pozicioni: W-7, dim. 0.90x2.10m	Sasia: 15	Pozicioni: W-8, dim. 1.30x3.45m	Sasia: 1
SKEMAT E DRITARET TË REJA		SKEMAT E DYERVE TË JASHTME					
Pos_W-9		Pos_D-2		Pos_D-1			
Pozicioni: W-9, dim. 1.30x2.20m	Sasia: 2	Pozicioni: D-2, dim. 1.00x2.10m	Sasia: 25	Pozicioni: D-1, dim. 2.20x2.20m	Sasia: 1		



REPUBLIKA E KOSOVËS / REPUBLIC OF KOSOVO
Fondi i Kosovës për Eficiencë të Energjisë
Kosovo Energy Efficiency Fund

Projekti:

Angazhimi i Kompanive për kryerje të punëve ndërtimore për implementimin e masave të Eficiencës së Energjisë në ndërtesat shumë banesore sociale

Nr. Prokurimi: VET-FKEE2020-24-1699-S-1-1/C70 LOT 5

Kompania punëkryese



ATC COM SHPK & DAIJING SHPK
nnpaticom@gmail.com

Emri i ndërtësit:

Ndertesa shume banesor Social I, Klinë

Faza e projektimit:

Arkitektura

Emri i vizatimit:

Skema e dyerve dhe dritarëve

Punuar nga:	Kontrolluar nga:
BSc Liridon Sejdlu	IDA. Njomza Hoti
Data:	Rishikim:
08/2025	01
Shkalla e zvogëlimit:	Nr. i faqes:
P= 1:50	10