
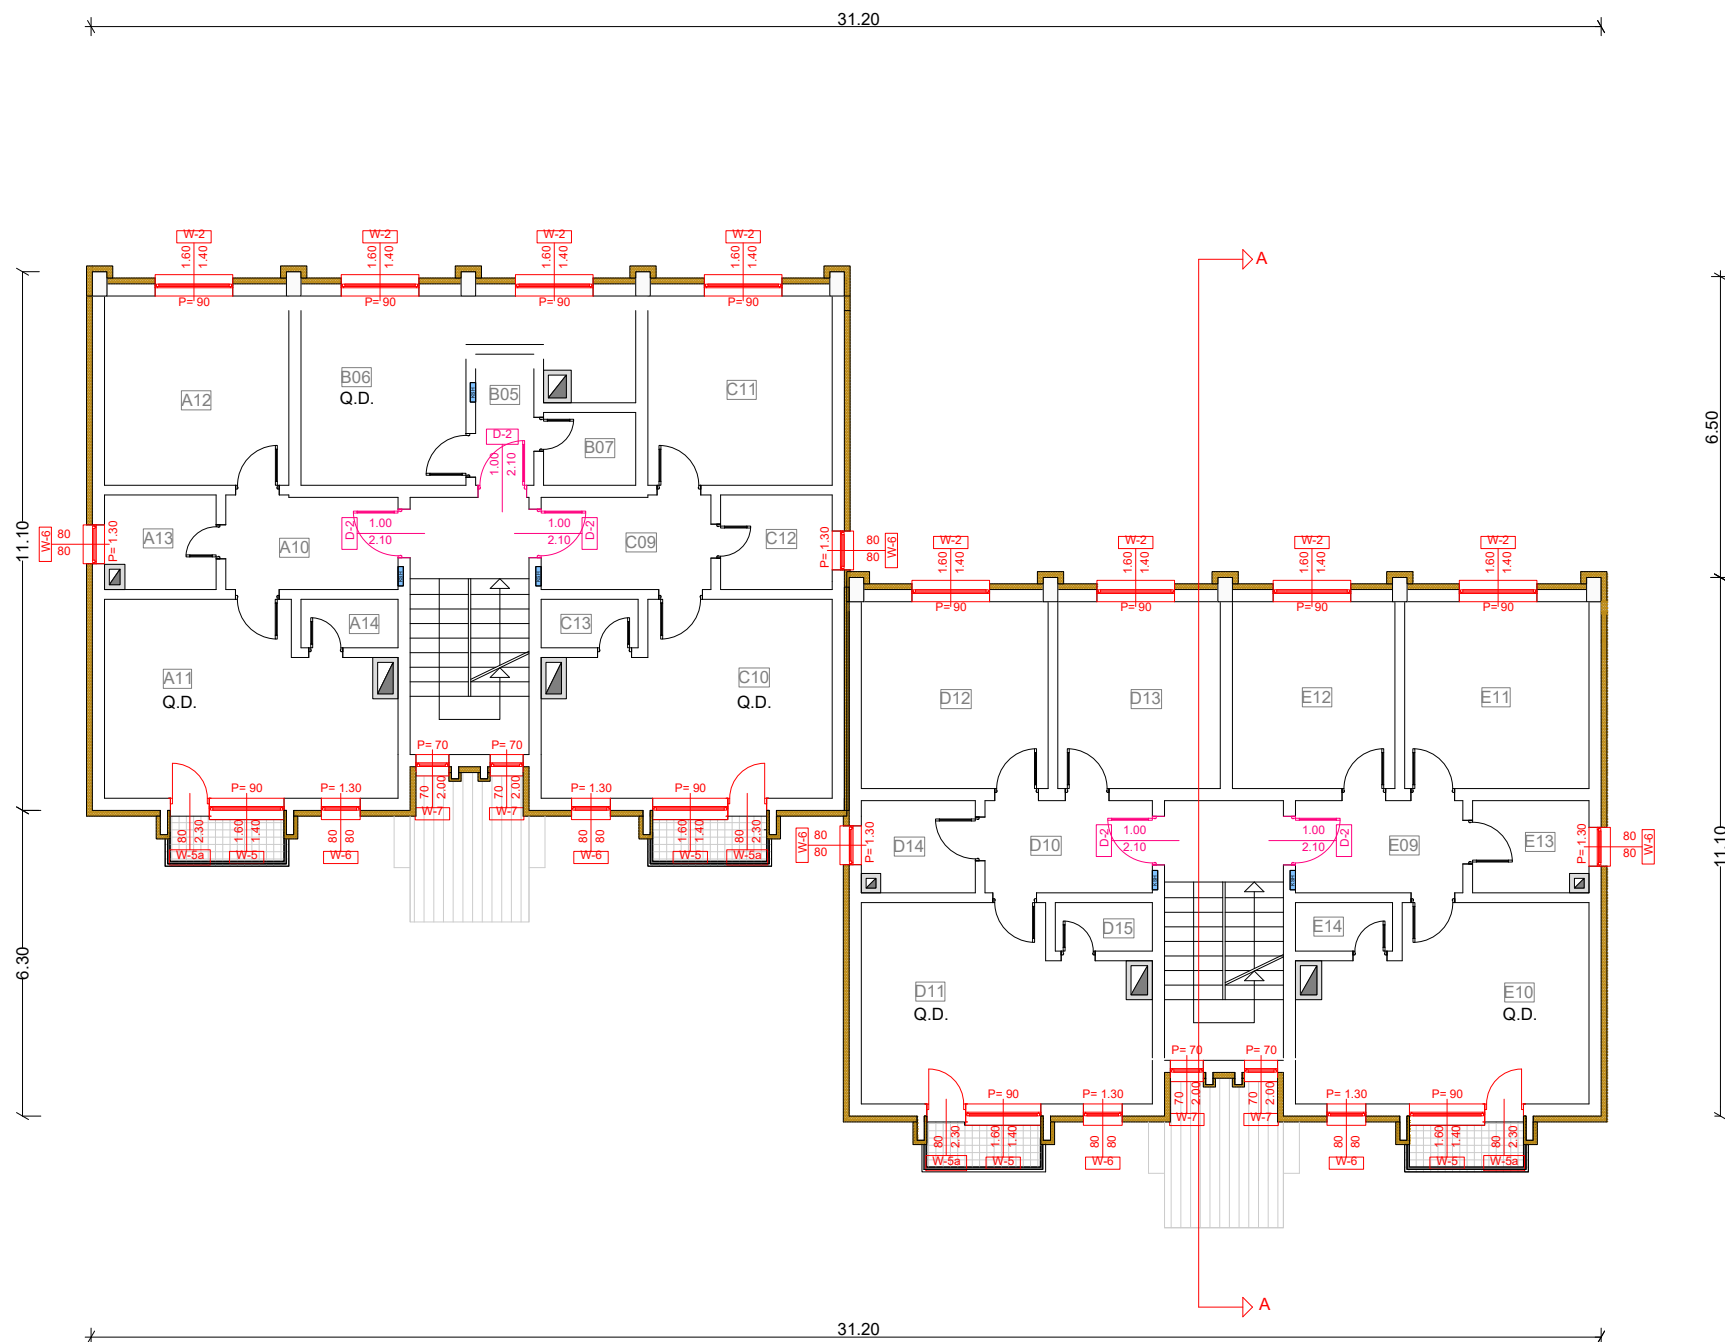


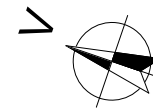

Përshkrimi i renovimit

- Termoizolimi i mureve me EPS t=12cm
- Ndërrimi i dritareve
- Ndërrimi i derve
- Renovimi i ballkoneve

 REPUBLIKA E KOSOVËS / REPUBLIC OF KOSOVO Fondi i Kosovës për Eficiencë të Energjisë Kosovo Energy Efficiency Fund	
Projekti: Angazhimi i Kompanive për kryerje të punëve ndërtimore për implementimin e masave të Eficiencës së Energjisë në ndërtësat shumë banesore sociale	
Nr. i kontratës: VET-FKEE2020-23-3896-2-1-1/C35_Lot 5	
Kompania punëkyese:  ATC COM SHPK & DATING SHPK mngatccom@gmail.com	
Emri i ndërtësatit: Ndërtësa shumë banesore sociale III, Klinë - Lot 5	
Faza e projektimit: Arkitektura	
Emri i vizatimit: Kati II-IV	
Punuar nga: BSc Liridon Sejdiu	Kontrolluar nga: IDA. Njomza Hoti
Data: 08/2025	Rishikim:
Shkalla e zvogëlimit: P=1:100	Nr. i faqes: 04