
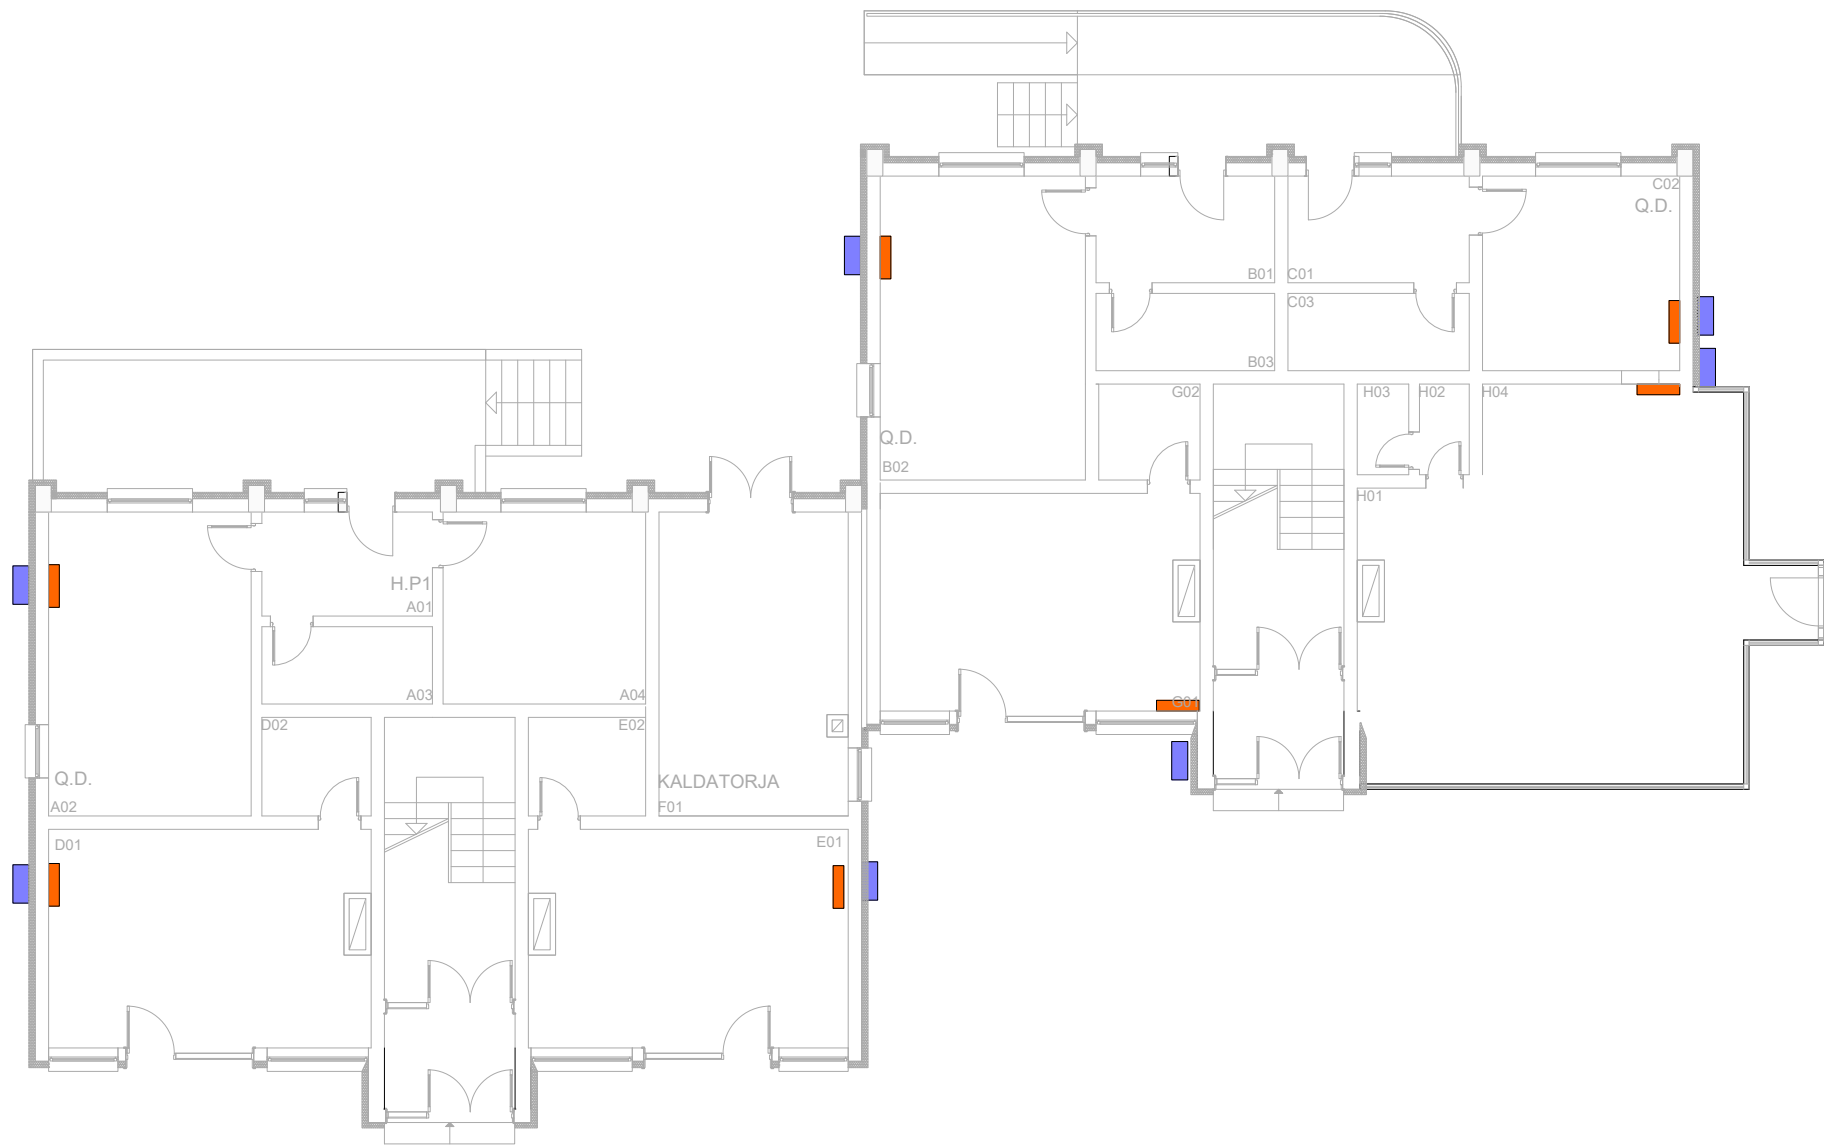


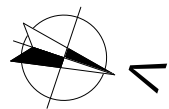

 REPUBLIKA E KOSOVËS / REPUBLIC OF KOSOVO Fondi i Kosovës për Eficiencë të Energjisë Kosovo Energy Efficiency Fund	
Projekti: Angazhimi i Kompanive për kryerje të punëve ndërtimore për implementimin e masave të Eficiencës së Energjisë në ndërtesat shumë-banesore sociale	
Nr.Prokurimit:VET-FKEE2020-24-1699-5-1-1/C70	
Kompania pun kryese:  ATC COM SHPK & DAJTING SHPK nnpatcom@gmail.com	
Emri i ndërtesës: Ndërtesa shumë-banesore sociale II_15, Klinë - Lot 5	
Faza e projektimit: Makineria	
Emri i vizatimit: Përdhesa	
Punuar nga: BSc Liridon Sejdiu	Kontrolluar nga: IDA. Njomza Hoti
Data: 08/2025	Rishikim:
Shkalla e zvogëlimit: P=1:100	Nr. i faqes: 02