



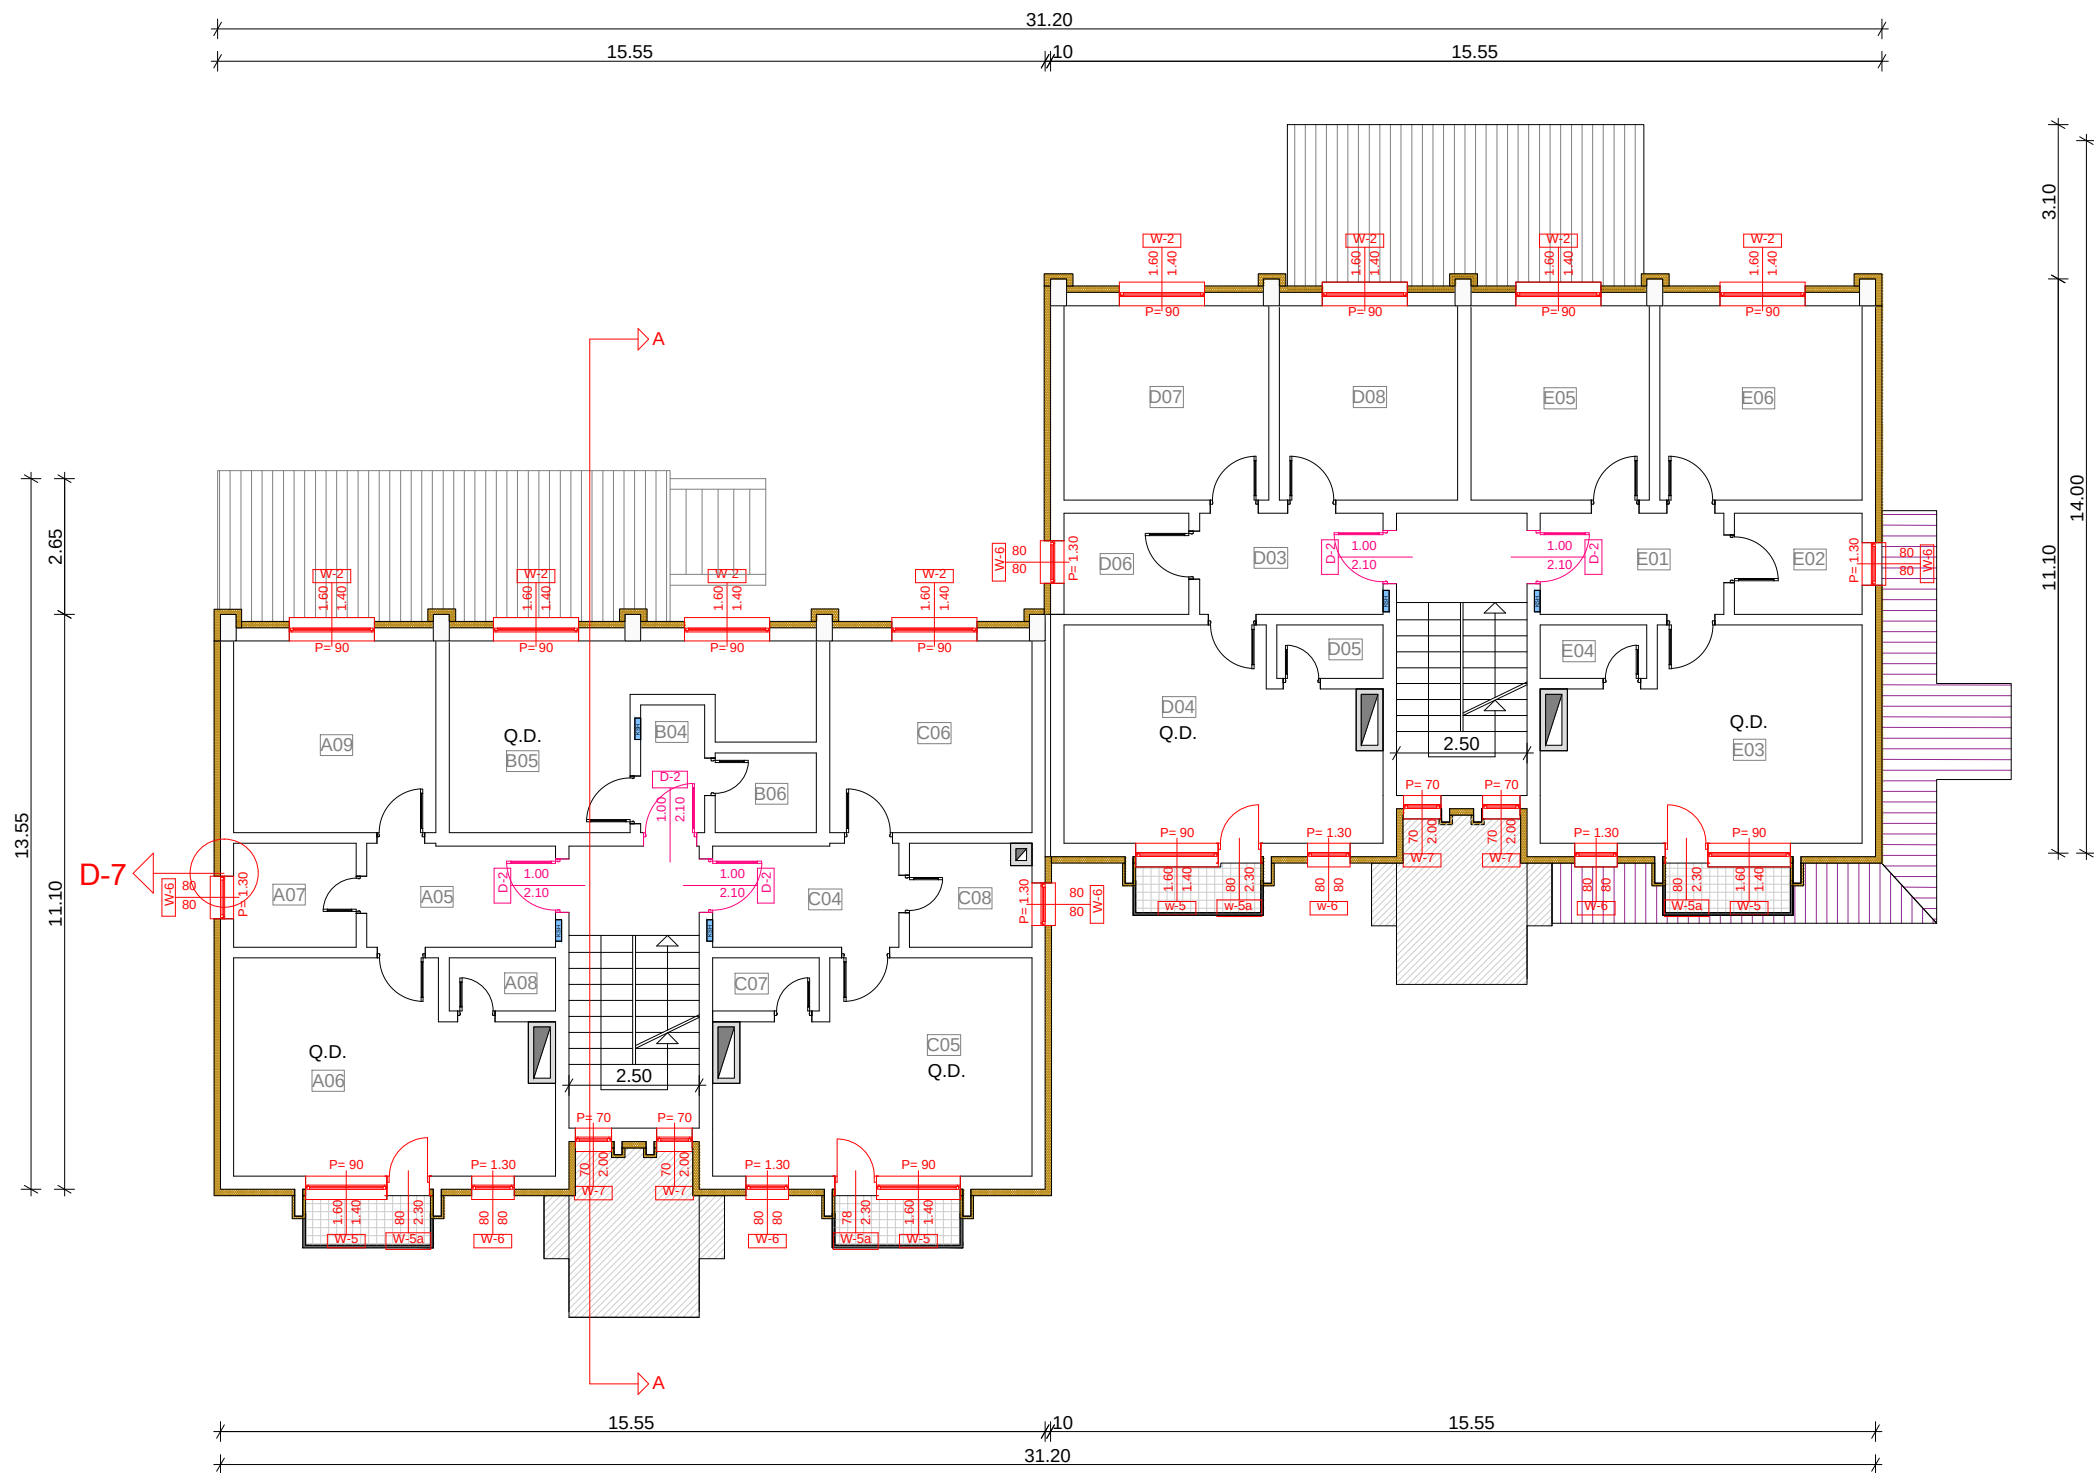

Përshkrimi i renovimit

- Termoizolimi i mureve me EPS t=12cm
- Ndërrimi i dritareve
- Ndërrimi i dyerve
- Ndërrimi i llamarinës të kulmeve të anekseve
- Renovimi i strehës së hyrjes
- Renovimi i ballkoneve

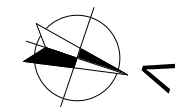

REPUBLIKA E KOSOVËS / REPUBLIC OF KOSOVO
Fondi i Kosovës për Eficiencë të Energjisë
Kosovo Energy Efficiency Fund

Projekti:

Angazhimi i Kompanive për kryerje të punëve ndërtimore për implementimin e masave të Eficiencës së Energjisë në ndërtesat shumë banesore sociale

Nr. Prokurimit : VET-FKEE2020-24-1699-S-1-1/C70 LOT 5

Kompania punëkryese:



ATC COM SHPK & DAITING SHPK

nnpatcom@gmail.com

Emri i ndërtesës:

**Ndërtesa shumë-banesore sociale II_15,
Klinë - Lot 5**

Faza e projektimit:

Arkitektura

Emri i vizatimit:

Kati I

Punuar nga:

BSc Liridon Sejdiu

Kontrolluar nga:

IDA. Njomza Hoti

Data:

08/2025

Rishikim:

Shkalla e zvogëlimit:

P=1:100

Nr. i faqes:

03