
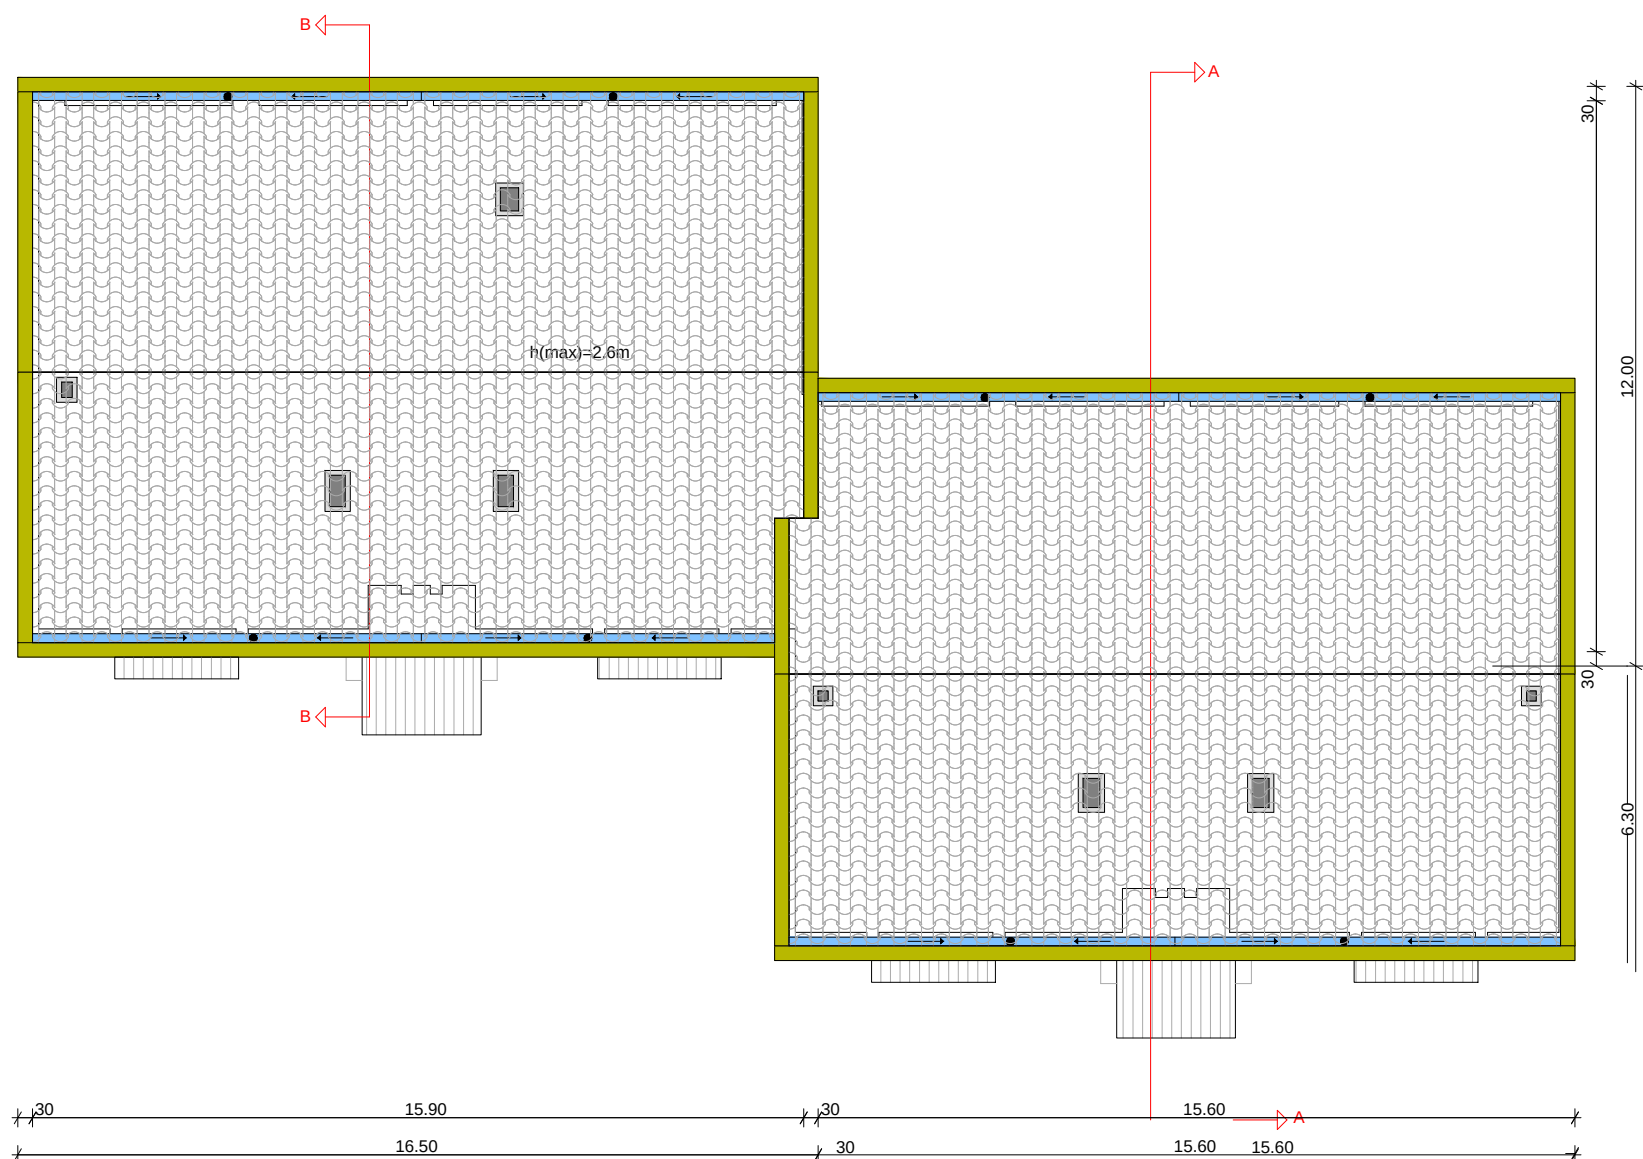
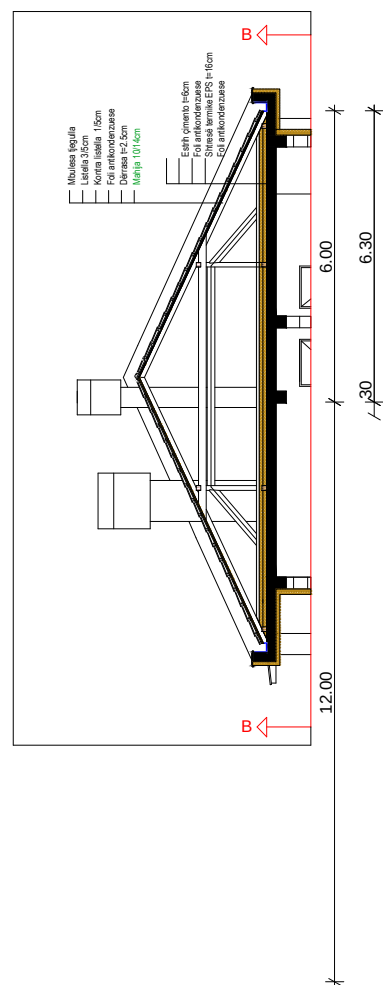


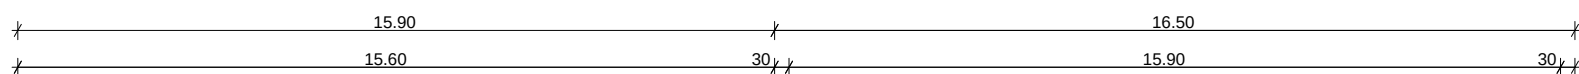

- Renovimi dhe termoizolimi i kulmit me EPS t=16cm
- Ndërrimi i ulluqeve horizontale
- Ndërrimi i ulluqeve vertikale
- Ndërrimi i pikores
- Ndërrimi i llamarinës së ballkonave

 FKEE KOSOVAN ENERGY EFFICIENCY FUND KOSOVAN ENERGIJE EFTESHSIS FUND REPUBLIKA E KOSOVES / REPUBLIC OF KOSOVO Fondi i Kosovës për Eficiencë të Energjisë Kosovo Energy Efficiency Fund	
Projekti: Angazhimi i Kompanive për kryerje të punëve ndërtimore për implementimin e masave të Eficiencës së Energjisë në ndërtesat shumë banesore sociale	
Nr. i kontratës: VET-FKEE2020-23-3696-2-1-1/C35_Lot 5	
 ATC CON SHPK & DITJING SHPK nppatccom@gmail.com	
Emri i ndërtesës: Ndërtesa shumë banesore sociale III, Klinë - Lot 5	
Faza e projektit: Arkitektura	
Emri i vizatimit: Kulmi	
Punuar nga: BSc Liridon Sejdlu	Kontrolluar nga: IDA. Njomza Hoti
Datë: 08/2025	Rishikim:
Shkala e zvogëlimit:	Nr. i faqes:
P:1:100	05