



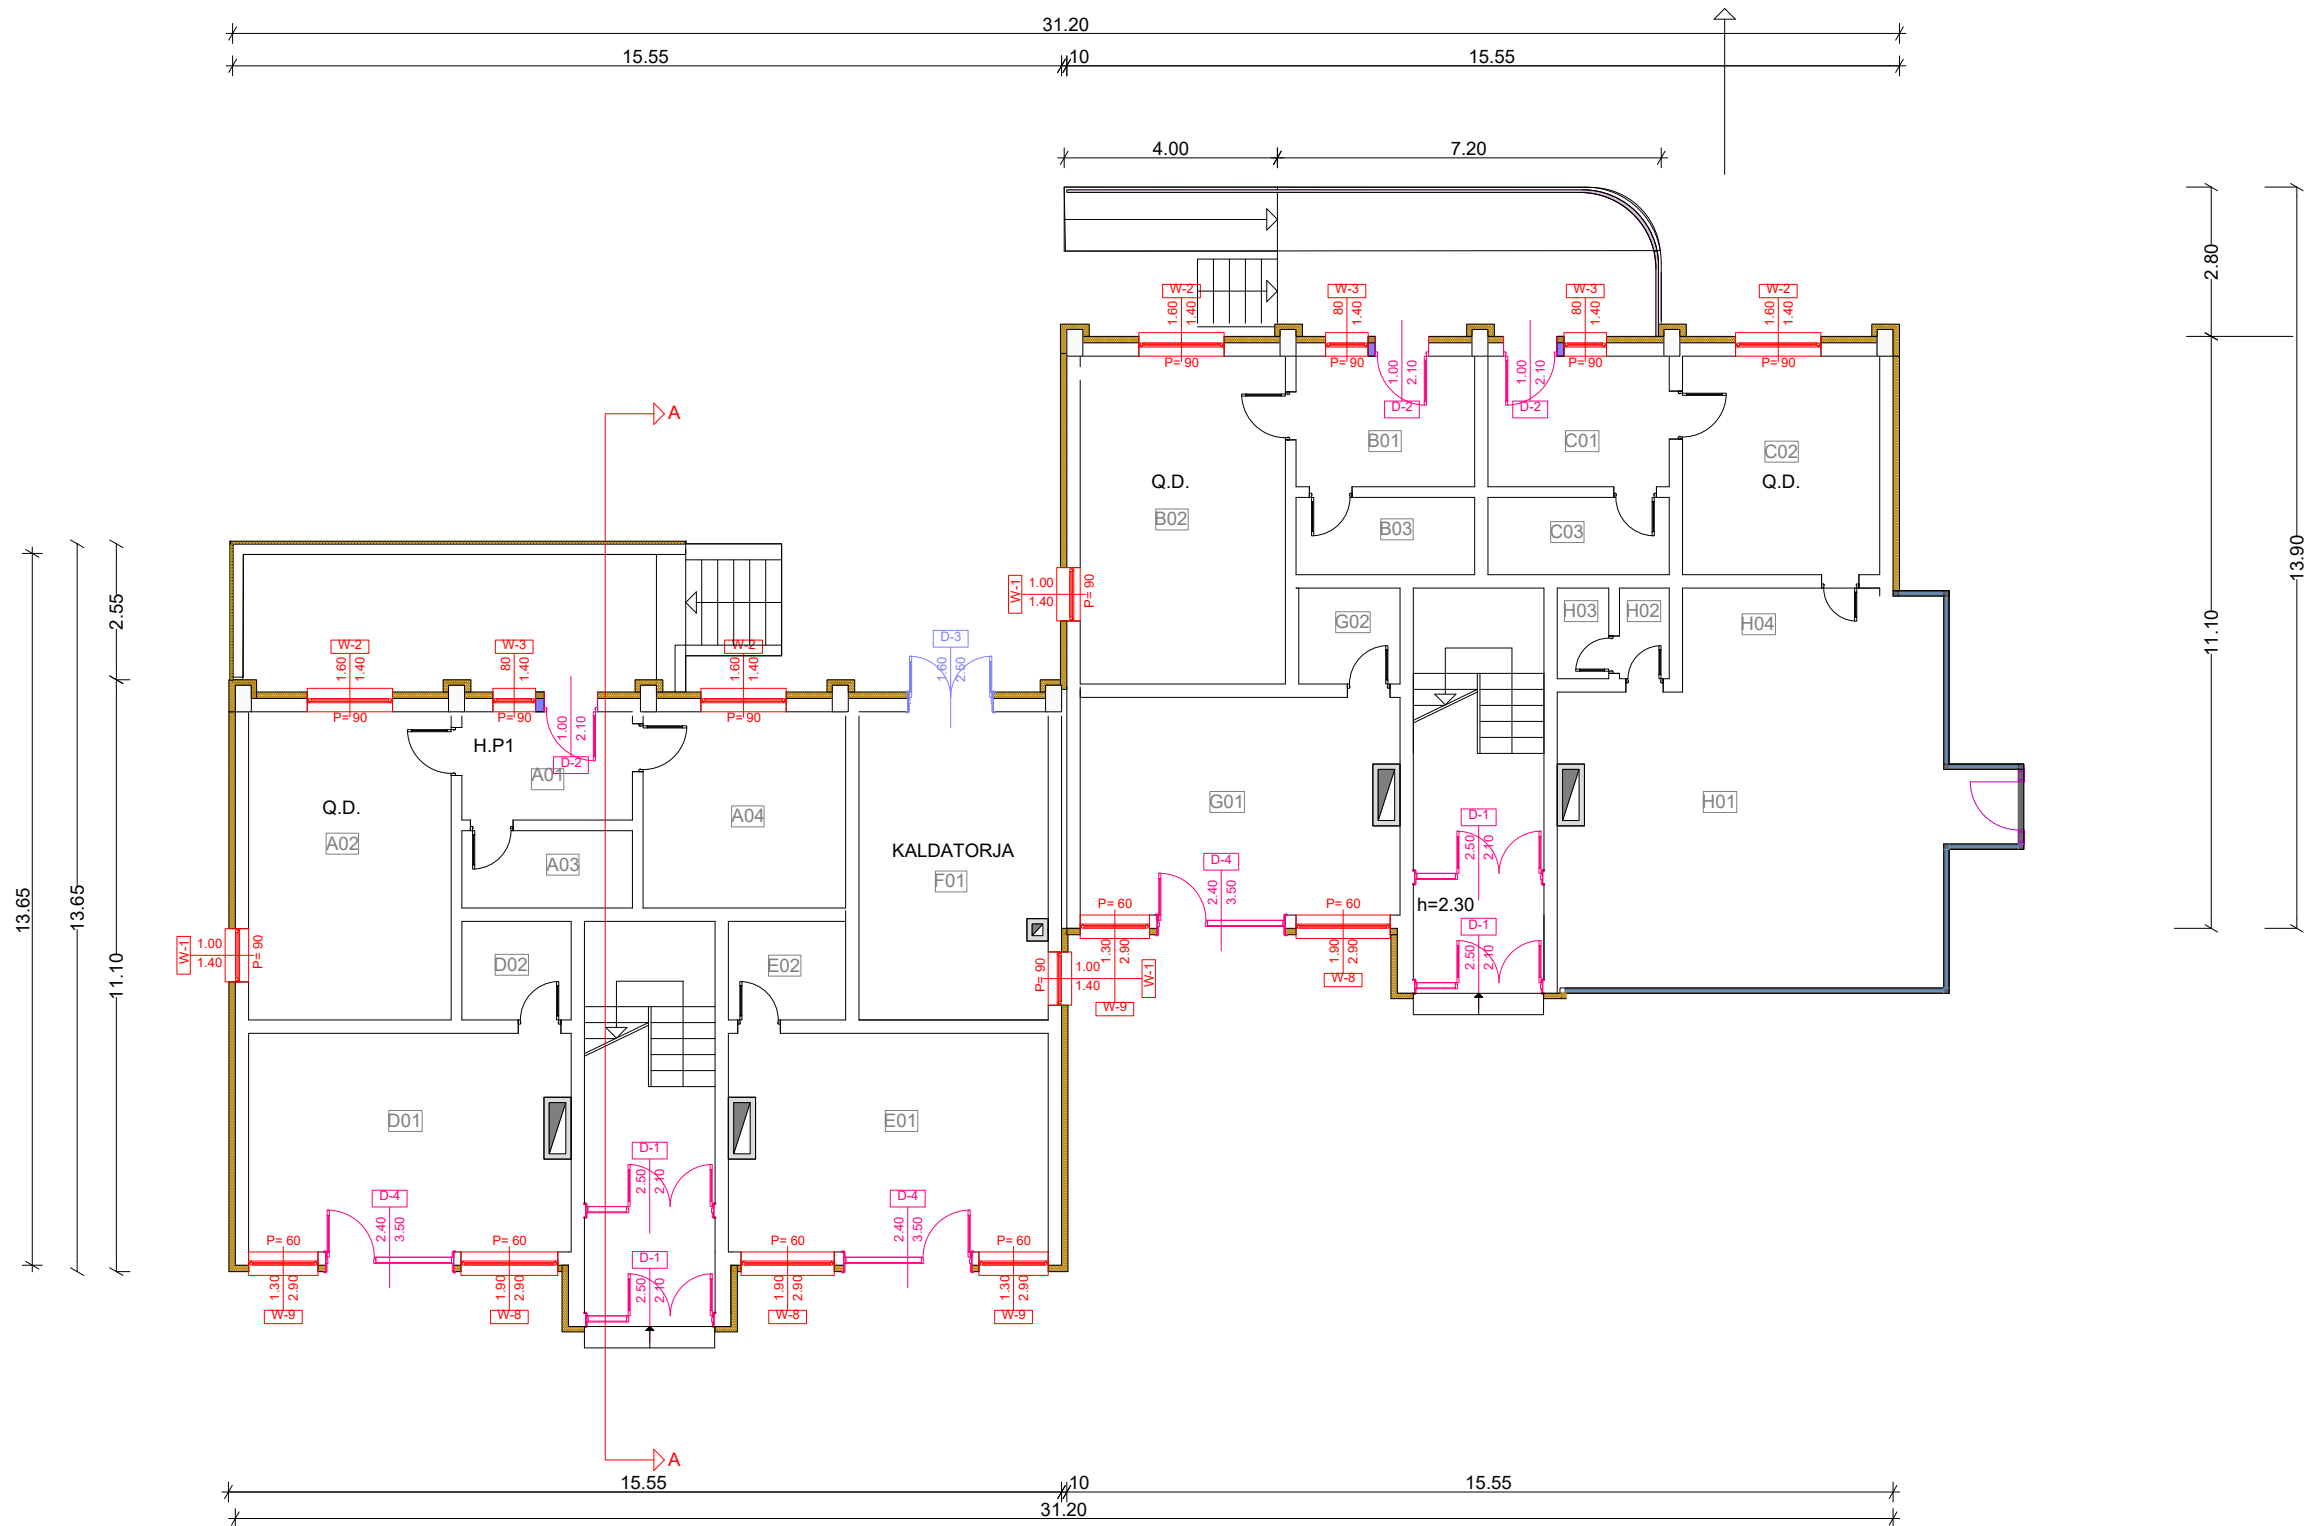

Përshkrimi renovimit

- Termoizolimi i mureve me EPS t=12cm
- Ndërrimi i dritareve
- Ndërrimi i dyerve
- Ngjyrose dhe renovimi i derës ekzistuese
- Muratim

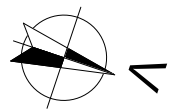

REPUBLIKA E KOSOVËS / REPUBLIC OF KOSOVO
Fondi i Kosovës për Eficiencë të Energjisë
Kosovo Energy Efficiency Fund

Projekti:
Angazhimi i Kompanie për kryerje të punëve ndërtimore për implementimin e masave të Eficiencës së Energjisë në ndërtesat shumë banesore sociale

Nr. Prokurimit : VET-FKEE2020-24-1699-S-1-1/C70 LOT 5



ALL TYPES OF CONSTRUCTION

ATC COM SHPK & DAITING SHPK
nnpatccom@gmail.com

Emri i ndërtuesit:
Ndërtesa shumë-banesore sociale II_15, Klinë - Lot 5

Faza e projektit:
Arkitektura

Emri i vizatimit:
Përdhesa

Punuar nga:
BSc Liridon Sejdiu

Kontrolluar nga:
IDA. Njomza Hoti

Datë:
08/2025

Rishikim:

Shkalla e zvogëlimit:
P=1:100

Nr. i faqes:
02