
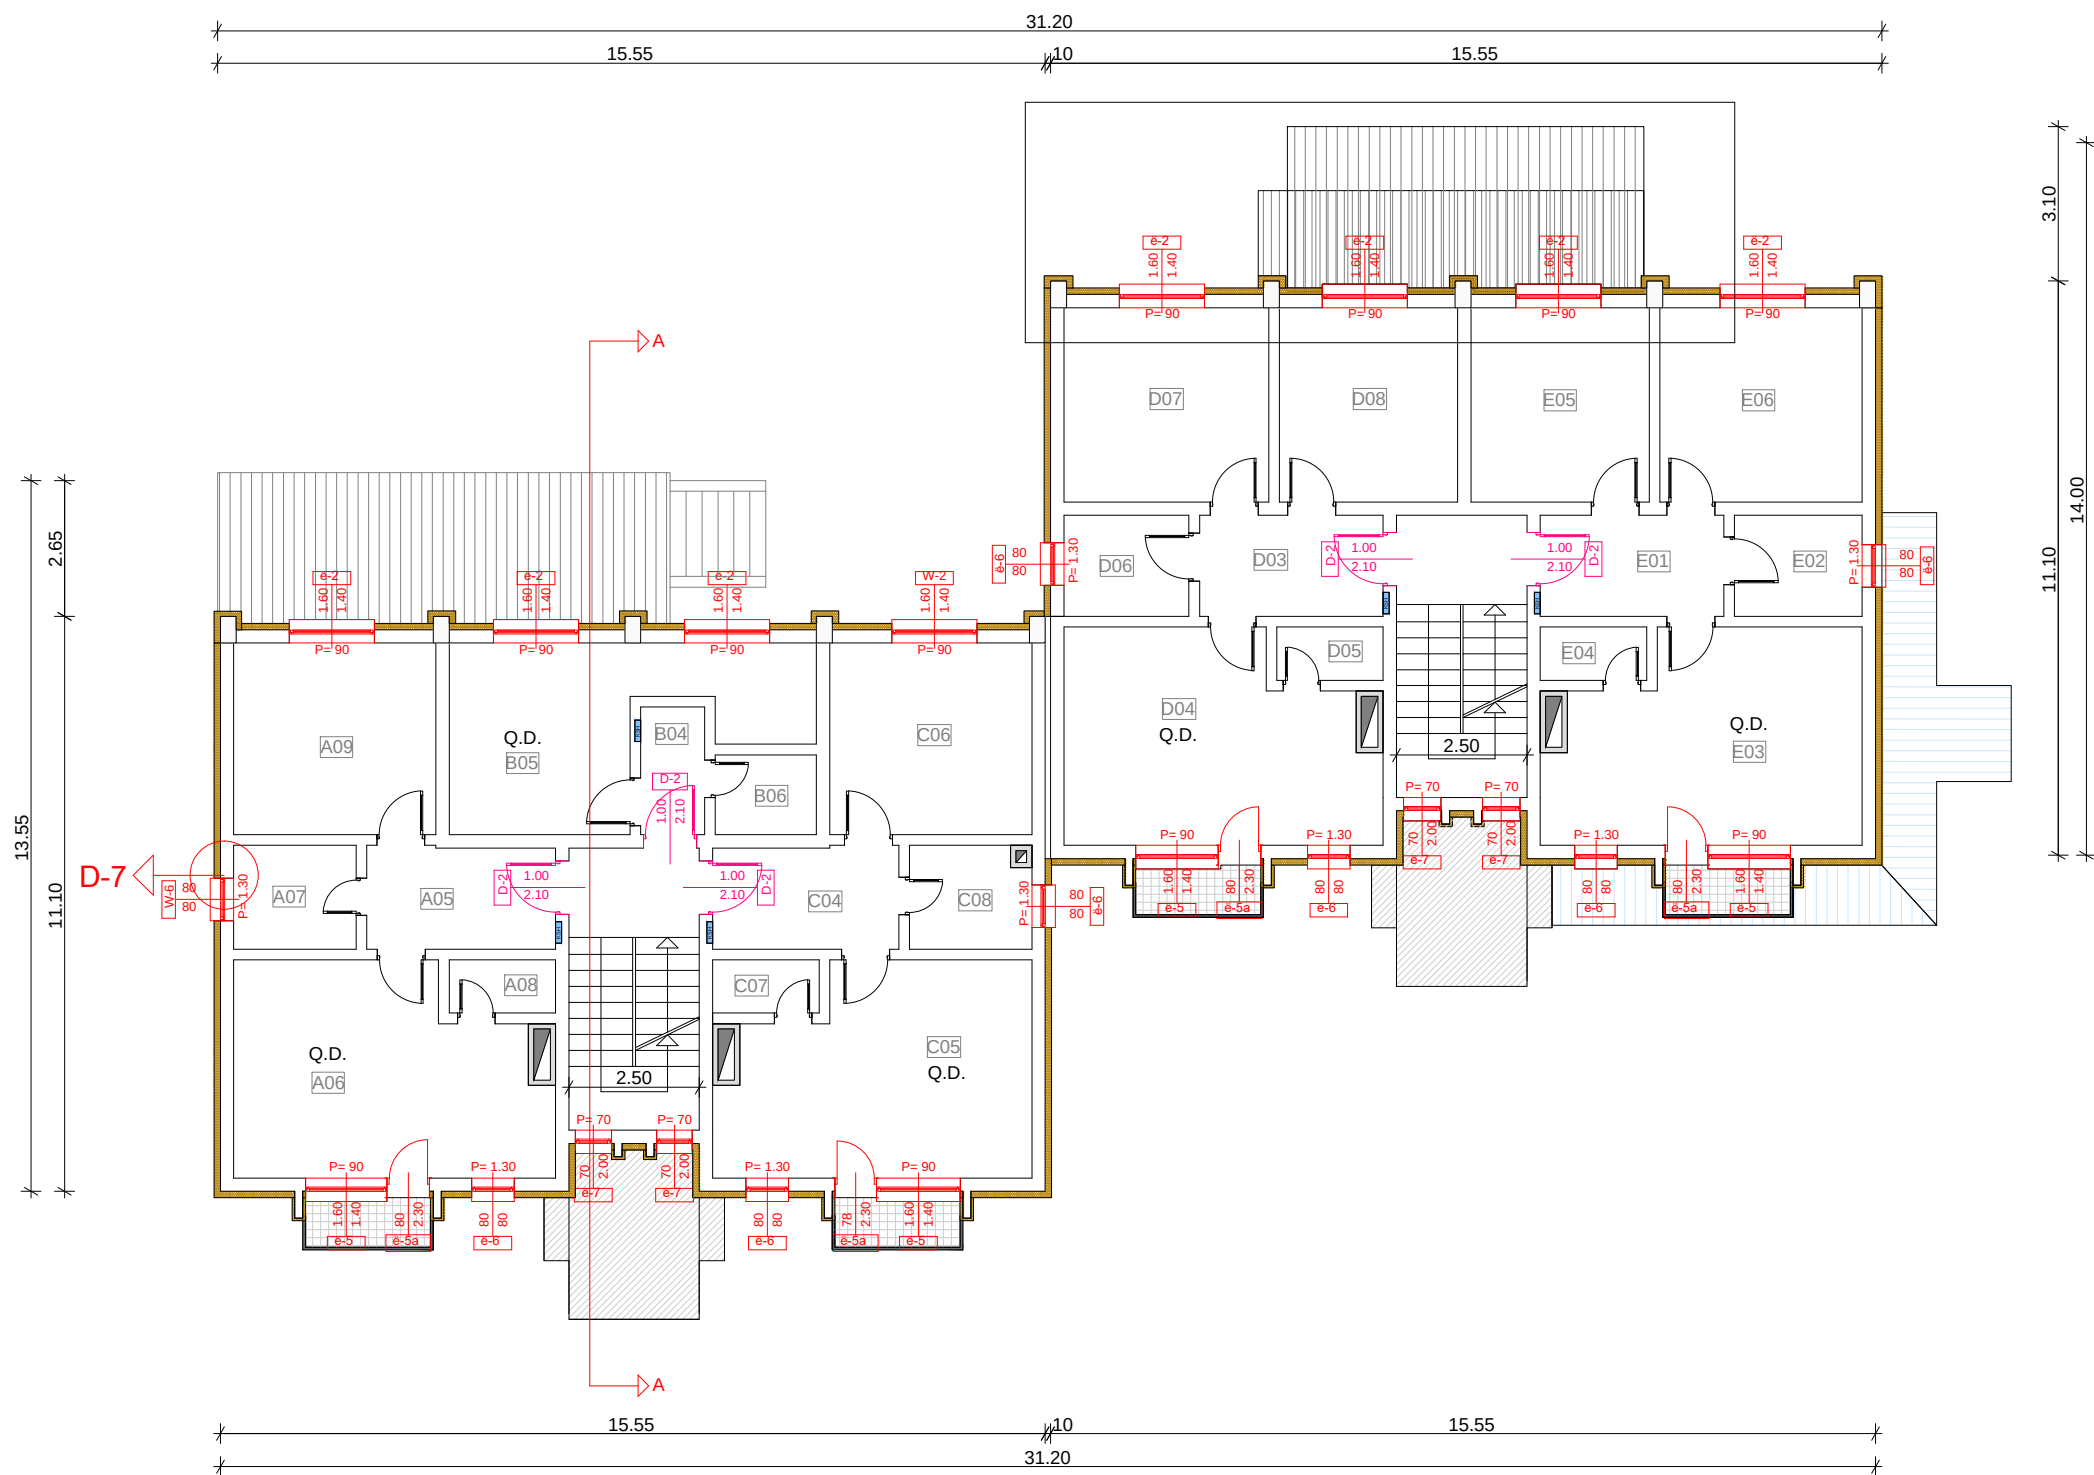


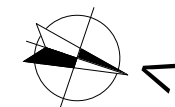

Përshkrimi i renovimit

- Termoizolimi i mureve me EPS t=12cm
- Ndërrimi i dritareve
- Ndërrimi i dyerve
- Demontimi i kulmit të aneksit
- Renovimi i strehës së hyrjes
- Renovimi i ballkoneve
- Kulm i ri

 REPUBLIKA E KOSOVËS / REPUBLIC OF KOSOVO Fondi i Kosovës për Eficiencë të Energjisë Kosovo Energy Efficiency Fund	
Projekti: Angazhimi i Kompanive për kryerje të punëve ndërtimore për implementimin e masave të Eficiencës së Energjisë në ndërtesat shumë banesore sociale	
Nr. Prokurimit : VET-FKEE2020-24-1699-S-1-1/C70 LOT 5	
Kompania punëkryese:  ATC COM SHPK & DAITING SHPK nnpatcom@gmail.com	
Emri i ndërtesës: Ndërtesa shumë-banesore sociale II_15, Klinë - Lot 5	
Faza e projektimit: Arkitektura	
Emri i vizatimit: Kati I	
Punuar nga: BSc Liridon Sejdiu	Kontrolluar nga: IDA. Njomza Hoti
Datë: 08/2025	Rishikim:
Shkalla e zvogëlimit: P=1:100	Nr. i faqes: 03