
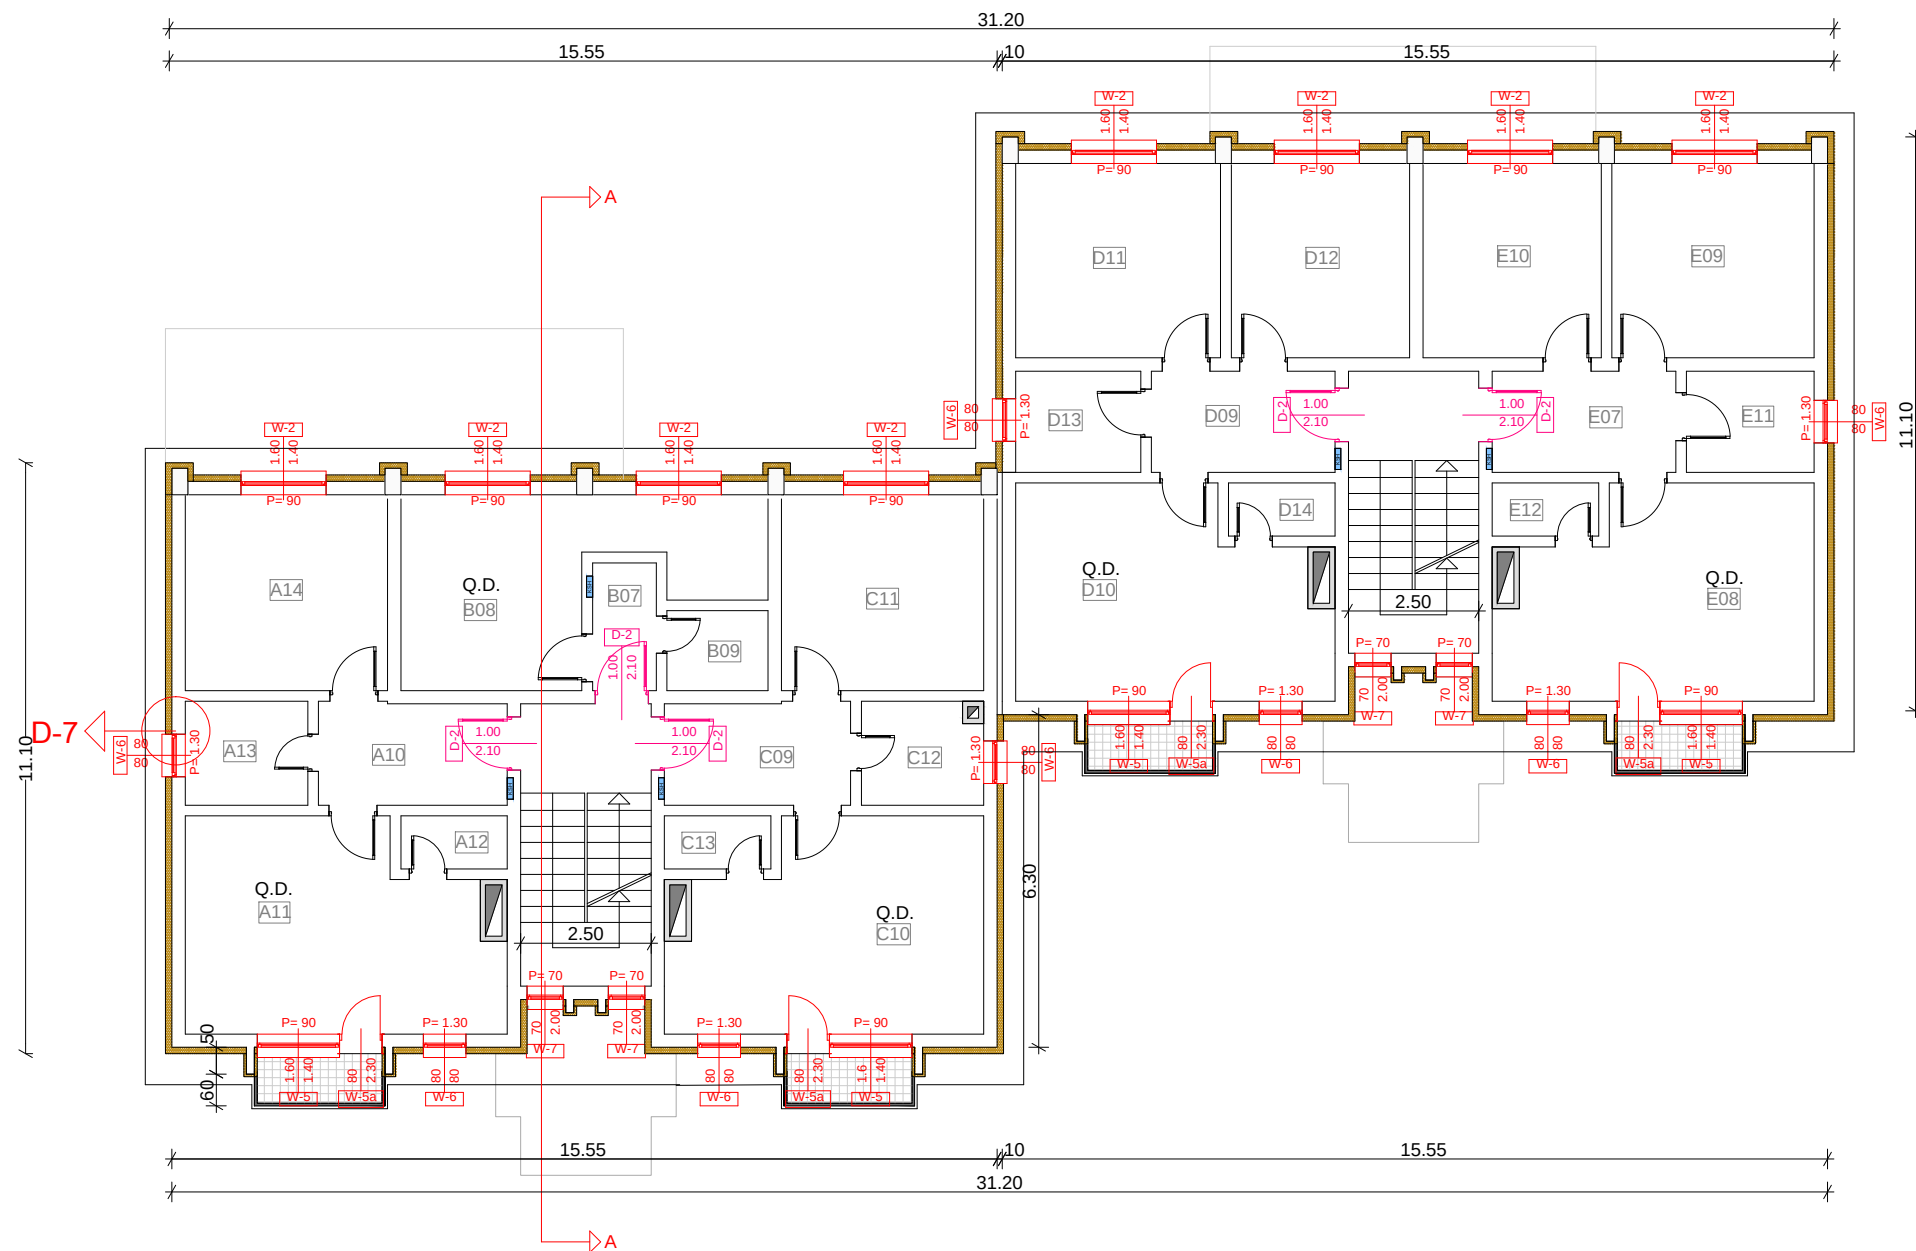


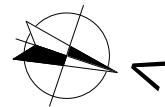

#### Përshkrimi i renovimit

- Termoizolimi i mureve me EPS t=12cm
- Ndërrimi i dritareve
- Ndërrimi i detyrve
- Renovimi i ballkoneve

|   |                                             |
|---|---------------------------------------------|
| <br><b>REPUBLIKA E KOSOVËS / REPUBLIC OF KOSOVO</b><br>Fondi i Kosovës për Eficiencë të Energjisë<br>Kosovo Energy Efficiency Fund             |                                             |
| Projekti:<br>Angazhimi i Kompanive për kryerje të punëve ndërtimore për implementimin e masave të Eficiencës së Energjisë në ndërtesat shumë banesore sociale                                                                       |                                             |
| Nr. Prokurimit : VET-FKEE2020-24-1699-S-1-1/C70 LOT 5<br>Kompania punëkryese:<br> <b>ATC COM SHPK &amp; DAITING SHPK</b><br>nnpatcom@gmail.com |                                             |
| Emri i ndërtesës:<br><b>Ndërtesa shumë-banesore sociale II_15, Klinë - Lot 5</b>   |                                             |
| Faza e projektimit:<br><b>Arkitektura</b>   |                                             |
| Emri i vizatimit:<br><b>Kati II-IV</b>   |                                             |
| Punuar nga:<br>BSc Liridon Sejdiu   | Kontrolluar nga:<br><b>IDA. Njomza Hoti</b> |
| Data:<br>08/2025   | Rishikim:                                   |
| Shkalla e zvogëlimit:<br>P=1:100   | Nr. i faqes:<br><b>04</b>                   |