

REPUBLIKA E KOSOVËS / REPUBLIC OF KOSOVO
Fondi i Kosovës për Eficiencë të Energjisë
Kosovo Energy Efficiency Fund

Projekti:
Angazhimi i Kompanive për kryerje të punëve ndërtimore për
implementimin e masave të Eficiencës së Energjisë në ndërtesat
shumë banesore sociale

Nr. i kontratës: VET-FKEE2020-23-3696-2-1-1/C35_Lot 5

Kompania punëkryese





ATC COM SHPK & DAIJING SHPK
nnpatcom@gmail.com

Emri i ndërtesës:
**Ndërtesa shumë-banesore sociale II_15,
Klinë - Lot 5**

Faza e projektimit:
Arkitektura

Emri i vizatimit:
Lokacioni i ndërtesës



Punuar nga: BSc Liridon Sejdiu	Kontrolluar nga: IDA. Njomza Hoti
Datë: 08/2025	Rishikim:
Shkalla e zvogëlimit:	Nr. i faqes: 01

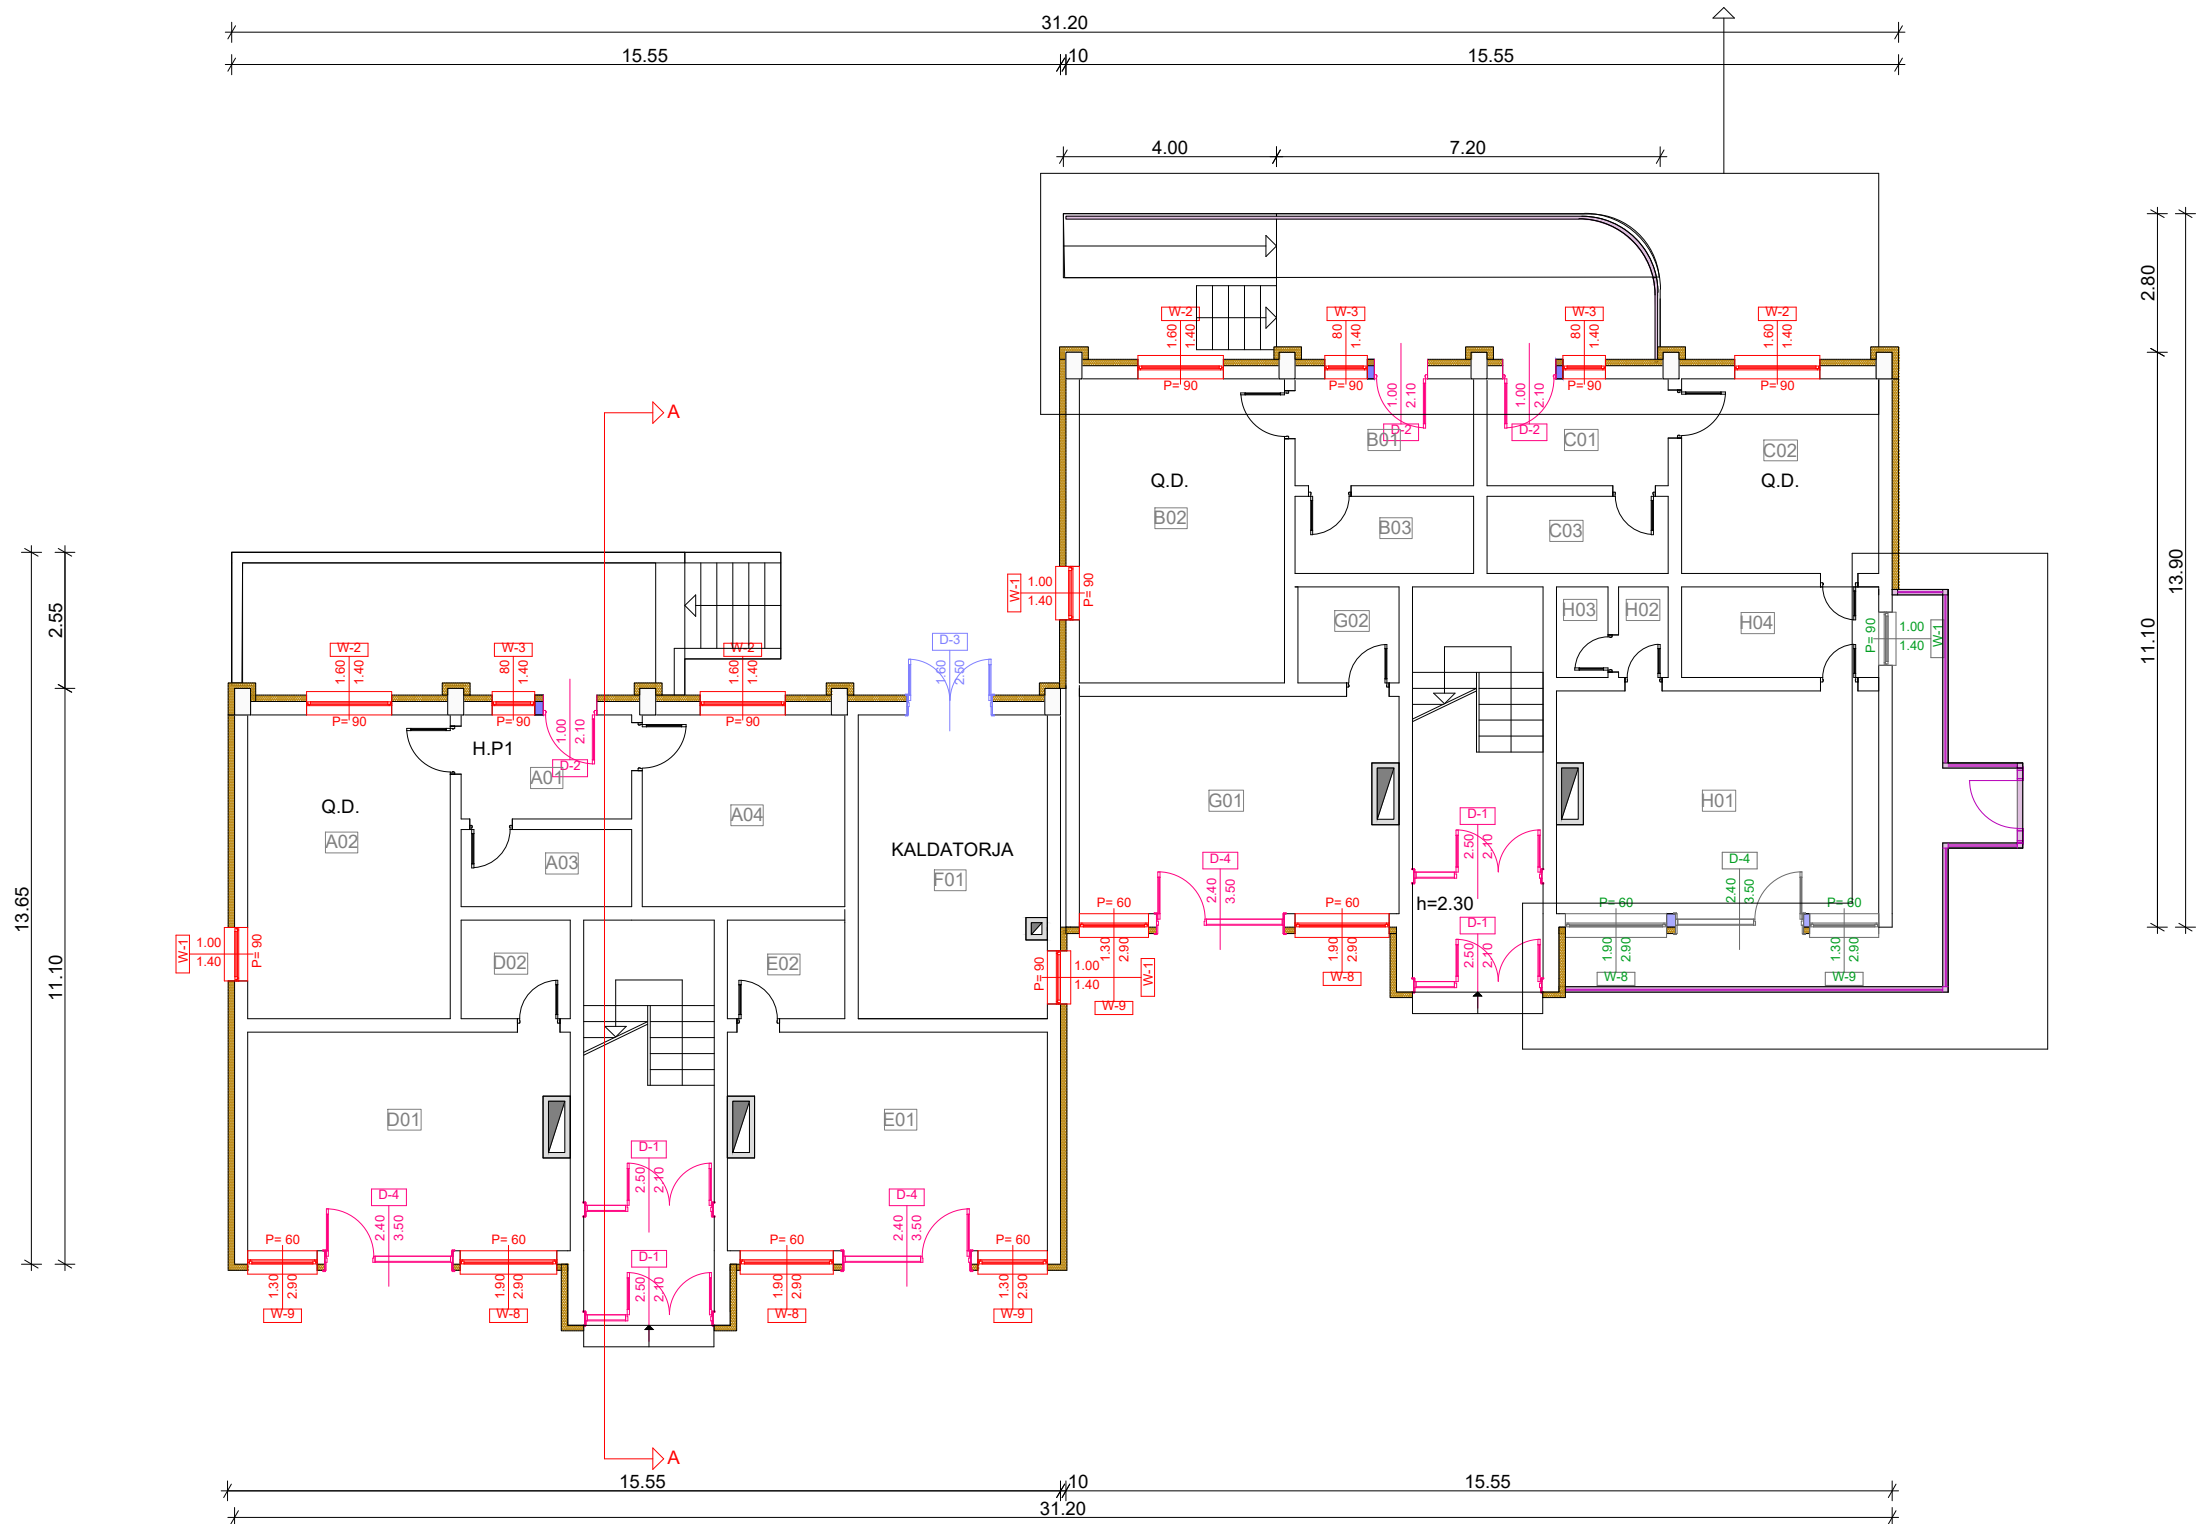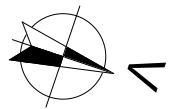

Përshkrimi renovimit

- Termoizolimi i mureve me EPS t=12cm
- Ndërrimi i dritareve
- Ndërrimi i derye
- Dyer/dritare të reja
- Ngjyrose dhe renovimi i derës ekzistuese
- Muratim
- Demontimi i aneksit
- Demolimi i aneksit



 REPUBLIKA E KOSOVËS / REPUBLIC OF KOSOVO Fondi i Kosovës për Eficiencë të Energjisë Kosovo Energy Efficiency Fund	
Projekti: Angazhimi i Kompanive për kryerje të punëve ndërtimore për implementimin e masave të Eficiencës së Energjisë në ndërtesat shumë banesore sociale	
Nr. Prokurimit : VET-FKEE2020-24-1699-5-1-1/C70 LOT 5	
Kompania punëkryese:  ATC COM SHPK & DAITING SHPK nnpattcom@gmail.com	
Emri i ndërtesës: Ndërtesa shumë-banesore sociale II_15, Klinë - Lot 5	
Faza e projektit: Arkitektura	
Emri i vizatimit: Përdhesa	
Punuar nga: BSc Liridon Sejdiu	Kontrolluar nga: IDA. Njomza Hoti
Data: 08/2025	Rishikim:
Shkalla e zvogëlimit: P=1:100	Nr. i faqes: 02

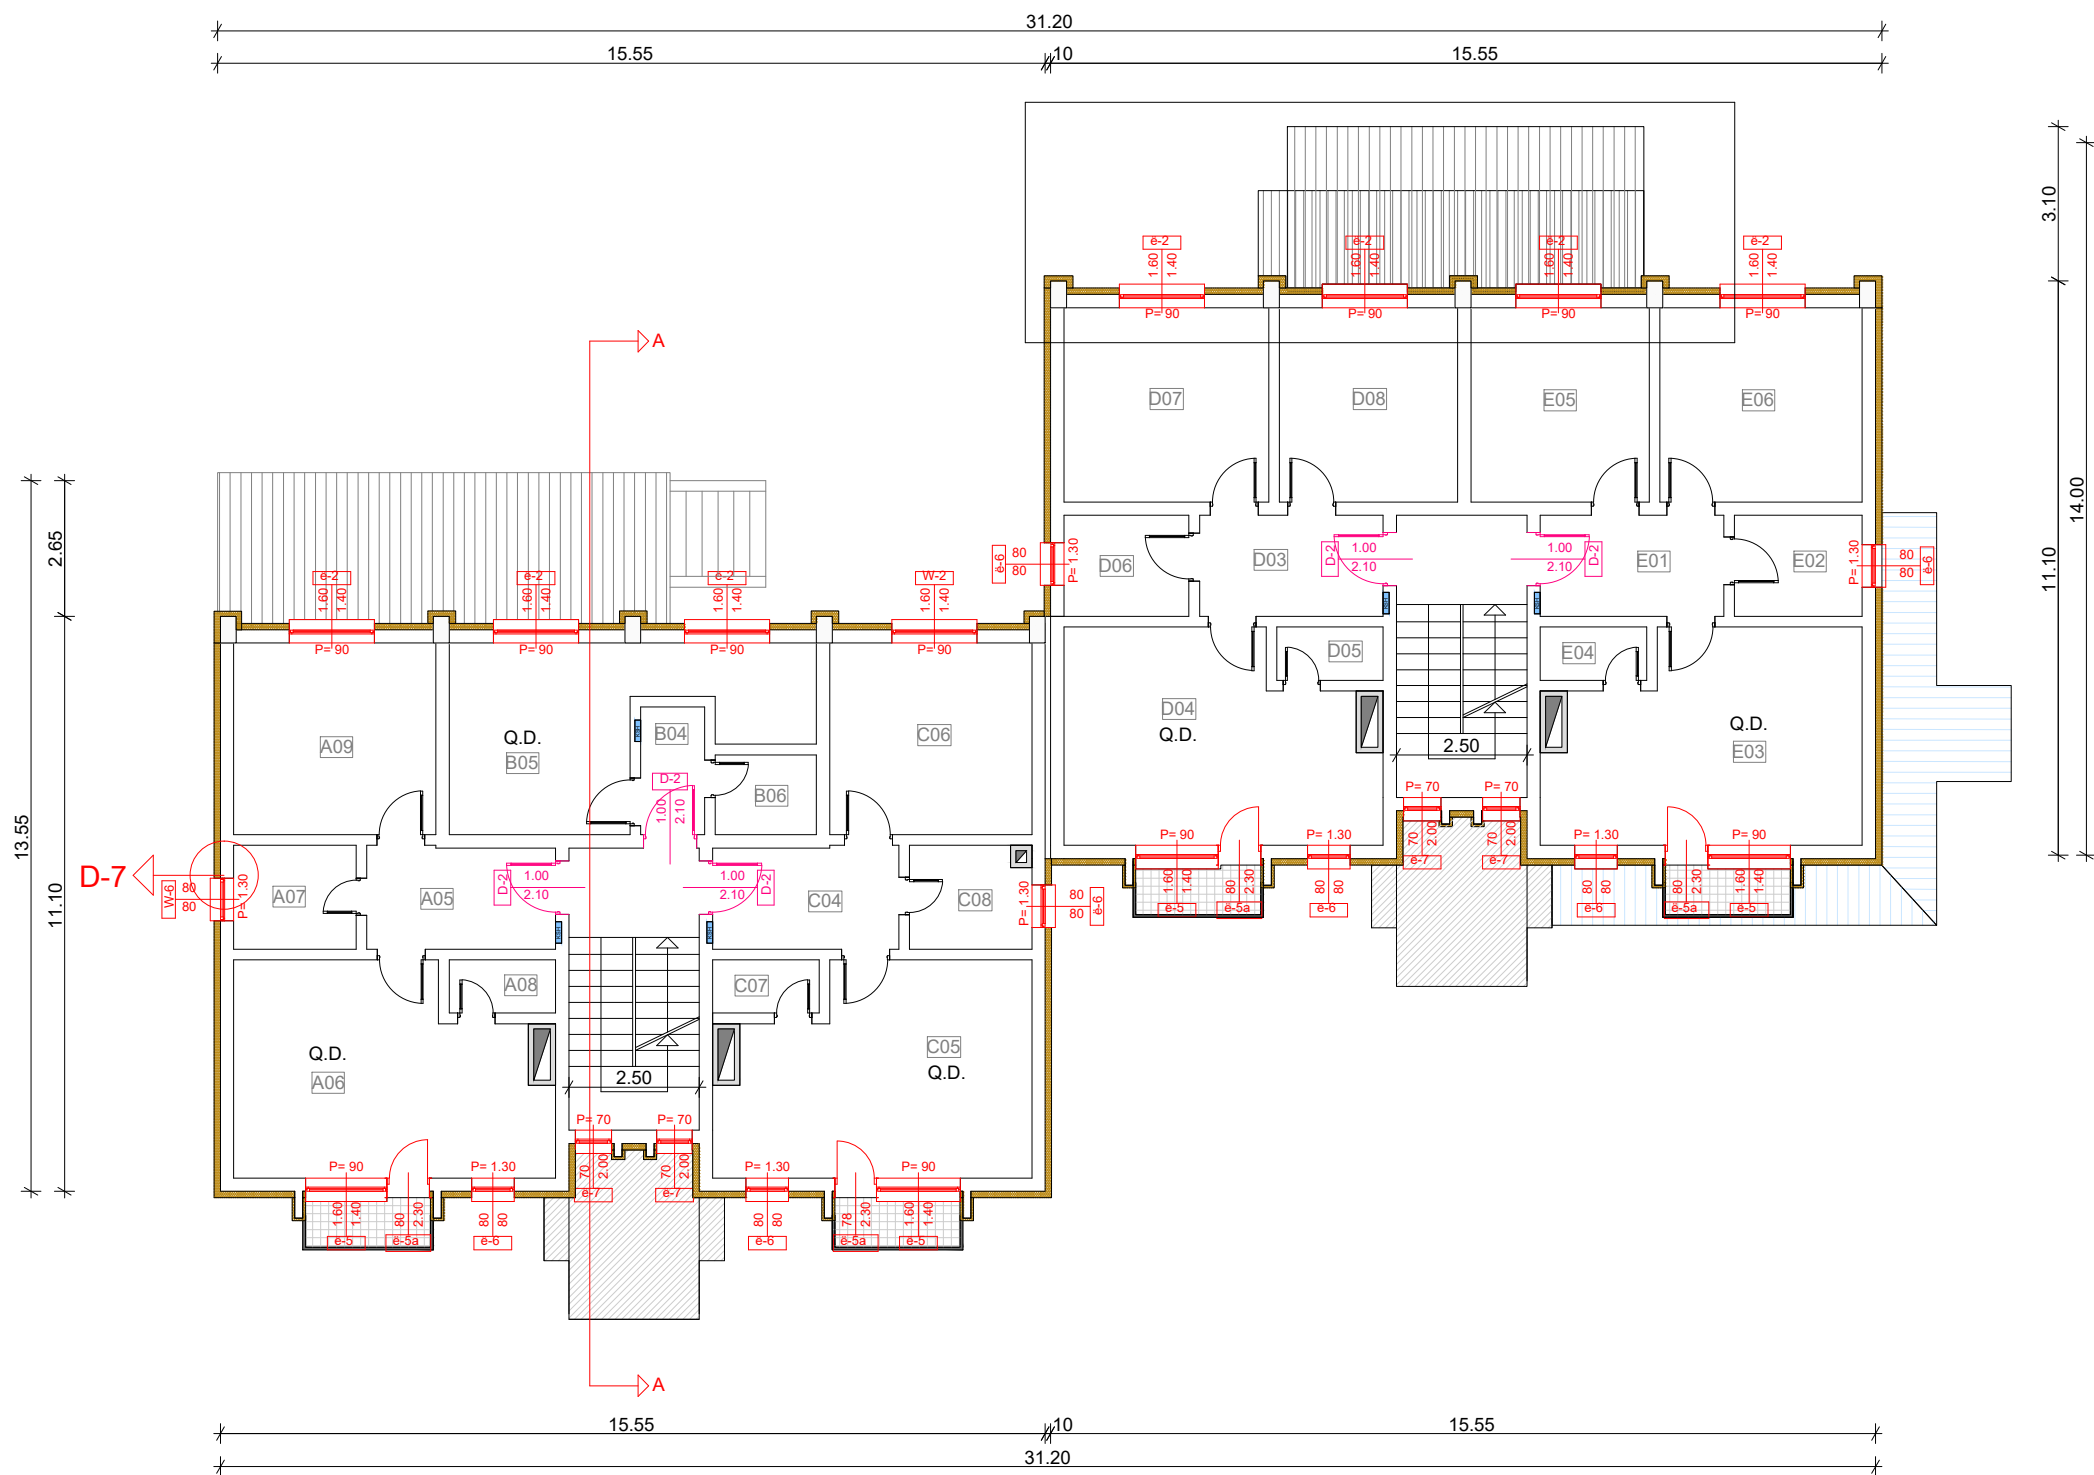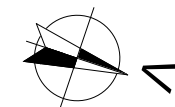

Përshkrimi i renovimit

- Termoizolimi i mureve me EPS t=12cm
- Ndërrimi i dritareve
- Ndërrimi i dyerve
- Demontimi i kulmit të aneksit
- Renovimi i strehës së hyrjes
- Renovimi i ballkoneve
- Kulm i ri


 REPUBLIKA E KOSOVËS / REPUBLIC OF KOSOVO Fondi i Kosovës për Eficiencë të Energjisë Kosovo Energy Efficiency Fund	
Projekti: Angazhimi i Kompanive për kryerje të punëve ndërtimore për implementimin e masave të Eficiencës së Energjisë në ndërtesat shumë banesore sociale	
Nr. Prokurimit : VET-FKEE2020-24-1699-S-1-1/C70 LOT 5	
Kompania punëkryese:  ATC COM SHPK & DAITING SHPK nnpatcom@gmail.com	
Emri i ndërtesës: Ndërtesa shumë-banesore sociale II_15, Klinë - Lot 5	
Faza e projektimit: Arkitektura	
Emri i vizatimit: Kati I	
Punuar nga: BSc Liridon Sejdiu	Kontrolluar nga: IDA. Njomza Hoti
Datë: 08/2025	Rishikim:
Shkalla e zvogëlimit: P=1:100	Nr. i faqes: 03

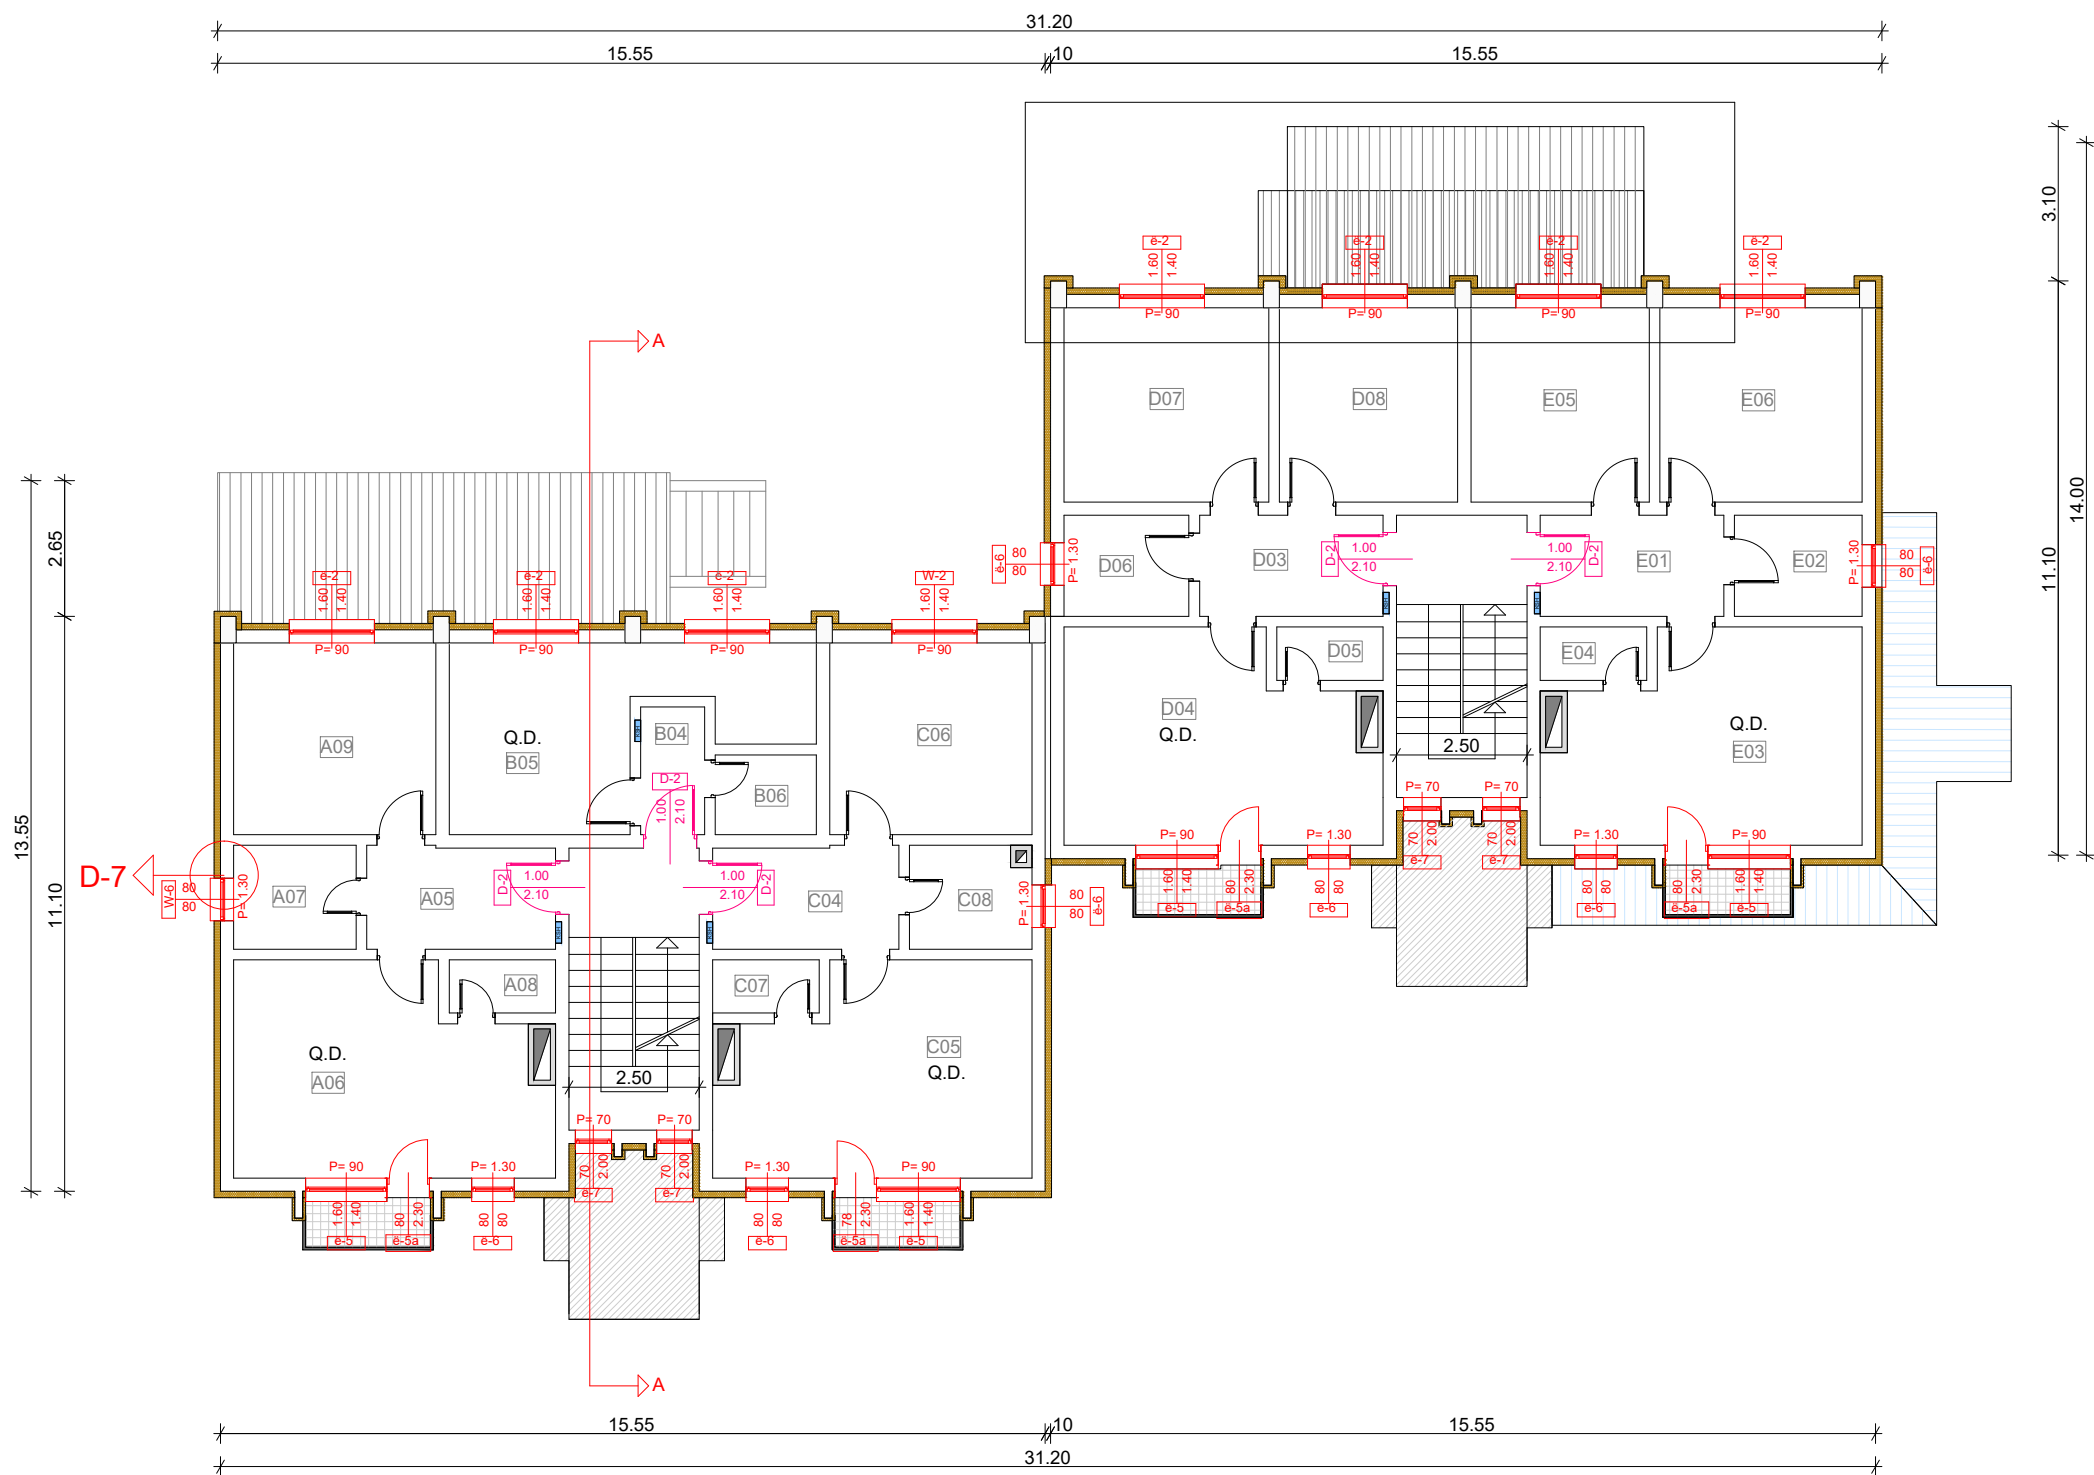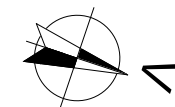

Përshkrimi i renovimit




- Termoizolimi i mureve me EPS t=12cm
- Ndërrimi i dritareve
- Ndërrimi i dyerve
- Demontimi i kulmit të aneksit
- Renovimi i strehës së hyrjes
- Renovimi i ballkoneve
- Kulm i ri

 REPUBLIKA E KOSOVËS / REPUBLIC OF KOSOVO Fondi i Kosovës për Eficiencë të Energjisë Kosovo Energy Efficiency Fund	
Projekti: Angazhimi i Kompanive për kryerje të punëve ndërtimore për implementimin e masave të Eficiencës së Energjisë në ndërtesat shumë banesore sociale	
Nr. Prokurimit : VET-FKEE2020-24-1699-S-1-1/C70 LOT 5	
Kompania punëkryese:  ATC COM SHPK & DAITING SHPK nnpatcom@gmail.com	
Emri i ndërtesës: Ndërtesa shumë-banesore sociale II_15, Klinë - Lot 5	
Faza e projektimit: Arkitektura	
Emri i vizatimit: Kati I	
Punuar nga: BSc Liridon Sejdiu	Kontrolluar nga: IDA. Njomza Hoti
Data: 08/2025	Rishikim:
Shkalla e zvogëlimit: P=1:100	Nr. i faqes: 03

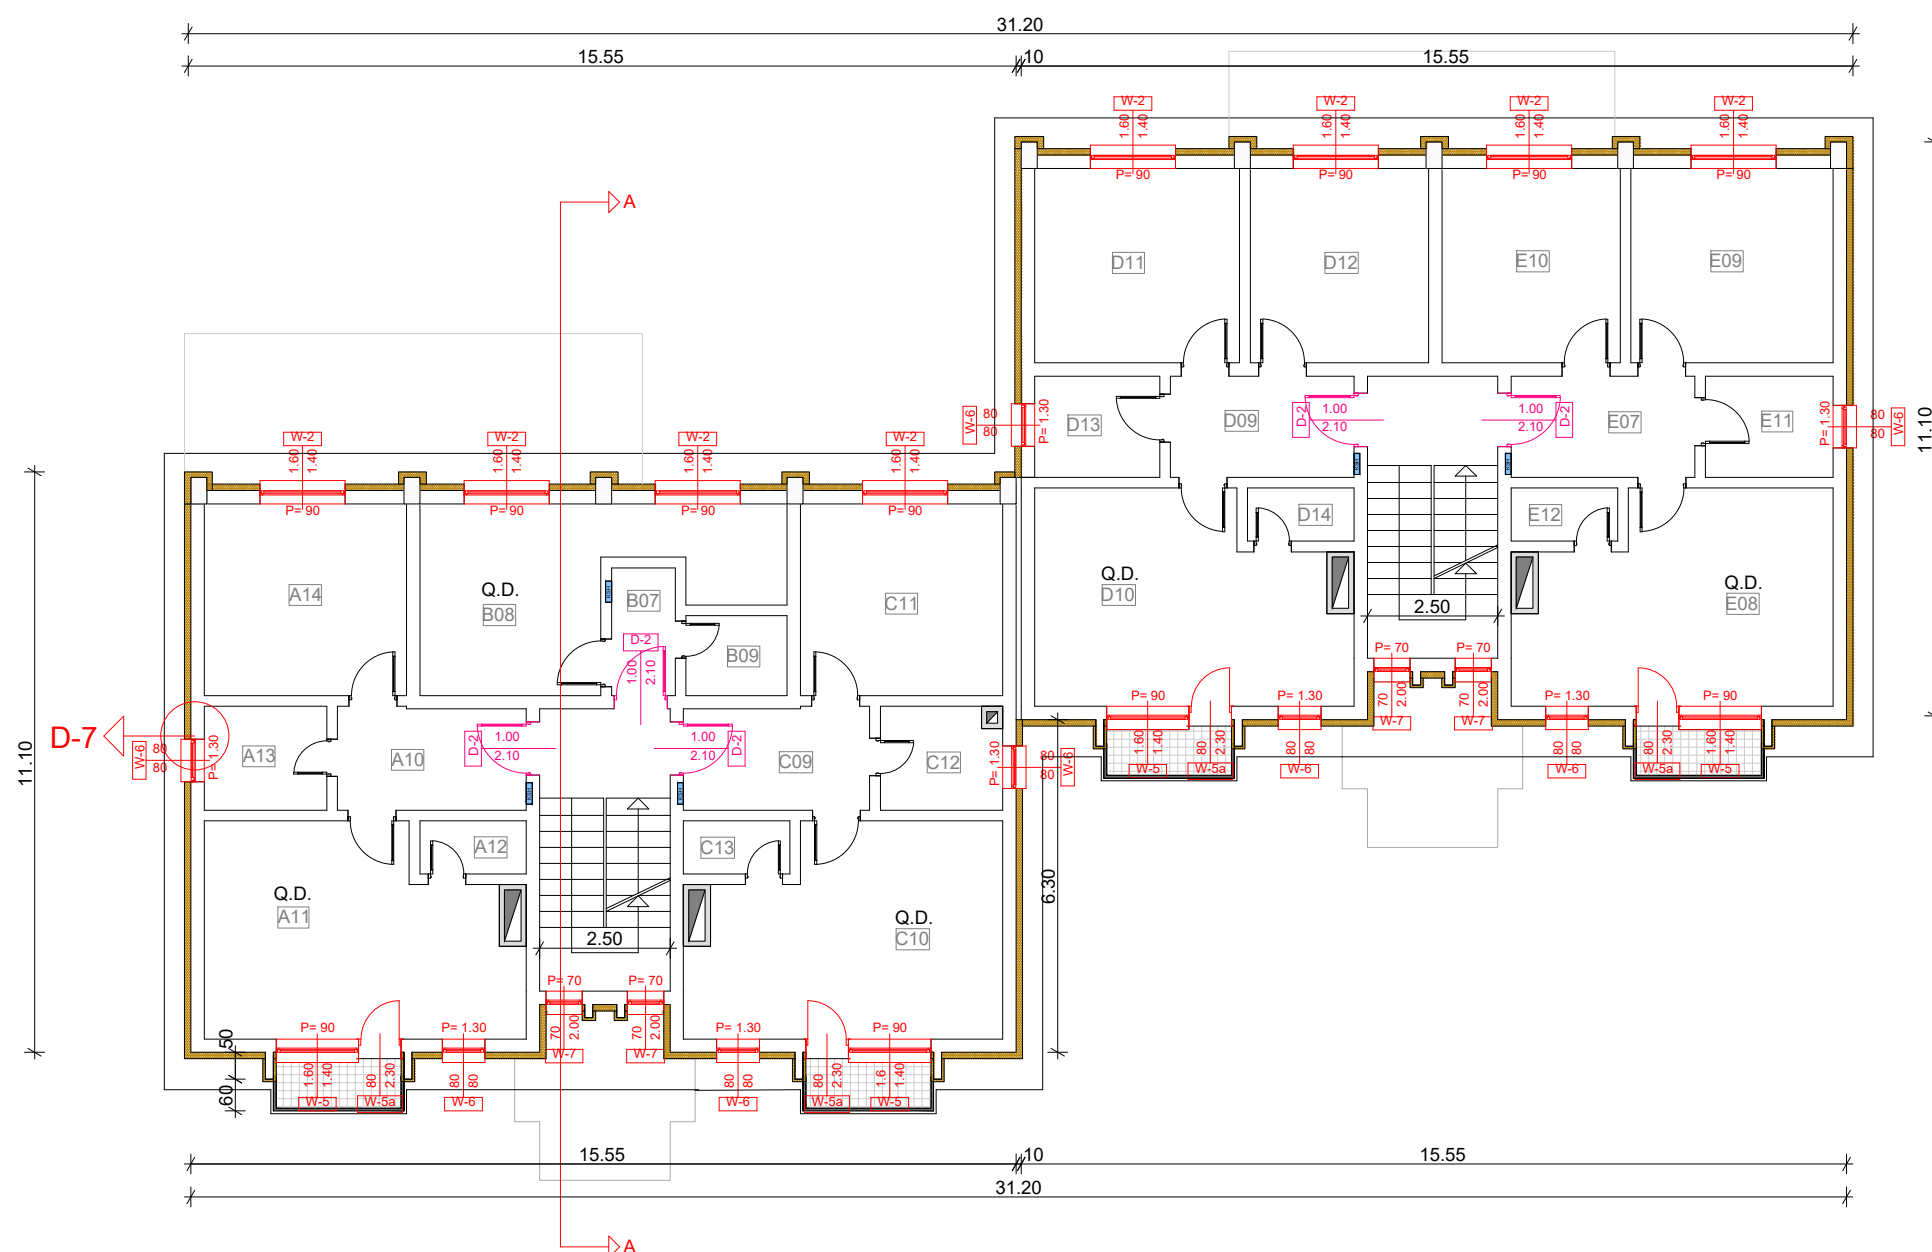

 Termoizolimi i mureve me EPS t=12cm
 Ndërrimi i dritareve
 Ndërrimi i dyerve
 Renovimi i ballkoneve




 FKEE FUNDI I KOSOVËS PËR EFICIENCË TË ENERGJISË KOSOVO ENERGY EFFICIENCY FUND	
REPUBLIKA E KOSOVËS / REPUBLIC OF KOSOVO Fondi i Kosovës për Eficiencë të Energjisë Kosovo Energy Efficiency Fund	
Projekt: Angazhimi i Kompanisë për kryerje të punëve ndërtimore për implementimin e masave të Eficiencës në Energji në ndërtesat shumë banesore sociale	
Nr. Prokurimit : VET-FKEE2020-24-1699-5-1-1/CT0 LOT 5	
Kompania punëkyese:  ATC COM SHPK & DAITING SHPK mgatccom@gmail.com	
Emri i ndërtesës: Ndërtesa shumë-banesore sociale II_15, Klinë - Lot 5	
Faza e projektimit: Arkitektura	
Emri i vizatimit: Kati II-IV	
Punuar nga: BSc Liridon Sejdiu	Kontrolluar nga: IDA. Njomza Hoti
Data: 08/2025	Rishikim:
Shkalla e zvogëlimit: P=1:100	Nr. i faqes:

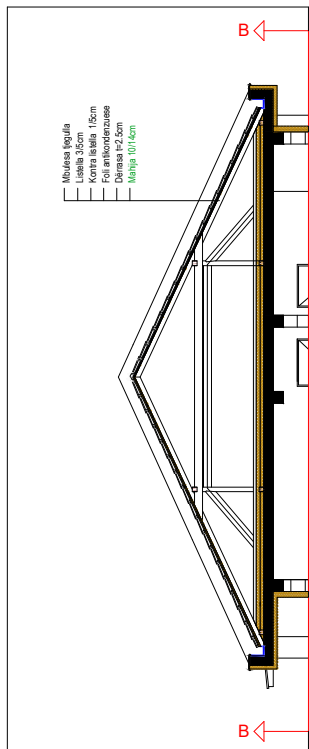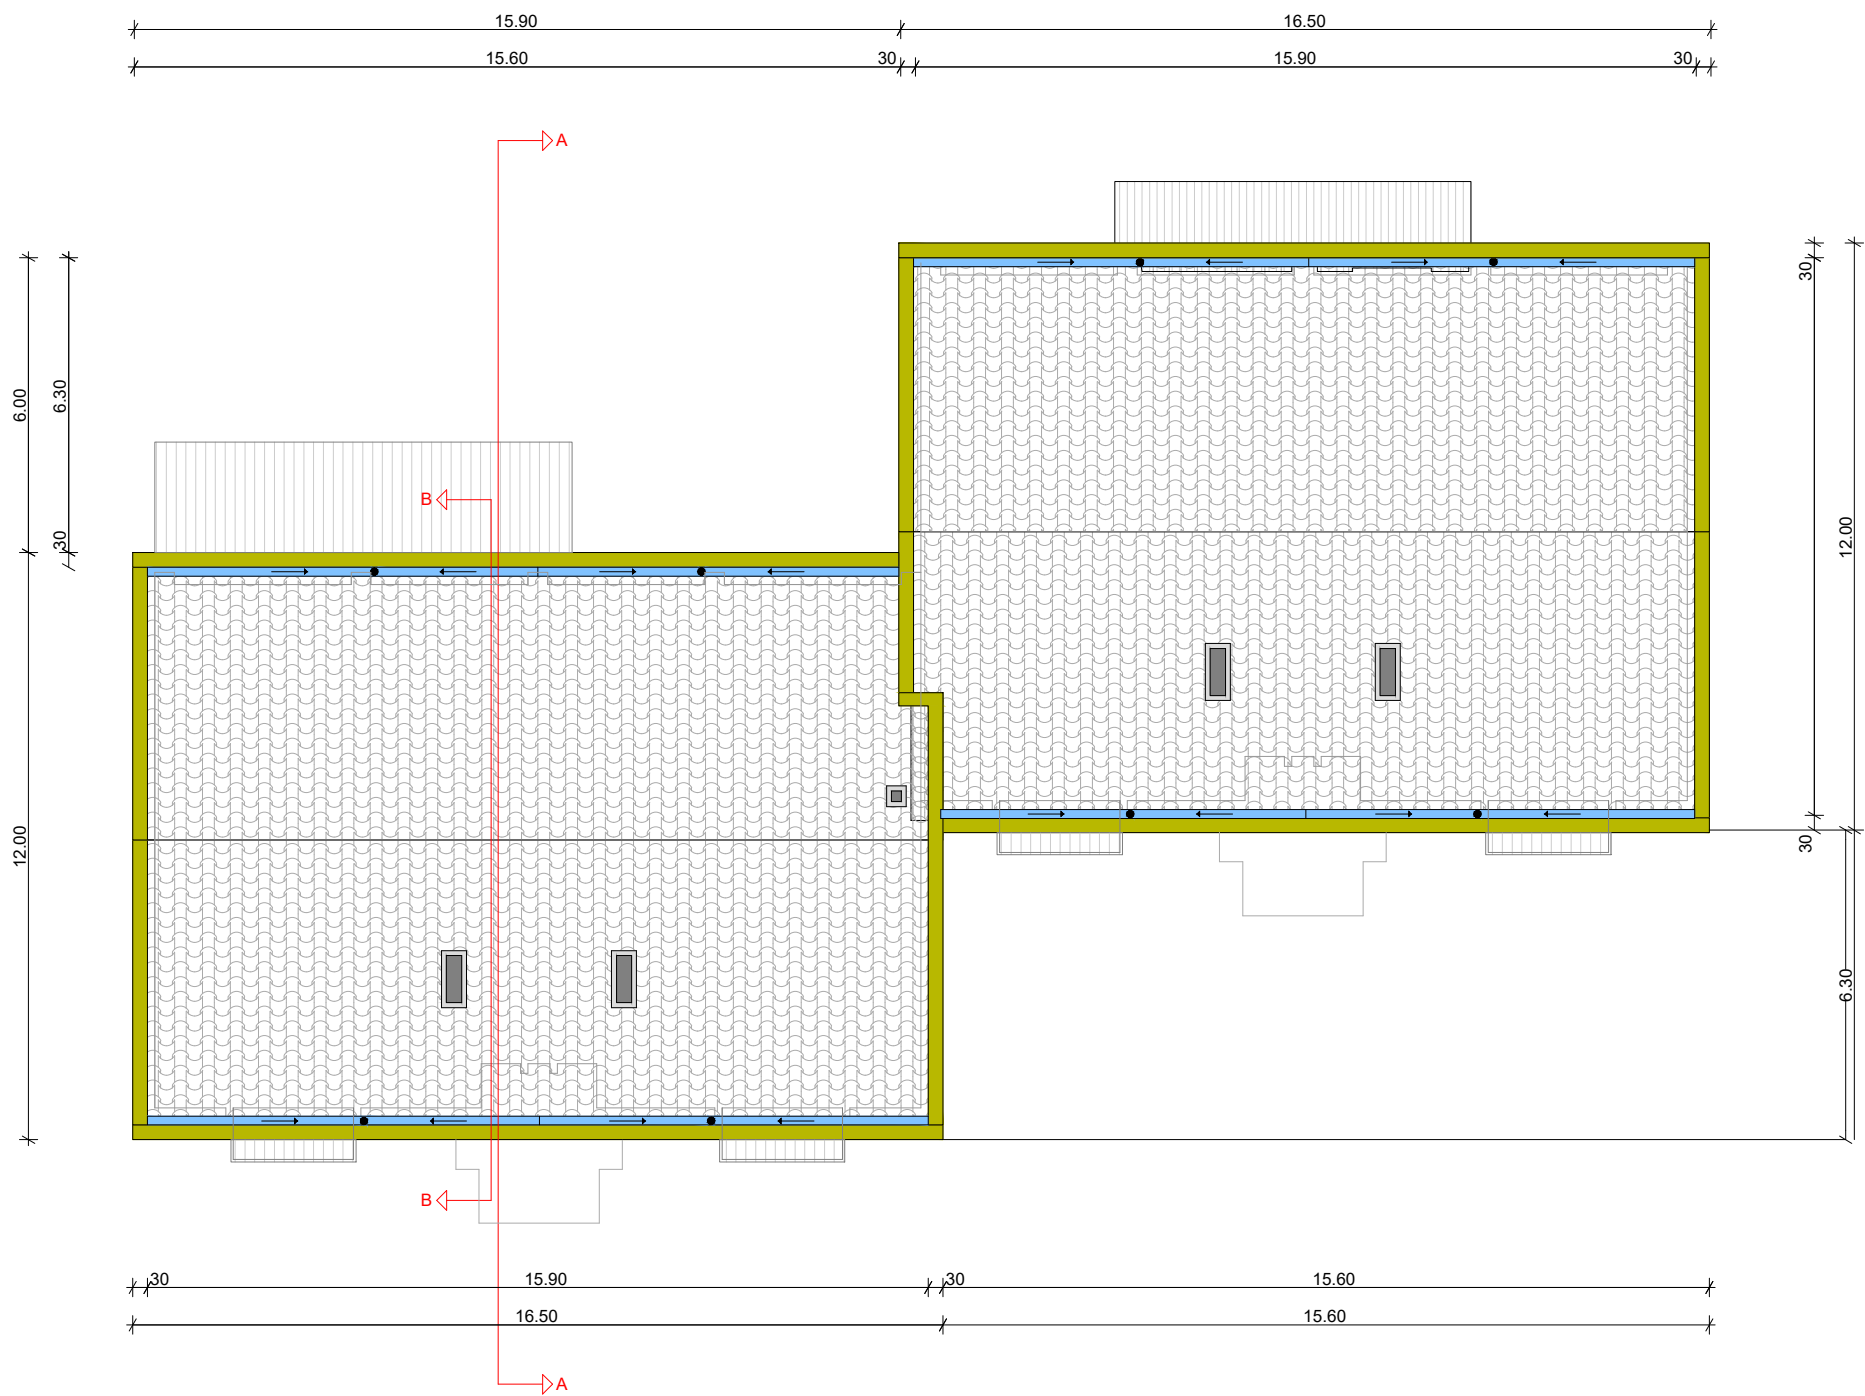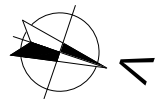


Përshkrimi i renovimit

- Renovimi dhe termoizolimi i kulmit me EPS t=16cm
- Ndërrimi i ulluqeve horizontale
- Ndërrimi i ulluqeve vertikale
- Ndërrimi i pikores

 REPUBLIKA E KOSOVËS / REPUBLIC OF KOSOVO Fondi i Kosovës për Eficiencë të Energjisë Kosovo Energy Efficiency Fund	
Projekti: Angazhimi i Kompanive për kryerje të punëve ndërtimore për implementimin e masave të Eficiencës së Energjisë në ndërtesat shumë banesore sociale	
Nr. Prokurimit : VET-FKEE2020-24-1699-S-1-1/C70 LOT 5	
Kompania punëkryese:  ATC COM SHPK & DATING SHPK nnpattccom@gmail.com	
Emri i ndërtesës: Ndërtesa shumë-banesore sociale II_15, Klinë - Lot 5	
Faza e projektimit: Arkitektura	
Emri i vizatimit: Kulmi	
Punuar nga: BSc Liridon Sejdiu	Kontrolluar nga: IDA. Njomza Hoti
Date: 08/2025	Rishikim:
Shkalla e zvogëlimit: P=1:100	Nr. i faqes: 05

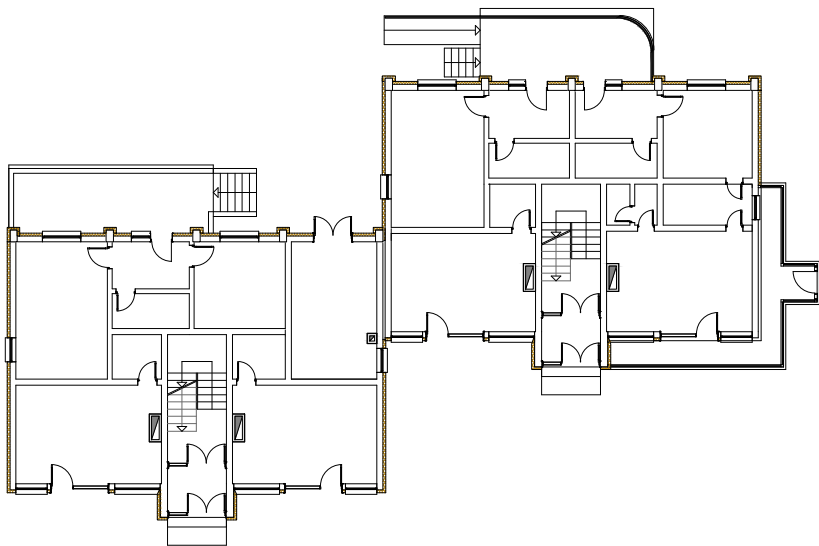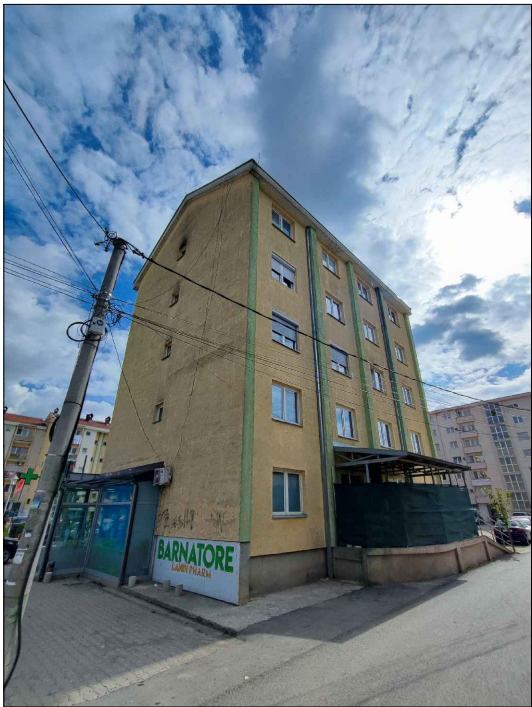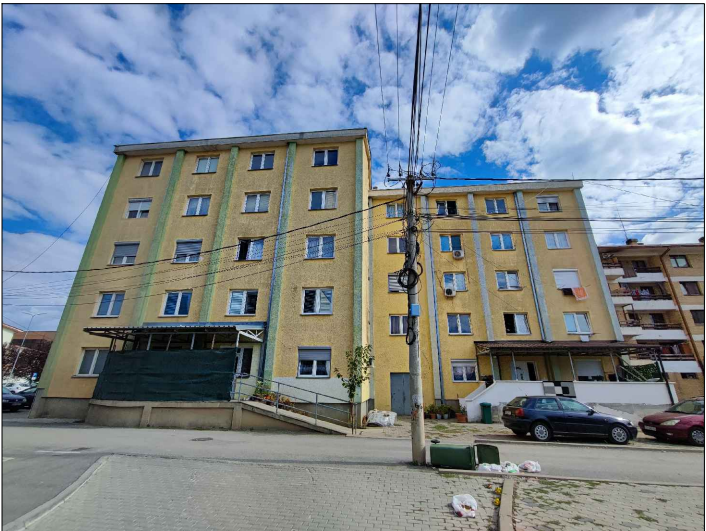

 FKEE FOND I KOSOVËS PËR EFICIENCË TË ENERGJISË KOSOVO ENERGY EFFICIENCY FUND REPUBLIKA E KOSOVËS / REPUBLIC OF KOSOVO Fondi i Kosovës për Eficiencë të Energjisë Kosovo Energy Efficiency Fund	
Projekti: Angazhimi i Kompanive për kryerje të punëve ndërtimore për implementimin e masave të Eficiencës së Energjisë në ndërtesat shumë banesore sociale	
Nr. Prokurimit : VET-FKEE2020-24-1699-5-1-1/C70 LOT 5	
Kompania punekryese:  ATC COM ALL TYPES OF CONSTRUCTION ATC COM SHPK & DAJTING SHPK nnpatccom@gmail.com	
Emri i ndërtesës: Ndërtesa shumë-banesore sociale II_15, Klinë - Lot 5	
Faza e projektimit: Arkitektura	
Emri i vizatimit: Fotot e ndërtesës	
Punuar nga: BSc Liridon Sejdiu	Kontrolluar nga: IDA. Njomza Hoti
Datë: 08/2025	Rishikim:
Shkalla e zvogëlimit:	Nr. i faqes: 06

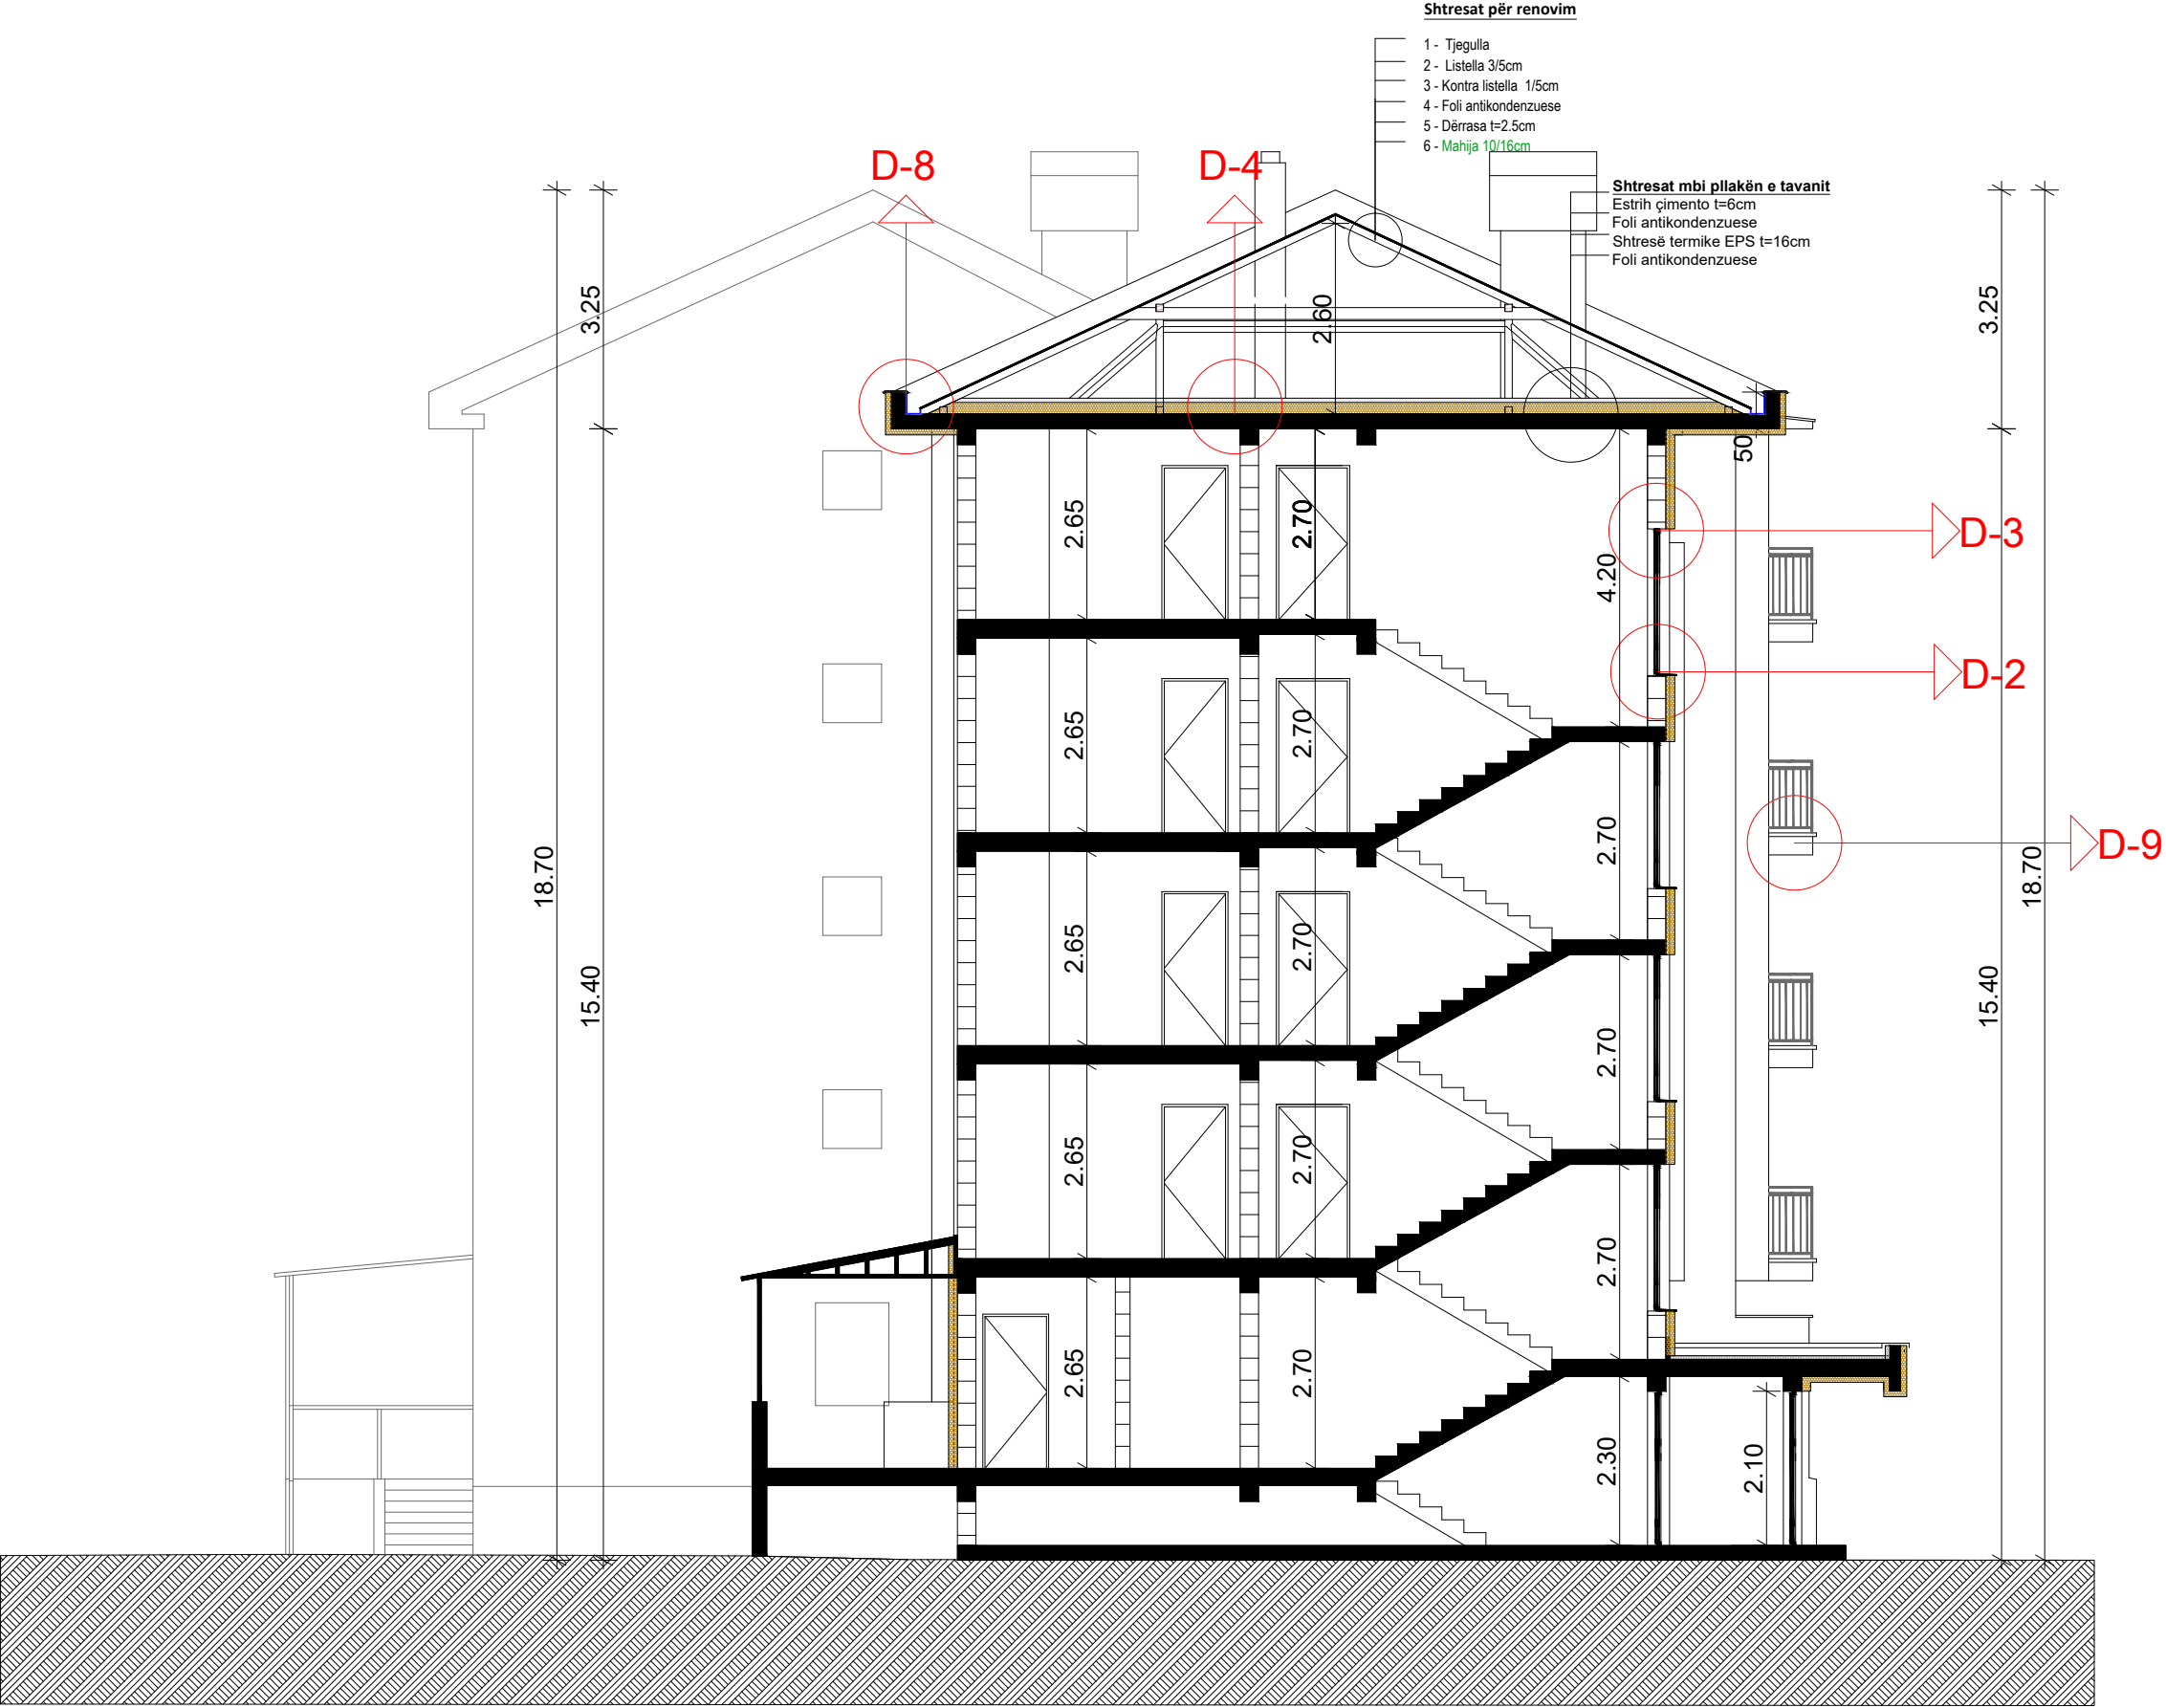



REPUBLIKA E KOSOVËS / REPUBLIC OF KOSOVO
Fondi i Kosovës për Eficiencë të Energjisë
Kosovo Energy Efficiency Fund

Projekti:

Angazhimi i Kompanive për kryerje të punëve ndërtimore për implementimin e masave të Eficiencës së Energjisë në ndërtesat shumë banesore sociale

Nr. Prokurimit : VET-FKEE2020-24-1699-5-1-1/C70 LOT 5

Kompania punëkryese:



ATC COM SHPK & DAJTING SHPK
nnpatccom@gmail.com

Emri i ndërtesës:

Ndërtesa shumë-banesore sociale II_15,
Klinë - Lot 5


Faza e projektimit:

Arkitektura

Emri i vizatimit:

Prerja A-A

Punuar nga:	Kontrolluar nga:
BSc Liridon Sejdiu	IDA. Njomza Hoti
Datë:	Rishikim:
08/2025	
Shkalla e zvogëlimit:	Nr. i faqes:
P=1:100	07

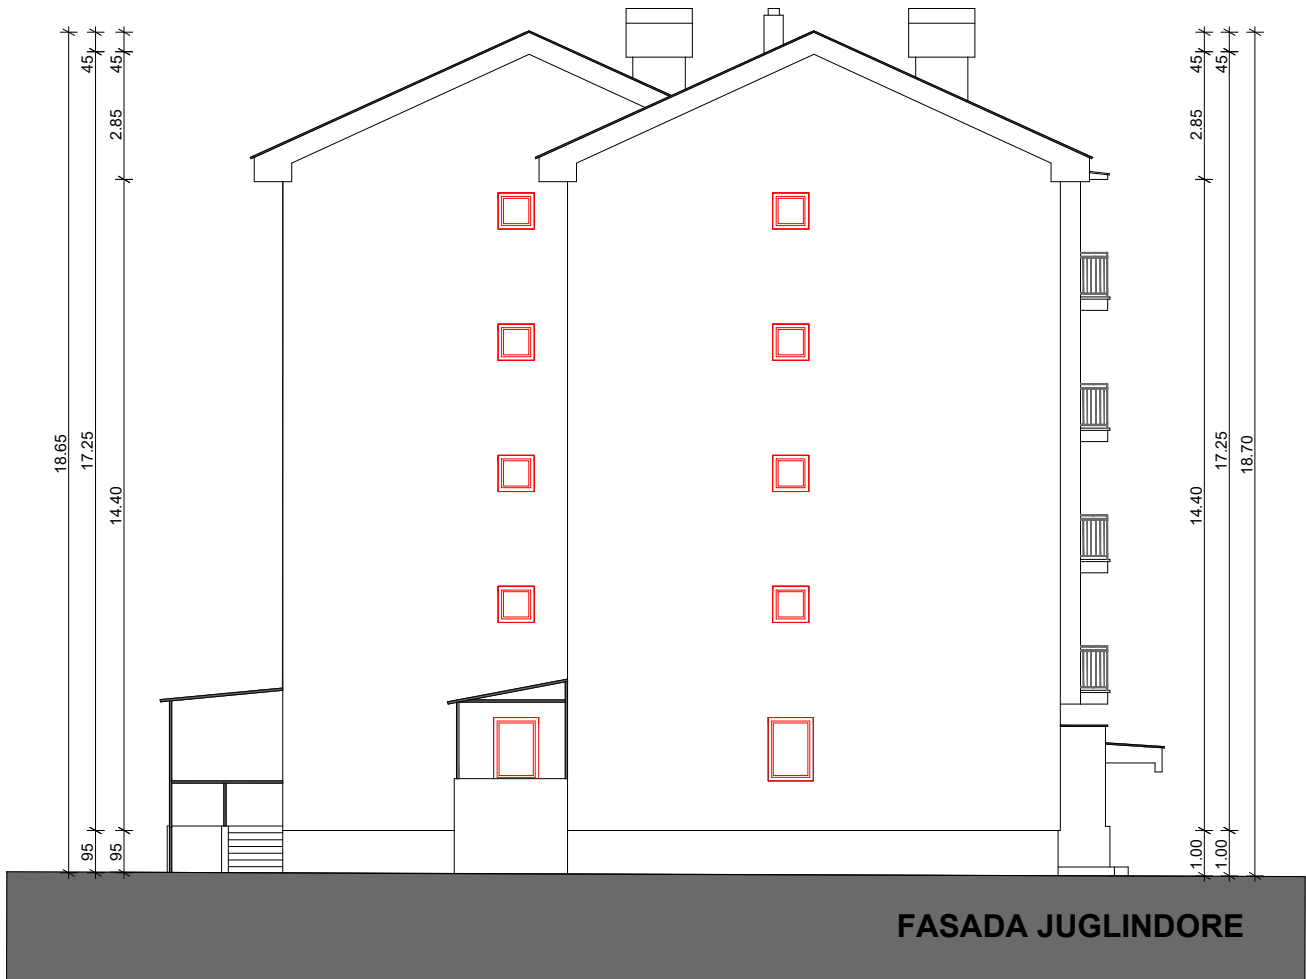

Përshkrimi renovimit

- ==== Ndërrimi i dritareve
- ==== Ndërrimi i dyerve
- ==== Dyer/dritare të reja



REPUBLIKA E KOSOVËS / REPUBLIC OF KOSOVO
Fondi i Kosovës për Eficiencë të Energjisë
Kosovo Energy Efficiency Fund

Projekti:
Angazhimi i Kompanive për kryerje të punëve ndërtimore për implementimin e masave të Eficiencës së Energjisë në ndërtesat shumë banesore sociale

Nr. Prokurimit : VET-FKEE2020-24-1699-S-1-1/C70 LOT 5



ATC COM SHPK & DAJTING SHPK

Emri i ndërtuesit:
Ndërtesa shumë-banesore sociale II_15, Klinë - Lot 5

Faza e projektimit:
Arkitektura

Emri i vizatimit:
Fasada Veriore & Lindore

Punuar nga:
BSc Liridon Sejdiu

Kontrolluar nga:
IDA. Njomza Hoti


Data:
08/2025

Rashikim:

Shkalla e zvogëlitimit:
P=1:100

Nr. / faqes:
08

650x500mm

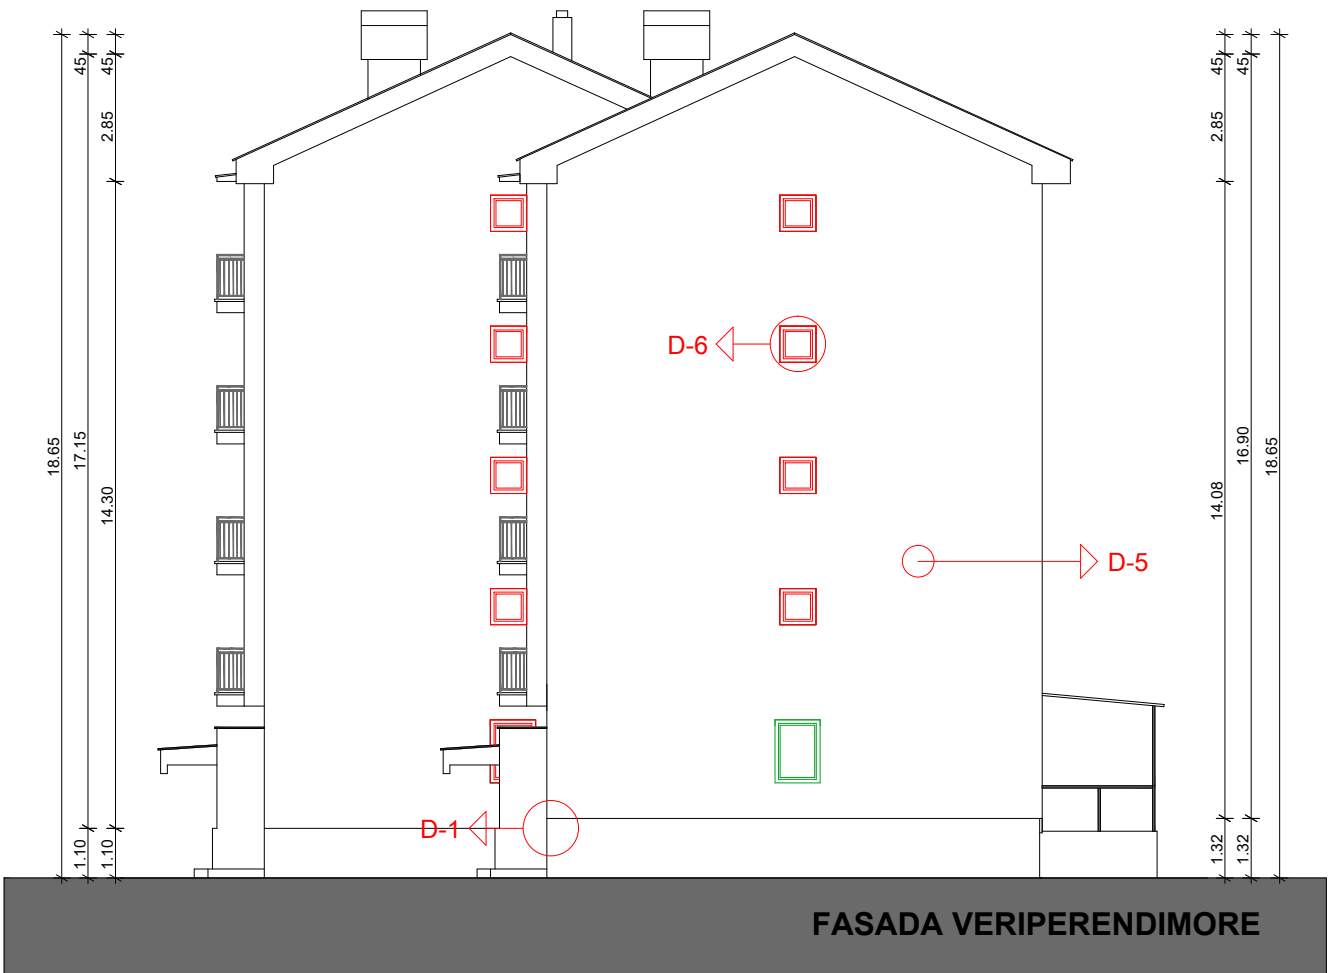

- Përshkrimi renovimit**
- Ndërrimi i dritareve
 - Ndërrimi i dyerve
 - Dyer/dritare të reja
 - Ngjyrosje dhe renovimi i derës ekzistuese

FKEE
FOND I KOSOVËS PËR EFICIENCËN E ENERGJISË
Kosovo Energy Efficiency Fund

Projekti:
Angazhimi i Kompanive për kryerje të punëve ndërtimore për implementimin e masave të Eficiencës së Energjisë në ndërtesat shumë banesore sociale

Nr. Prokurimit : VET-FKEE2020-24-1699-S-1-1/C70 LOT 5

Kompania punëkryese:

ATC ALL TYPES OF CONSTRUCTION CO. LTD.
ATC COM SHPK & DAIJING SHPK
nmpatcom@gmail.com

Emri i ndërtesës:
Ndërtesa shumë-banesore sociale II_15, Klinë - Lot 5

Faza e projektimit:
Arkitektura

Emri i vizatimit:
Fasada Jugore & Perëndimore

Punuar nga:
BSc Liridon Sejdiu

Kontrolluar nga:
IDA. Njomza Hoti

Dati:
08/2025

Rishikim:

Shkalla e zvogëlitimit:
P=1:100

Nr. / faqes:
09



FASADA VERILINDORE



FASADA JUGLINDORE



FASADA JUGPERENDIMORE



FASADA VERIPERENDIMORE

Vërejtje: Masat mbrojtëse kundër zjarrit duhet të instalohen në tërë perimetrin e ndërtesës, si unazë me lesh guri dhe lartësi h=60cm sipas paraqitjeve grafike

Përshkrimi renovimit

 Termoizolimi i mureve me Lesh Guri t=12cm

 REPUBLIKA E KOSOVËS / REPUBLIC OF KOSOVO Fondi i Kosovës për Eficiencë të Energjisë Kosovo Energy Efficiency Fund	
Projekti: Angazhimi i Kompanive për kryerje të punëve ndërtimore për implementimin e masave të Eficiencës së Energjisë në ndërtesat shumë banesore sociale	
Nr. Prokurimit : VET-FKEE2020-24-1699-S-1-1/C70 LOT 5	
Kompania punëkryese:  ATC COM SHPK & DAJTING SHPK nnpatcom@gmail.com	
Emri i ndërtesës: Ndërtesa shumë-banesore sociale II_15, Klinë - Lot 5	
Faza e projektimit: Arkitektura	
Emri i vizatimit: Mbrojtja nga zjarri	
Punuar nga: BSc Liridon Sejdiu	Kontrolluar nga: IDA. Njomza Hoti
Data: 08/2025	Rishikim:
Shkalla e zvogëlimit: P=1:50	Nr. i faqes: 10

SKEMAT E DRITAREVE					
Pos_W-1		Pos_W-2		Pos_W-3	
Pos_W-5		Pos_W-5a			
Pozicioni: W-1, dim. 1.00x1.40m	Sasia: 2	Pozicioni: W-2, dim. 1.60x1.40m	Sasia: 36	Pozicioni: W-3, dim. 0.80x1.40m	Sasia: 3
Pozicioni: W-5, dim. 1.60x1.40m		Pozicioni: W-5a, dim. 0.80x2.30m		Sasia: 16	

SKEMAT E DRITAREVE					
Pos_W-6		Pos_W-7		Pos_W8	
Pos_W9					
Pozicioni: W-6, dim. 0.80x0.80m	Sasia: 32	Pozicioni: W-7, dim. 0.70x2.00m	Sasia: 16	Pozicioni: W-8, dim. 1.90x2.90m	Sasia: 3
Pozicioni: W-9, dim. 1.30x2.90m				Sasia: 3	

SKEMA E DYERVE TË JASHTME					
Pos_D-1		Pos_D-2		Pos_D-3	
Pos_D-4					
Pozicioni: D-1, dim.2.50x2.10m	Sasia: 4	Pozicioni: D-2, dim.1.00x2.10m	Sasia: 20	Pozicioni: D-3, dim.1.60x2.50m	Sasia: 1
Pozicioni: D-4, dim.2.40x3.50m				Sasia: 3	



REPUBLIKA E KOSOVËS / REPUBLIC OF KOSOVO
Fondi i Kosovës për Eficiencë të Energjisë
Kosovo Energy Efficiency Fund

Projekti:
Angazhimi i Kompanive për kryerje të punëve ndërtimore për implementimin e masave të Eficiencës së Energjisë në ndërtesat shumë banesore sociale

Nr. Prokurimit: VET-FKEE2020-24-1699-S-1-1/C70 LOT 5



ATC COM SHPK & DAITING SHPK
mnpattcom@gmail.com

Emri i ndërtuesit:
Ndërtesa shumë-banesore sociale II_15, Klinë - Lot 5

Faza e projektimit:
Arkitektura

Emri i vizatimit:
Skemat e dyerve dhe dritareve

Punuar nga:
BSc Liridon Sejdiu

Kontrolluar nga:
IDA. Njomza Hoti

Data:
08/2025

Rishikim:

Shkalla e zvogëlimit:
P=1:50

Nr. i faqes:
11