
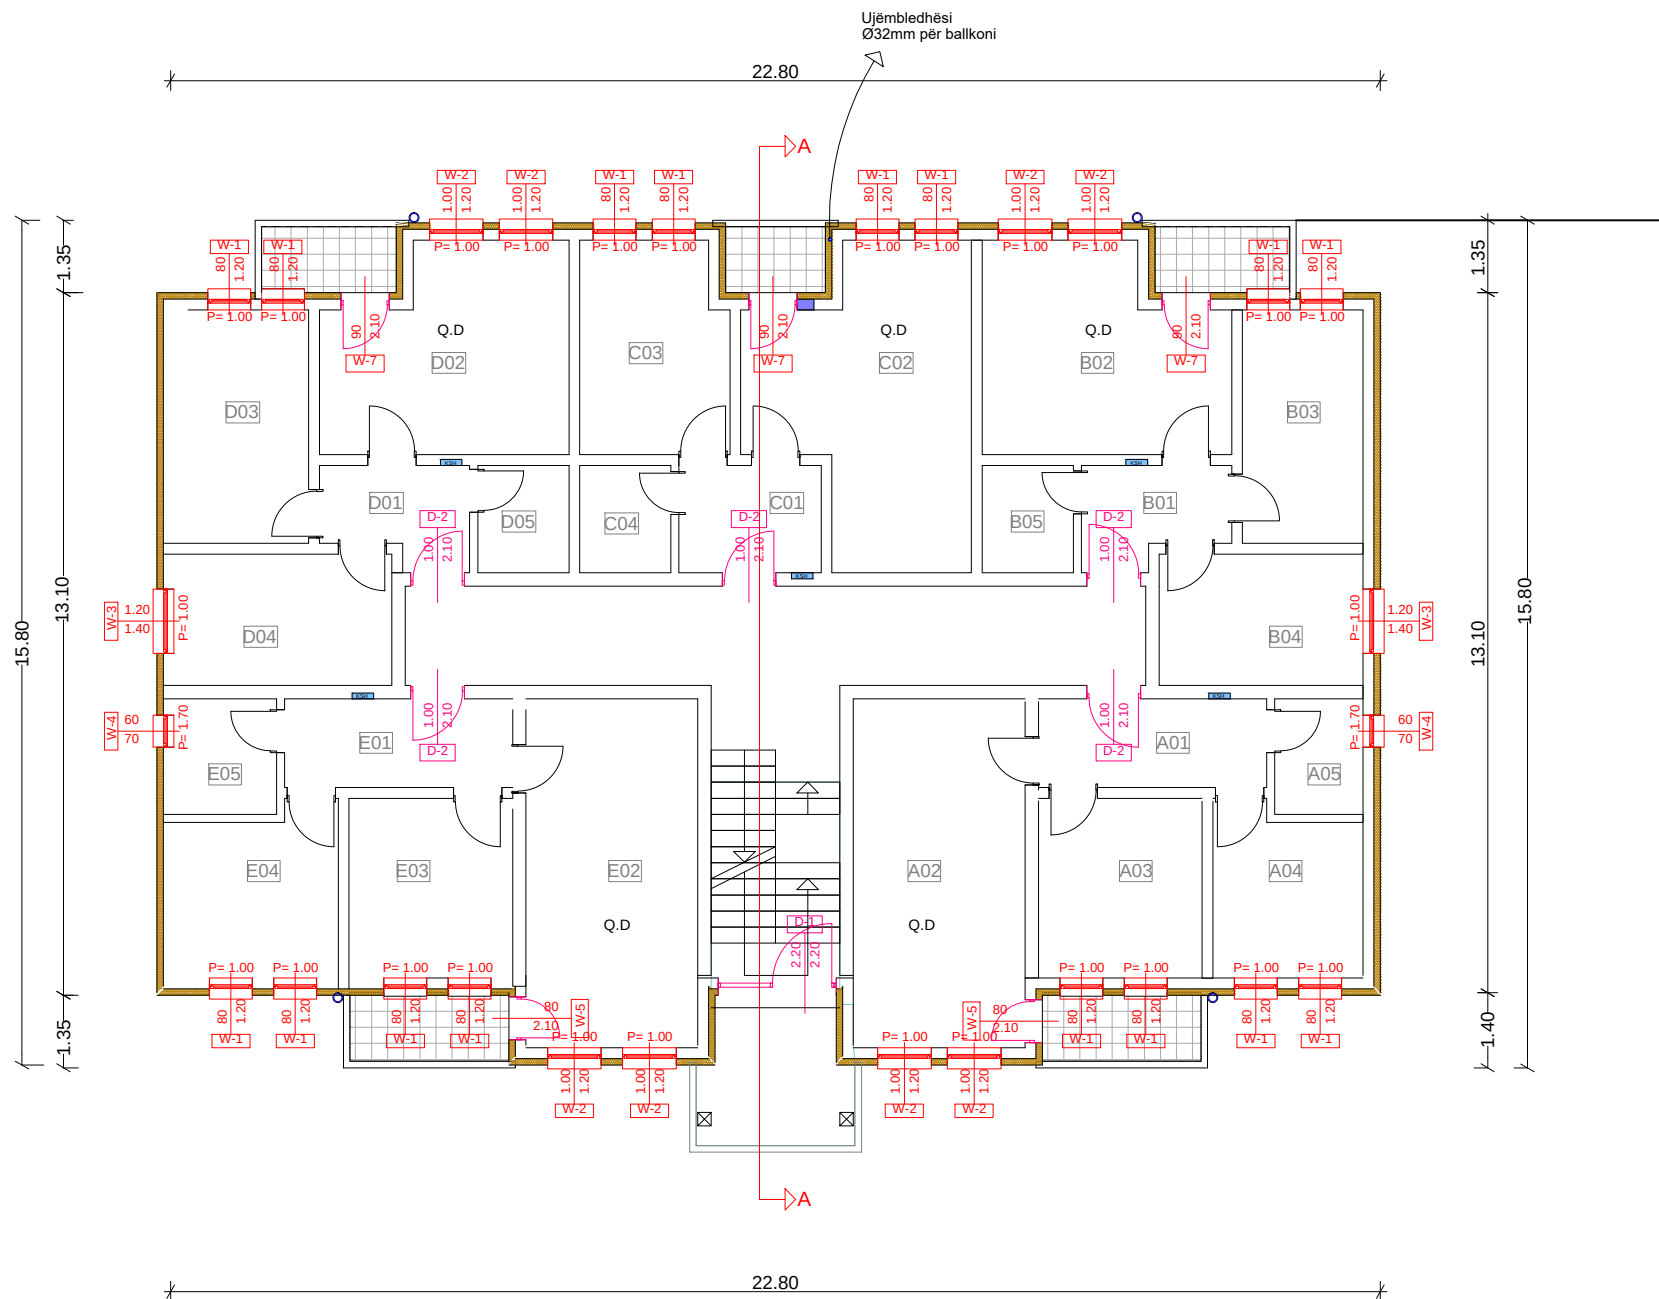


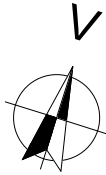

Përshkrimi renovimit

- Termoizolimi i mureve me EPS t=12cm
- Ndërrimi i dritareve
- Ndërrimi i detyrë
- Muratim

 REPUBLIKA E KOSOVËS / REPUBLIC OF KOSOVO Fondi i Kosovës për Eficiencë të Energjisë Kosovo Energy Efficiency Fund	
Projekti: Angazhimi i Kompanive për kryerje të punëve ndërtimore për implementimin e masave të Eficiencës së Energjisë në ndërtesat shumë banesore sociale	
Nr. Prokurimit : VET-FKEE2020-24-1699-S-1-UC70 LOT 5 Kompania punëkryesë  ALL TYPES OF CONSTRUCTION CO. LTD. ATC COM SHPK & DATING SHPK nnpstccom@gmail.com	
Emri i ndërtesës: Ndertesa shume banesor Social I, Klinë	
Faza e projektimit: Arkitektura	
Emri i vizatimit: Përdhesa	
Punuar nga: BSc Liridon Sejdiu	Kontrolluar nga: IDA. Njoma Hoti
Date: 08/2025	Rishikim:
Shkalla e zvogëlimit: P=1:100	Nr. i faqes: 02