



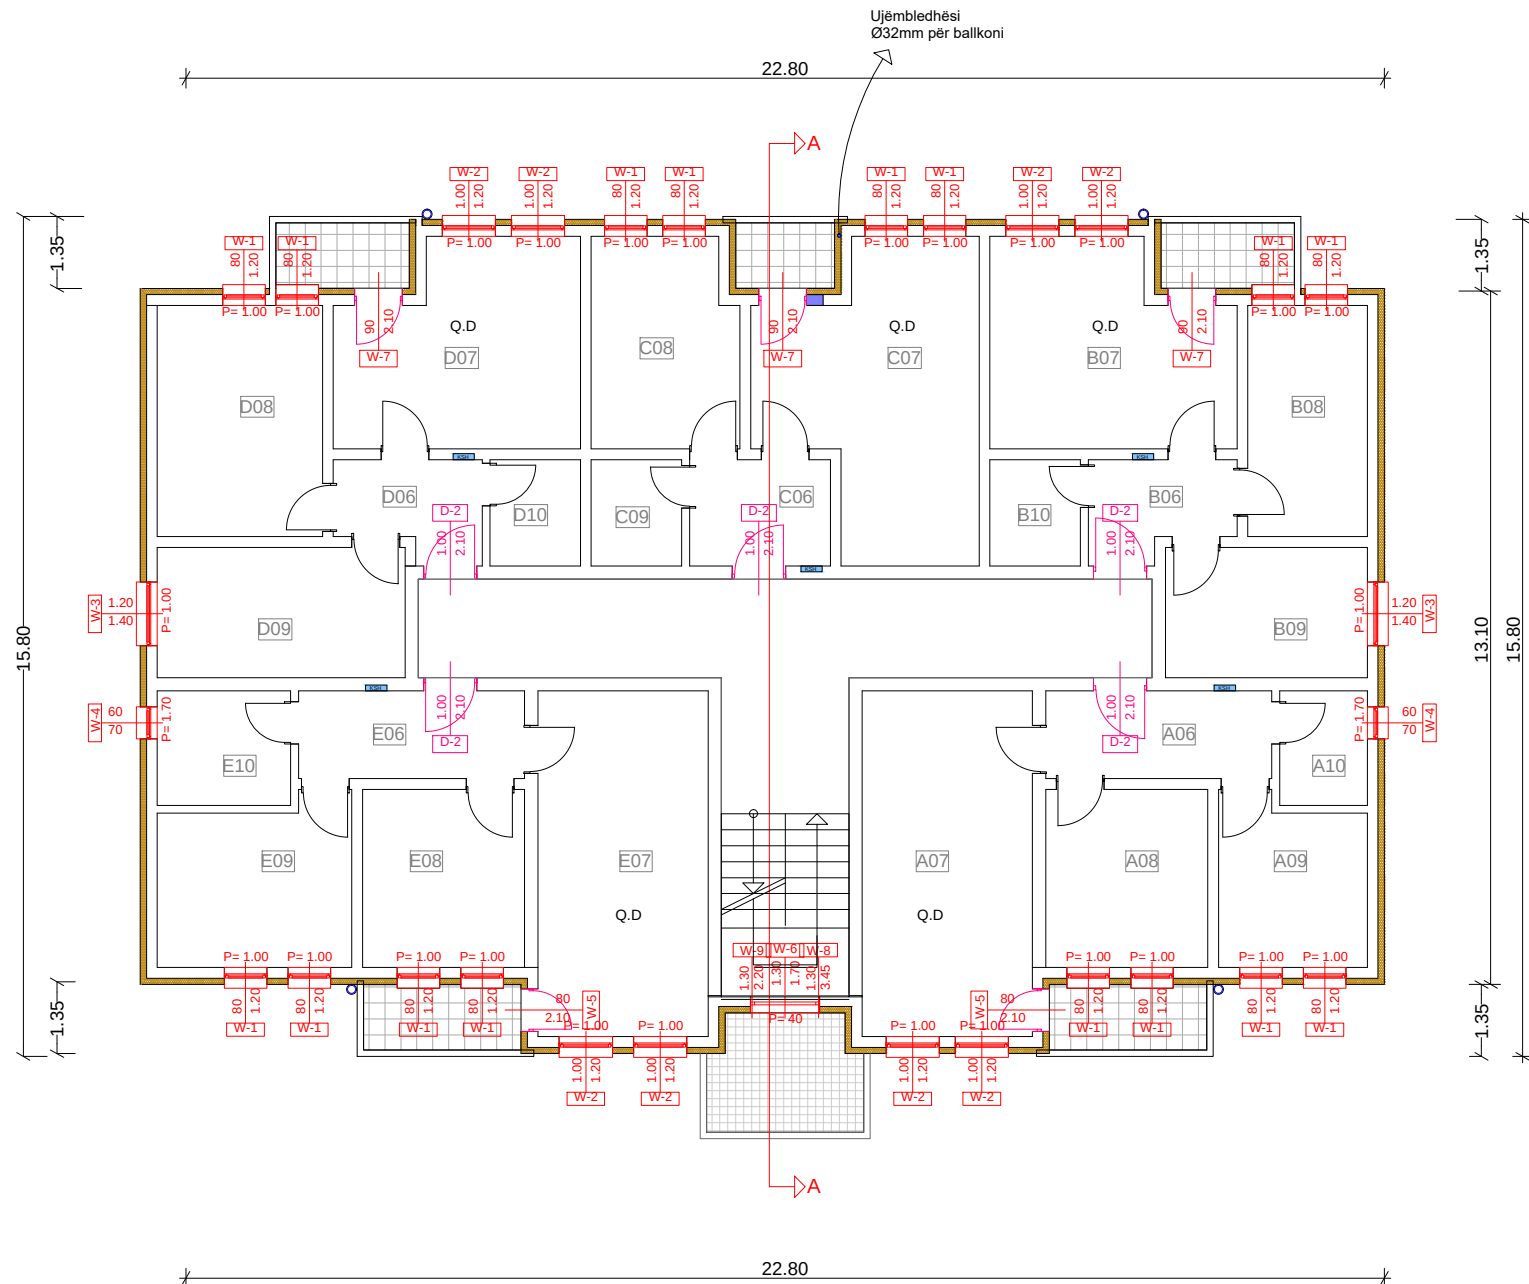

Përshkrimi renovimit

- Termoizolimi i mureve me EPS t=12cm
- Ndërrimi i dritareve
- Ndërrimi i dyerve
- Renovimi i strehes te hryja
- Mur i ri

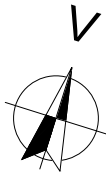

REPUBLIKA E KOSOVËS / REPUBLIC OF KOSOVO
Fondi i Kosovës për Eficiencë të Energjisë
Kosovo Energy Efficiency Fund

Projekti:
Angazhimi i Kompanive për kryerje të punëve ndërtimore për implementimin e masave të Eficiencës së Energjisë në ndërtesat shumë banesore sociale

Nr. Prokurimit : VET-FKEE2020-24-1699-S-1-UC70 LOT 5

Kompania punëkryese



ALL TYPES OF CONSTRUCTION

ATC COM SHPK & DAITING SHPK
nnpstccom@gmail.com

Emri i ndërtesës:
Ndertesa shume banesor Social I, Klinë

Faza e projektimit:
Arkitektura

Emri i vizatimit:
Kati I - IV

Punuar nga: BSc Liridon Sejdiu	Kontrolluar nga: IDA. Njomza Hoti
Date: 08/2025	Rishikim:
Shkalla e zvogëlimit: P=1:100	Nr. i faqes: 03