



 FKEE FOND I KOSOVËS PËR EFICIENCËN E ENERGJISË KOSOVO ENERGY EFFICIENCY FUND REPUBLIKA E KOSOVËS / REPUBLIC OF KOSOVO Fondi i Kosovës për Eficiencë të Energjisë Kosovo Energy Efficiency Fund	
Projekti: Angazhimi i Kompanive për kryerje të punëve ndërtimore për implementimin e masave të Eficiencës së Energjisë në ndërtesat shumë banesore sociale	
Nr. i kontratës: VET-FKEE2020-23-3696-2-1-1/C35_Lot 5	
Kompania punëkryese  ALL TYPES OF CONSTRUCTION ATC COM SHPK & DAIJING SHPK nnpatcom@gmail.com	
Emri i ndërtesës: Ndërtesa shumë-banesore sociale II_15, Klinë - Lot 5	
Faza e projektimit: Arkitektura	
Emri i vizatimit: Lokacioni i ndërtesës	
Punuar nga: BSc Liridon Sejdiu	Kontrolluar nga: IDA. Njomza Hoti
Datë: 08/2025	Rishikim:
Shkalla e zvogëlimit:	Nr. i faqes: 01

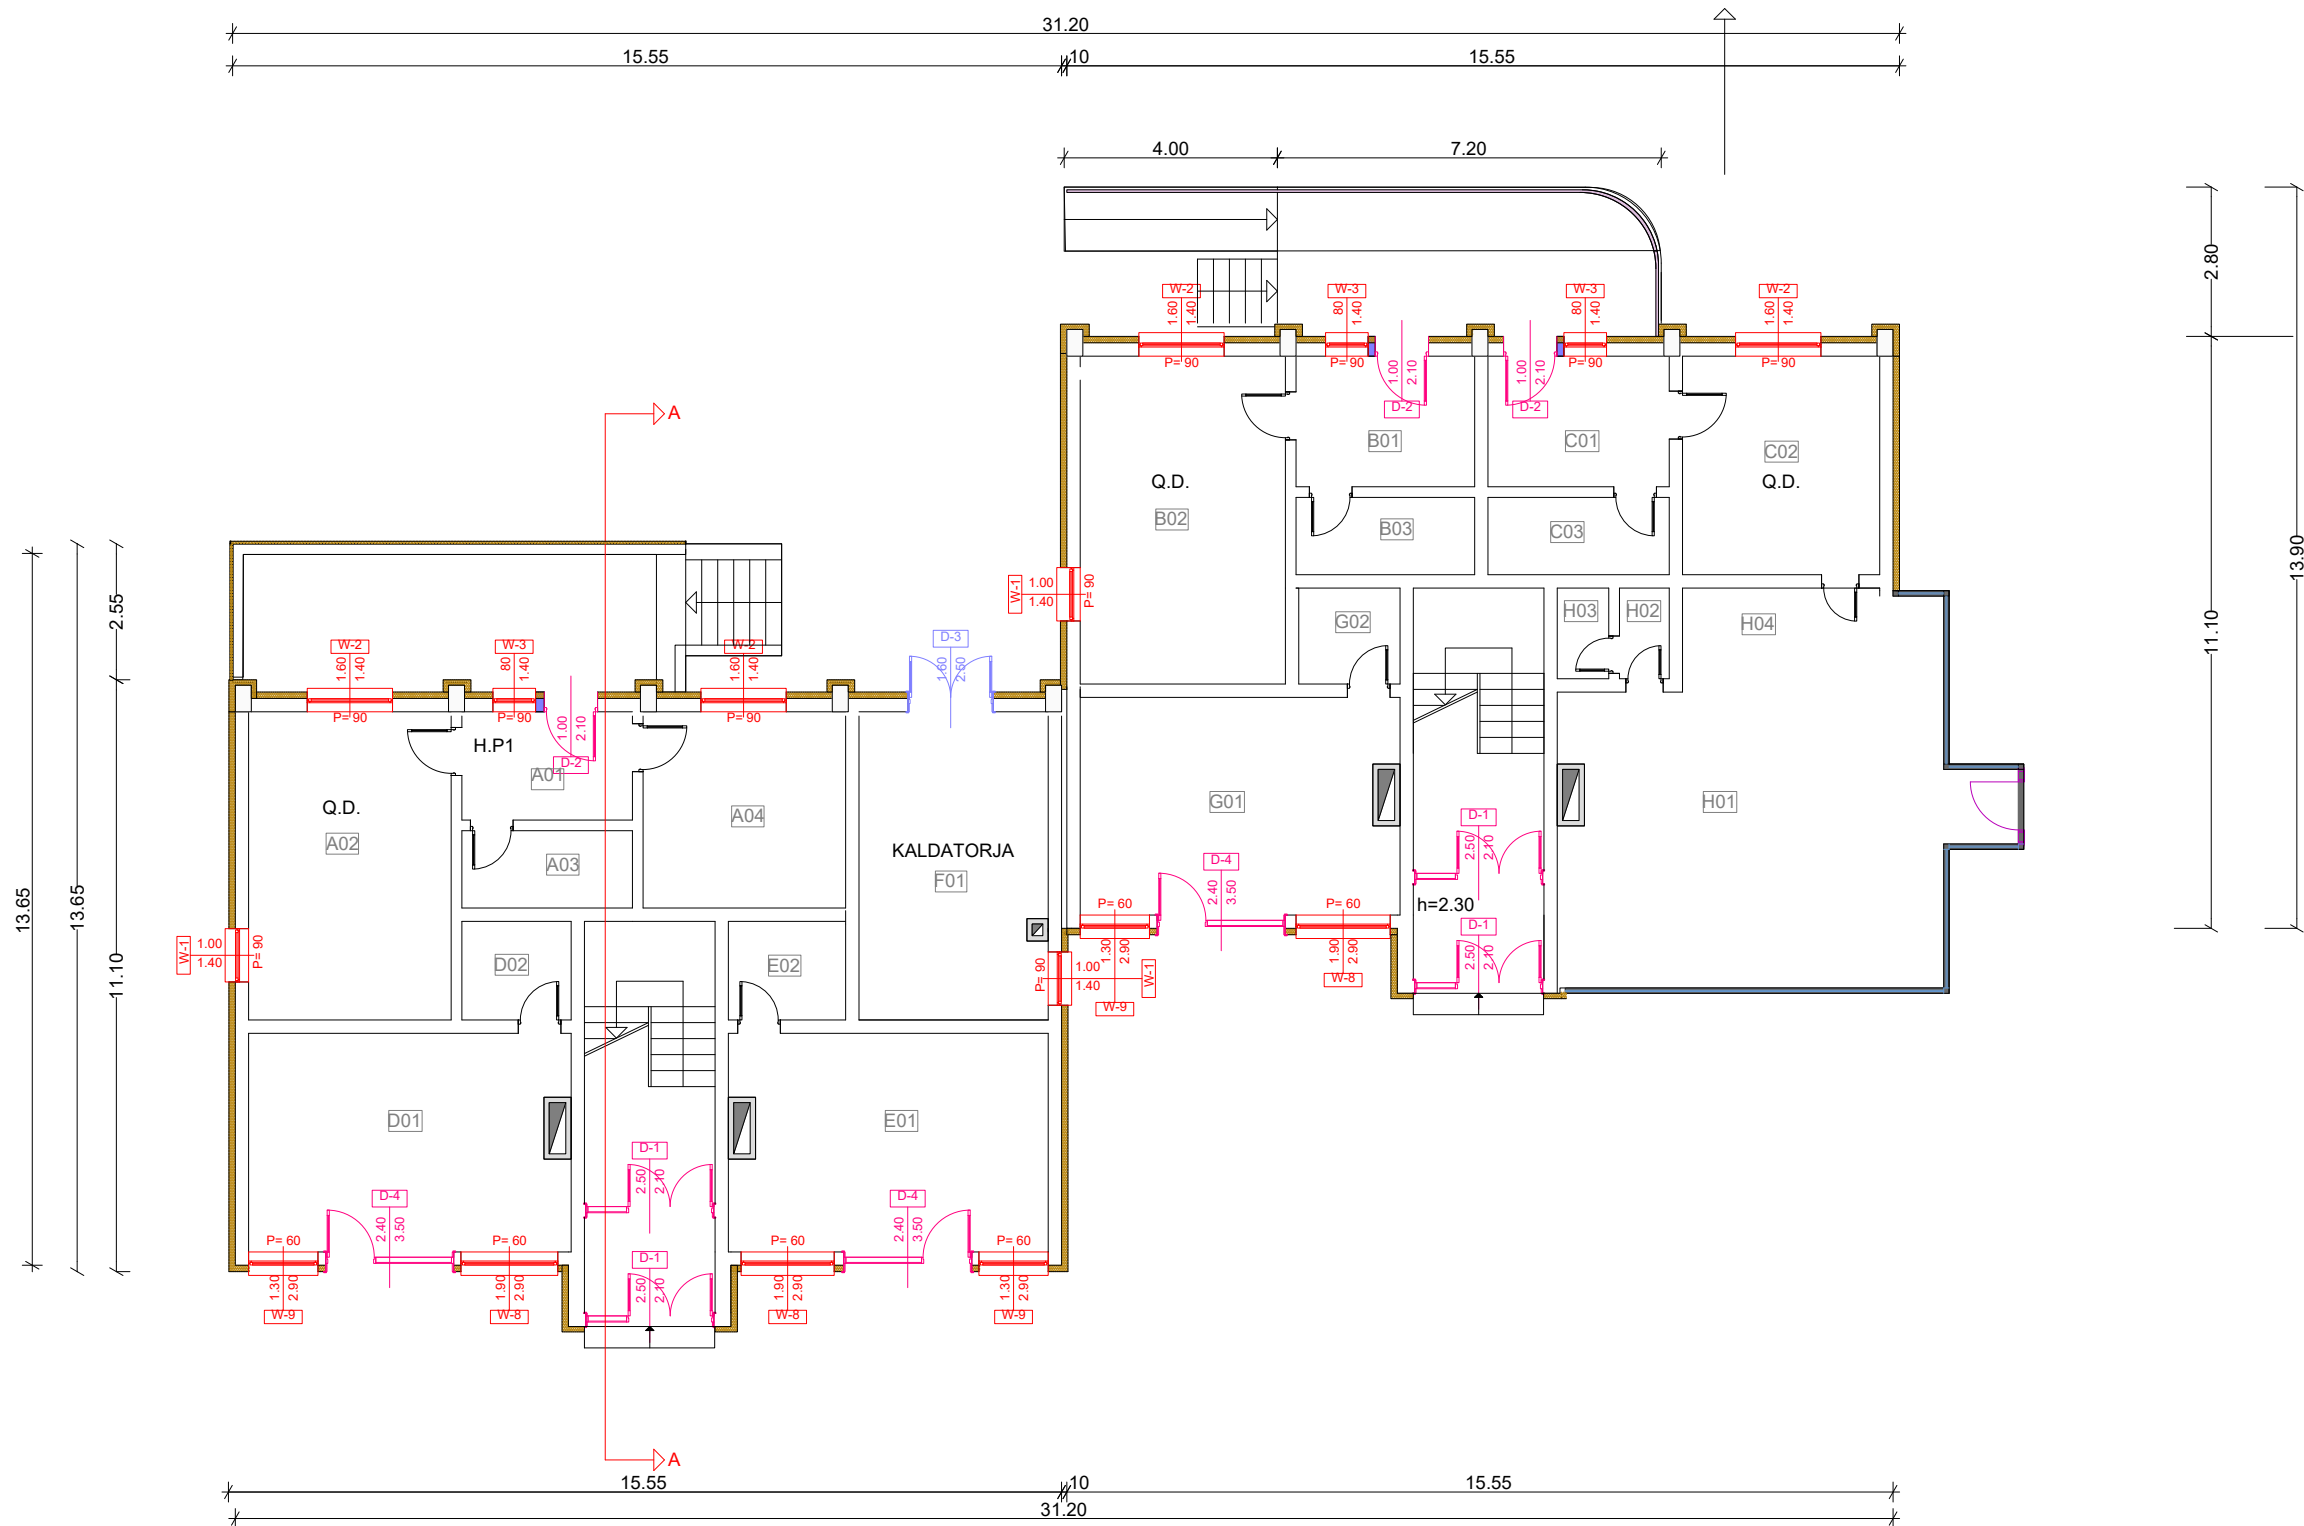

Përshkrimi renovimit

- Termoizolimi i mureve me EPS t=12cm
- Ndërrimi i dritareve
- Ndërrimi i dyerve
- Ngjyrose dhe renovimi i derës ekzistuese
- Muratim

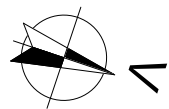

REPUBLIKA E KOSOVËS / REPUBLIC OF KOSOVO
Fondi i Kosovës për Eficiencë të Energjisë
Kosovo Energy Efficiency Fund

Projekti:

Angazhimi i Kompanie për kryerje të punëve ndërtimore për implementimin e masave të Eficiencës së Energjisë në ndërtesat shumë banesore sociale

Nr. Prokurimit : VET-FKEE2020-24-1699-S-1-1/C70 LOT 5

Kompania punëkryese:



ATC COM SHPK & DAITING SHPK
nnpatccom@gmail.com

Emri i ndërtesës:

**Ndërtesa shumë-banesore sociale II_15,
Klinë - Lot 5**

Faza e projektimit:

Arkitektura

Emri i vizatimit:

Përdhesa

Punuar nga:

BSc Liridon Sejdiu

Kontrolluar nga:

IDA. Njomza Hoti

Data:

08/2025


Rishikim:

Shkalla e zvogëlimit:

P=1:100


Nr. i faqes:

02

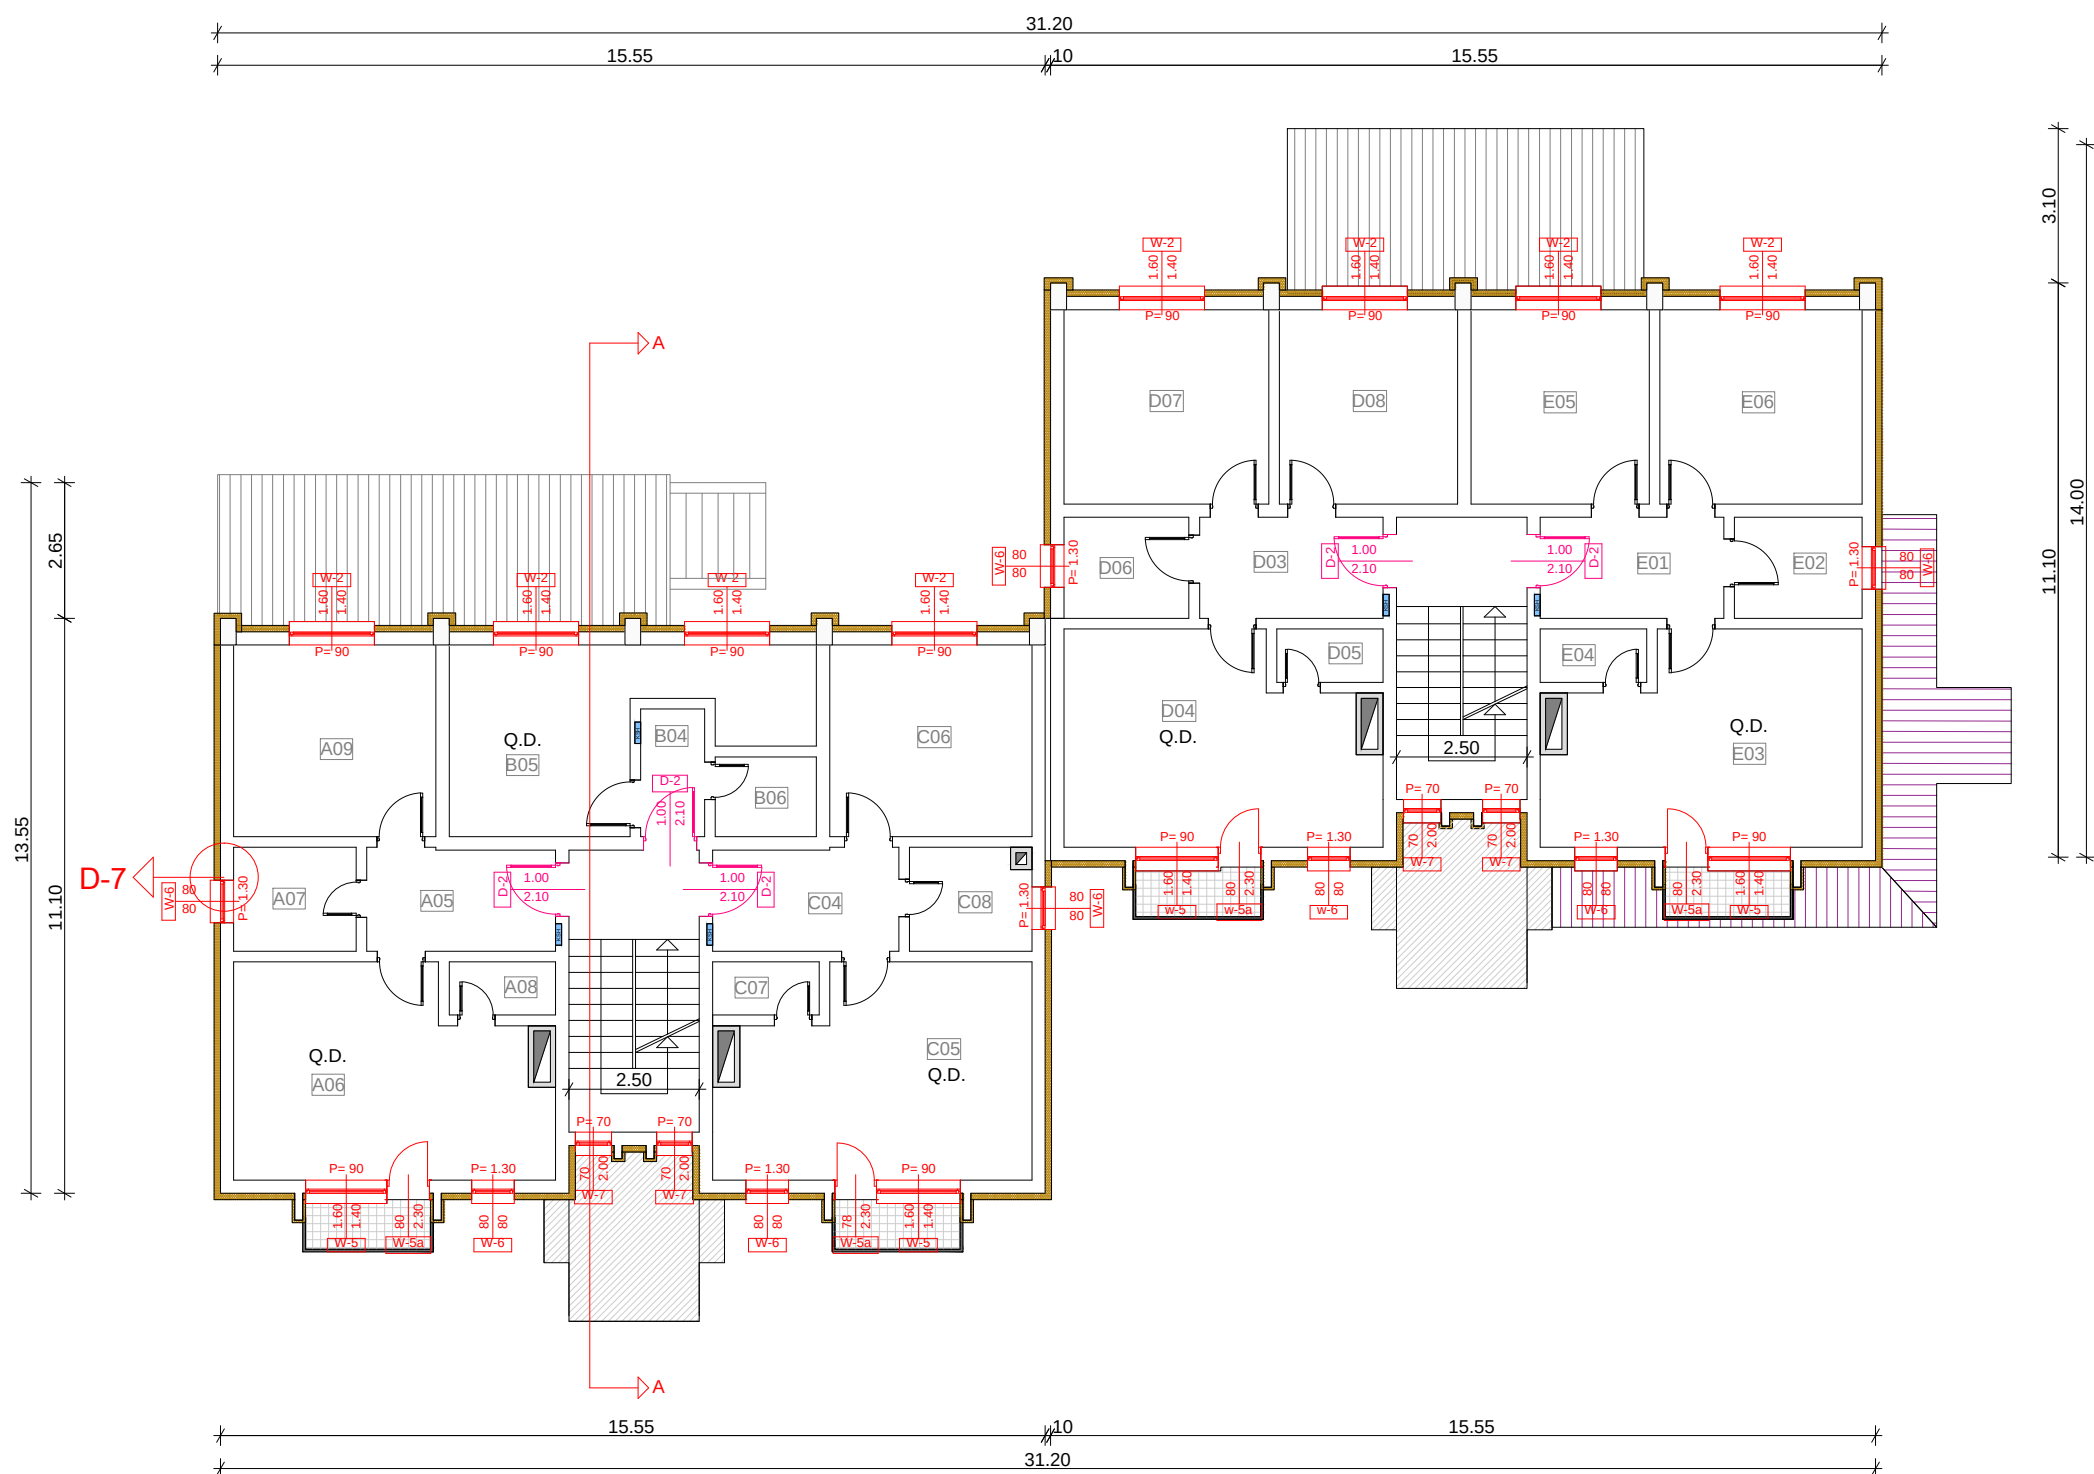



	Termoizolimi i mureve me EPS t=12cm
	Ndërrimi i dritareve
	Ndërrimi i dyerve
	Ndërrimi i llamarinës të kulmeve të anekseve
	Renovimi i strehës së hyrjes
	Renovimi i ballkoneve

600x420mm

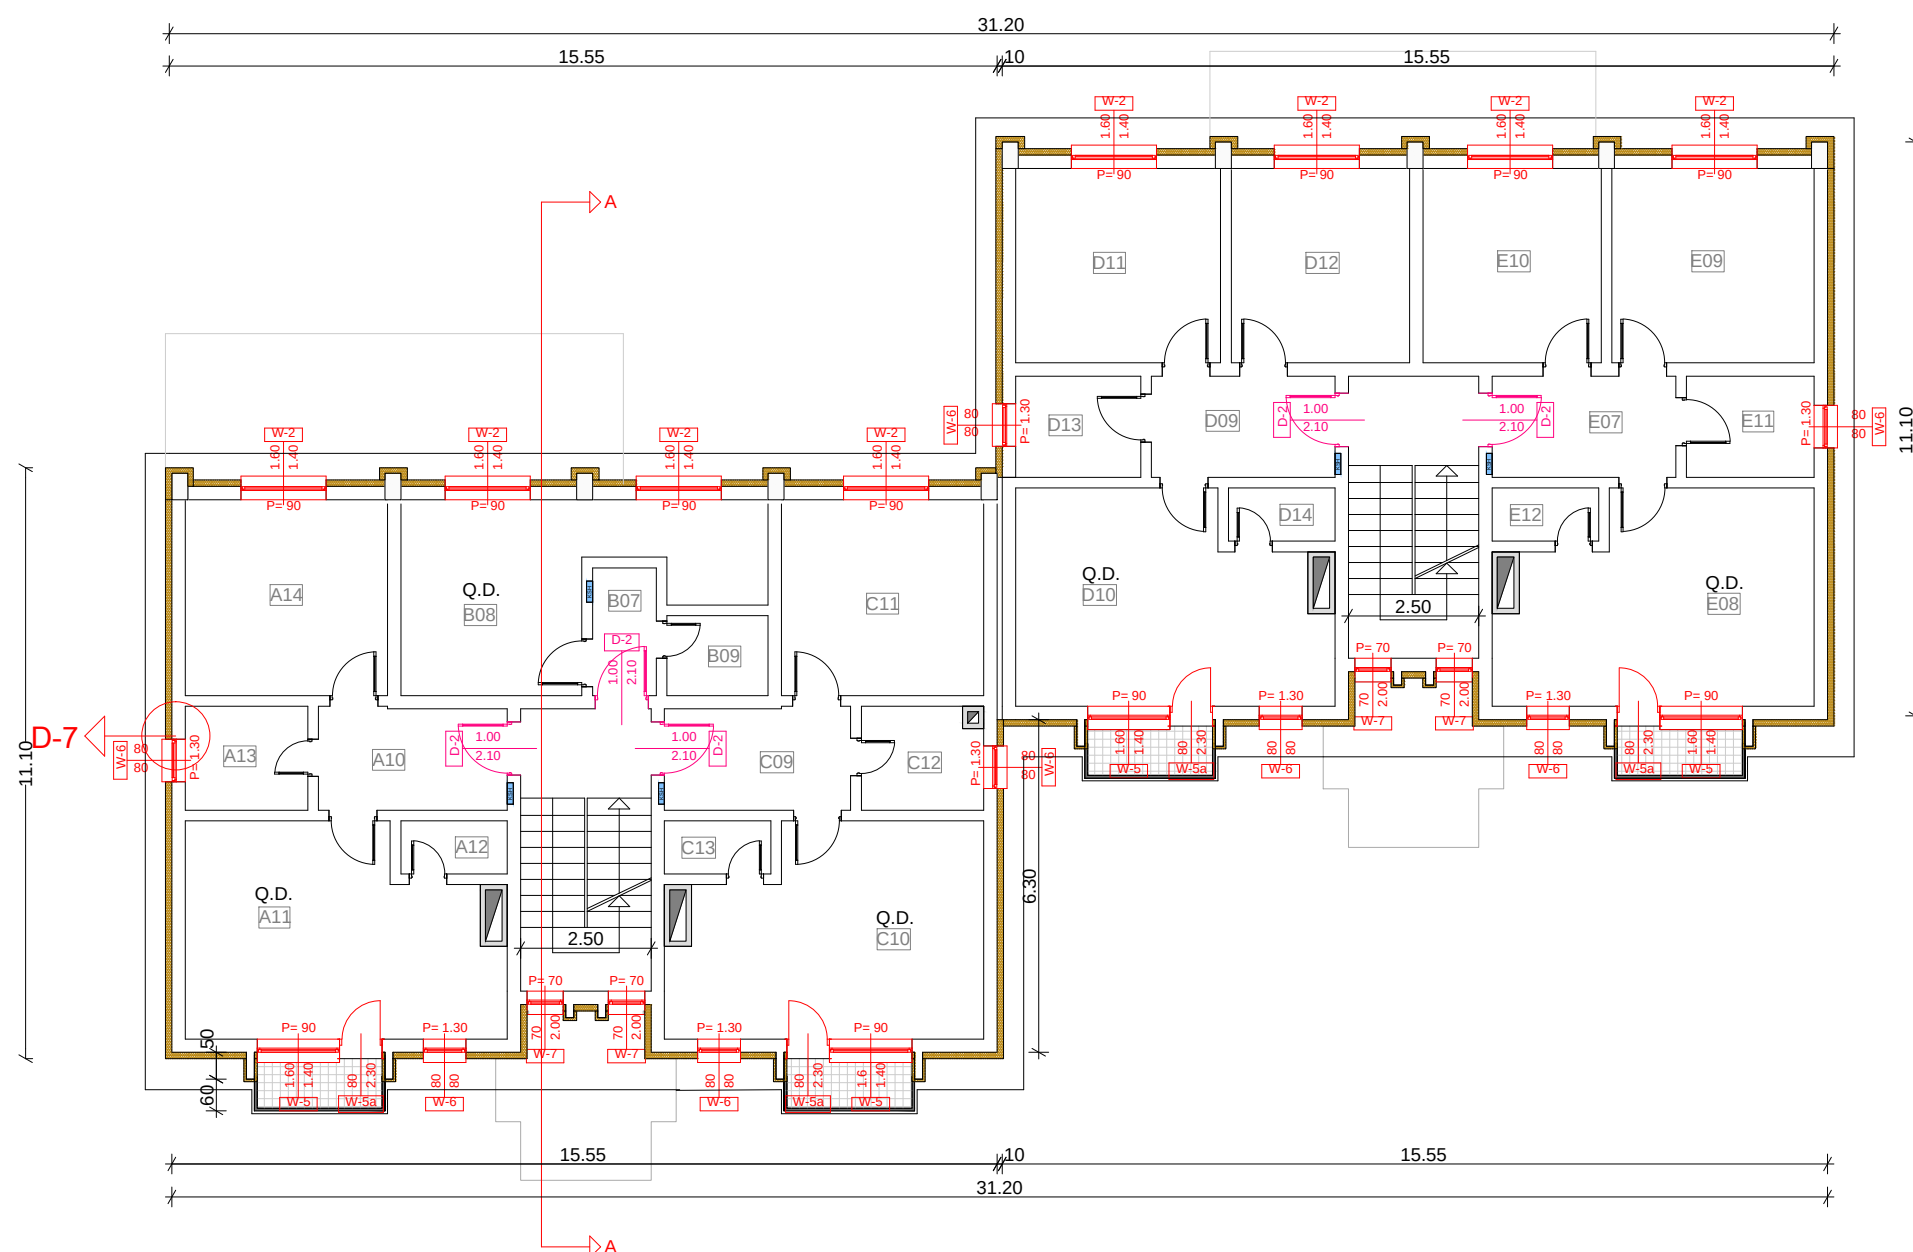

	Termoizolimi i mureve me EPS t=12cm
	Ndërrimi i dritareve
	Ndërrimi i dyerve
	Renovimi i ballkoneve

 <b style="font-size: 2em;">FKEE FUNDI I KOSOVËS PËR EFICIENCË TË ENERGJISË KOSOVO ENERGY EFFICIENCY FUND	
REPUBLIKA E KOSOVËS / REPUBLIC OF KOSOVO Fondi i Kosovës për Eficiencë të Energjisë Kosovo Energy Efficiency Fund	
Projekt: Angazhimi i Kompanisë për kryerje të punëve ndërtimore për implementimin e masave të Eficiencës së Energjisë në ndërtesat shumë banesore sociale	
Nr. Prokurimit: VET-FKEE2020-24-1699-5-1-1C70 LOT 5	
Kompania punëkryese:  ATC COM SHPK & DAITING SHPK mgatccom@gmail.com	
Emri i ndërtesës: Ndërtesa shumë-banesore sociale II_15, Klinë - Lot 5	
Faza e projektimit: Arkitektura	
Emri i vizatimit: Kati II-IV	
Punuar nga: BSc Liridon Sejdiu	Kontrolluar nga: IDA. Njomza Hoti
Data: 08/2025	Rishikim:
Shkalla e zvogëlimit: P=1:100	Nr. / faqes:

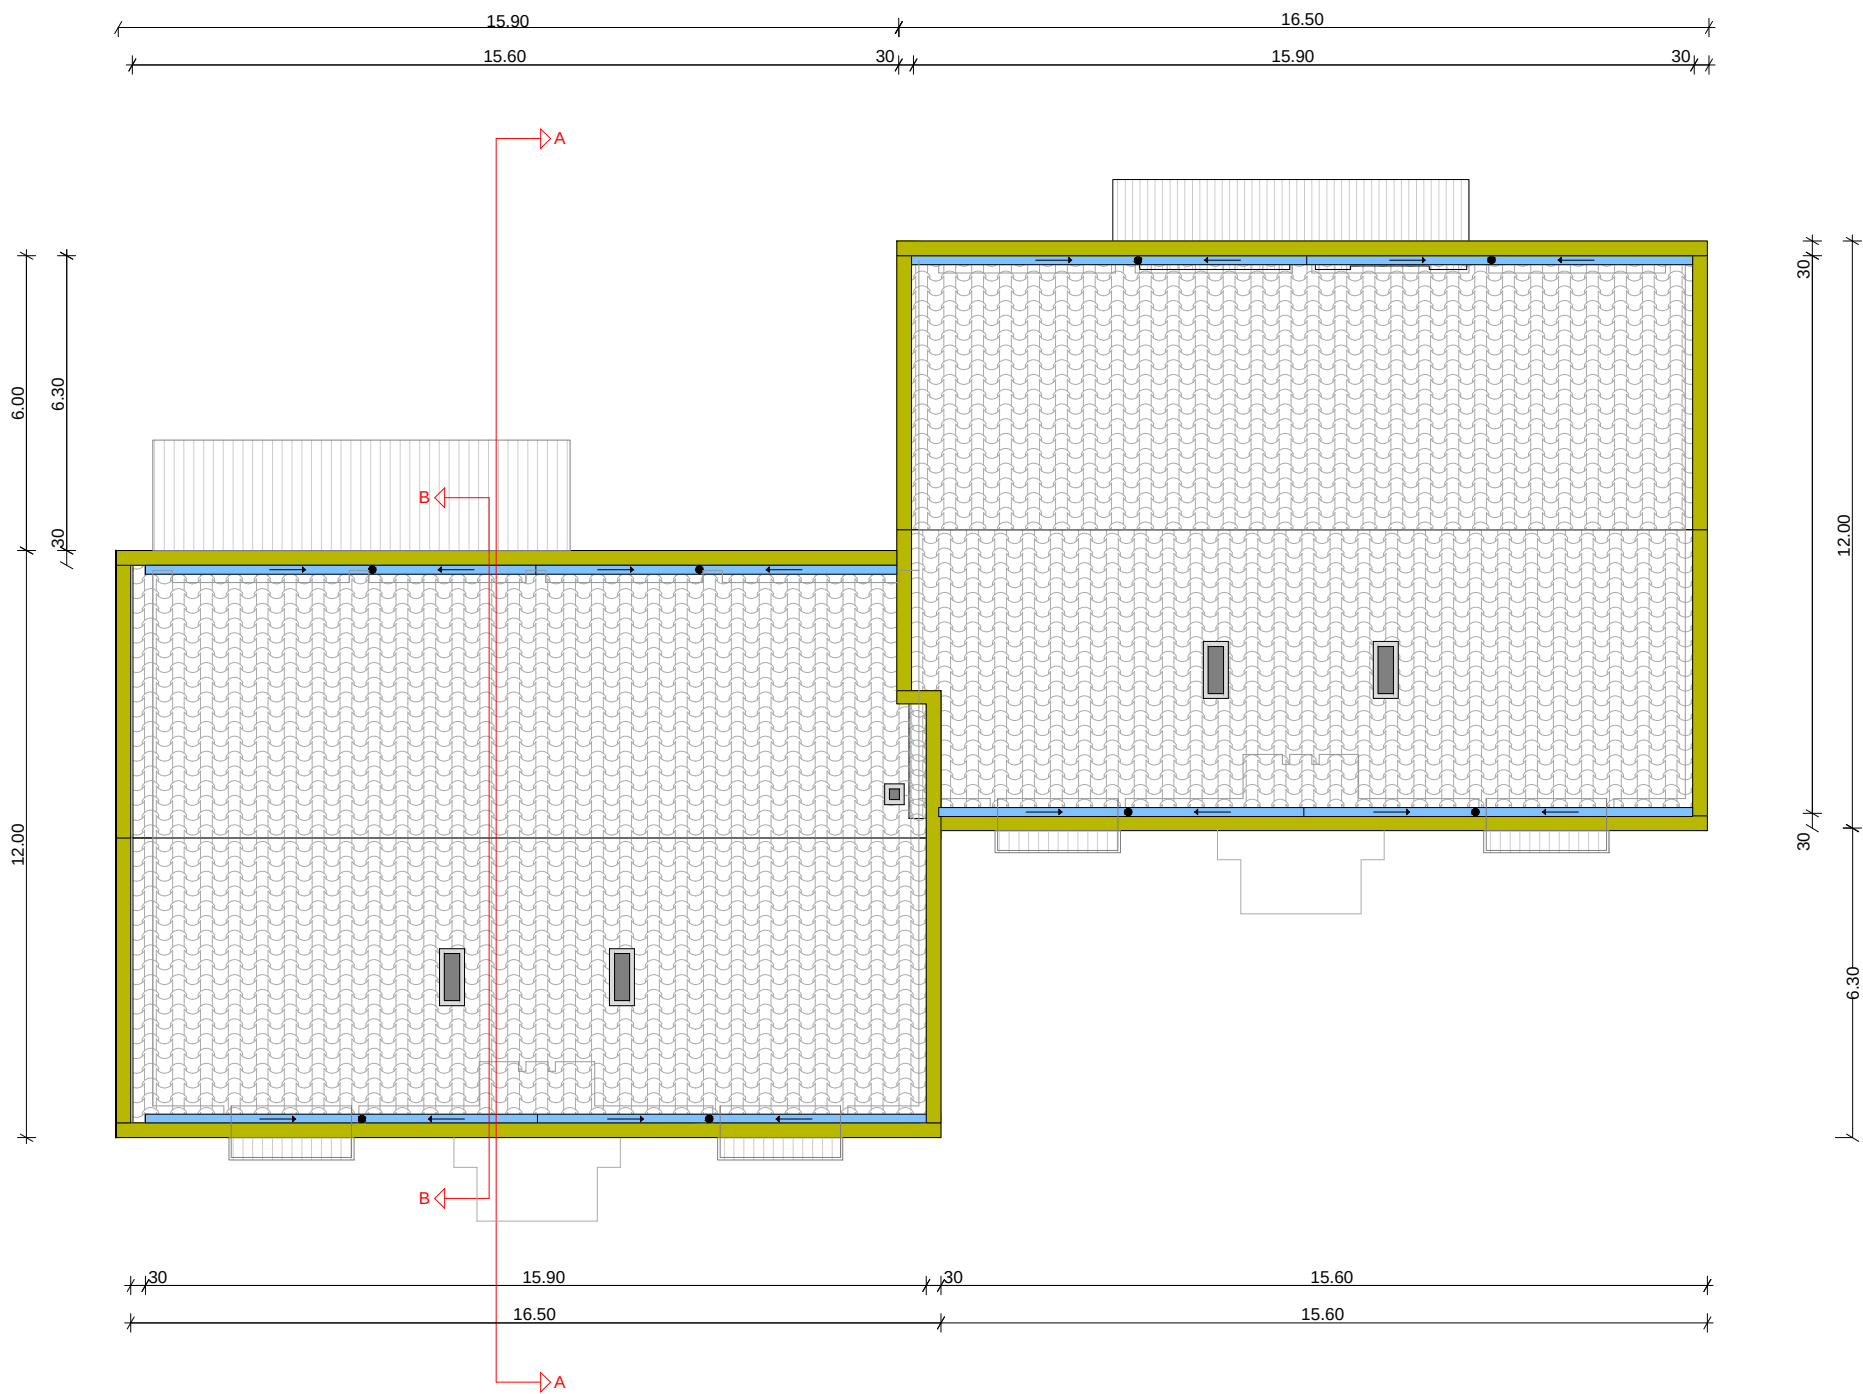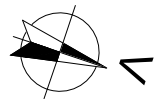

Përshkrimi i renovimit

- Renovimi dhe termoizolimi i kulmit me EPS t=16cm
- Ndërrimi i ulluqeve horizontale
- Ndërrimi i ulluqeve vertikale
- Ndërrimi i pikores
- Ndërrimi i llamarinës së ballkonave



REPUBLIKA E KOSOVËS / REPUBLIC OF KOSOVO
Fondi i Kosovës për Eficiencë të Energjisë
Kosovo Energy Efficiency Fund

Projekti:

Angazhimi i Kompanive për kryerje të punëve ndërtimore për implementimin e masave të Eficiencës së Energjisë në ndërtesat shumë banesore sociale

Nr. Prokurimit : VET-FKEE2020-24-1699-S-1-1/C70 LOT 5

Kompania punëkryese:



ATC COM SHPK & DATING SHPK
nnpattccom@gmail.com

Emri i ndërtesës:

**Ndërtesa shumë-banesore sociale II_15,
Klinë - Lot 5**

Faza e projektimit:

Arkitektura

Emri i vizatimit:

Kulmi

Punuar nga:

BSc Liridon Sejdiu

Kontrolluar nga:

IDA. Njomza Hoti

Date:

08/2025



Rishikim:

Shkalla e zvogëlimit:

P=1:100

Nr. i faqes:

05

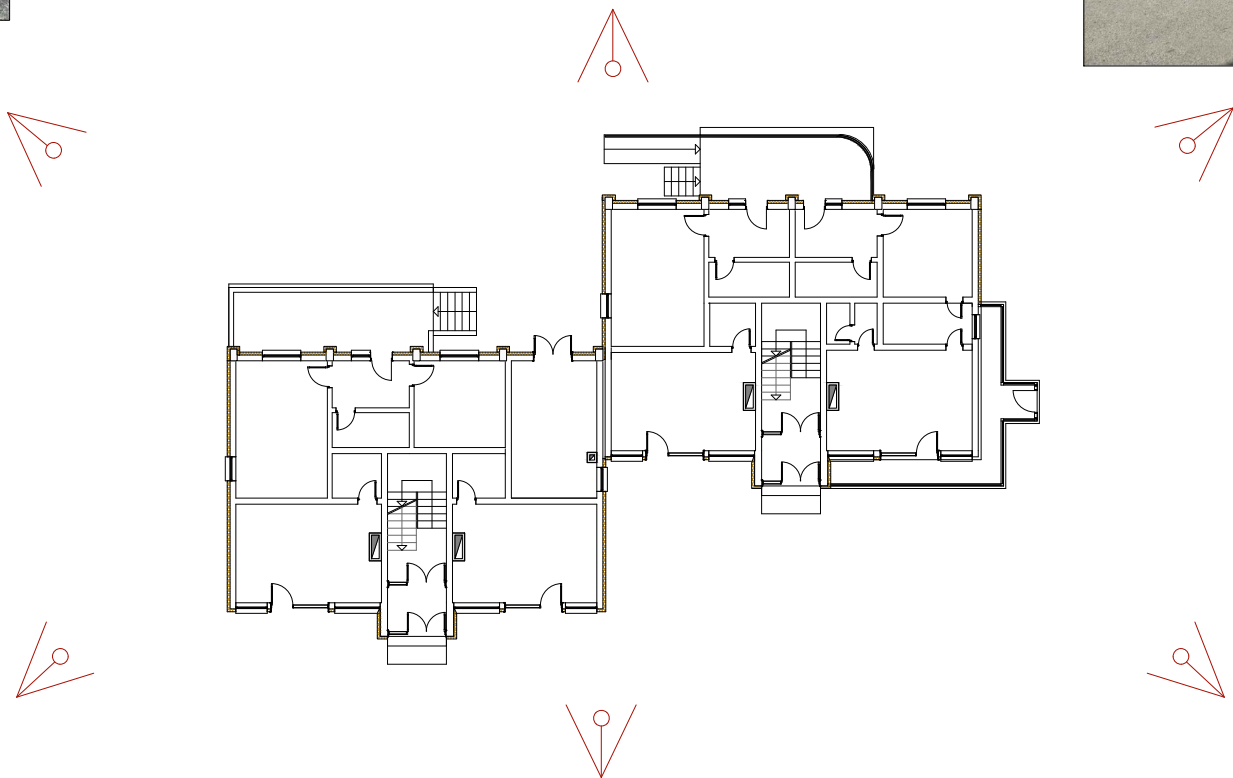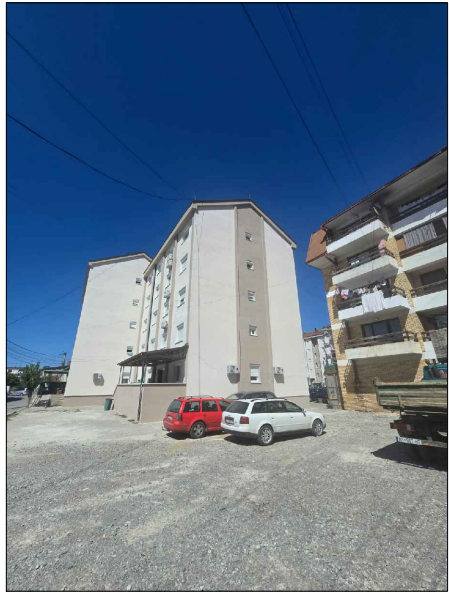



REPUBLIKA E KOSOVËS / REPUBLIC OF KOSOVO
Fondi i Kosovës për Eficiencë të Energjisë
Kosovo Energy Efficiency Fund

Projekti:

Angazhimi i Kompanive për kryerje të punëve ndërtimore për implementimin e masave të Eficiencës së Energjisë në ndërtesat shumë banesore sociale

Nr. Prokurimit : VET-FKEE2020-24-1699-5-1-1/C70 LOT 5

Kompania punekryese:



ATC COM SHPK & DAJTING SHPK
nnpatccom@gmail.com

Emri i ndërtesës:

**Ndërtesa shumë-banesore sociale II_15,
Klinë - Lot 5**


Faza e projektimit:

Arkitektura

Emri i vizatimit:

Fotot e ndërtesës

Punuar nga: BSc Liridon Sejdiu	Kontrolluar nga: IDA. Njomza Hoti
Datë: 08/2025	Rishikim:
Shkalla e zvogëlimit:	Nr. i faqes: 06

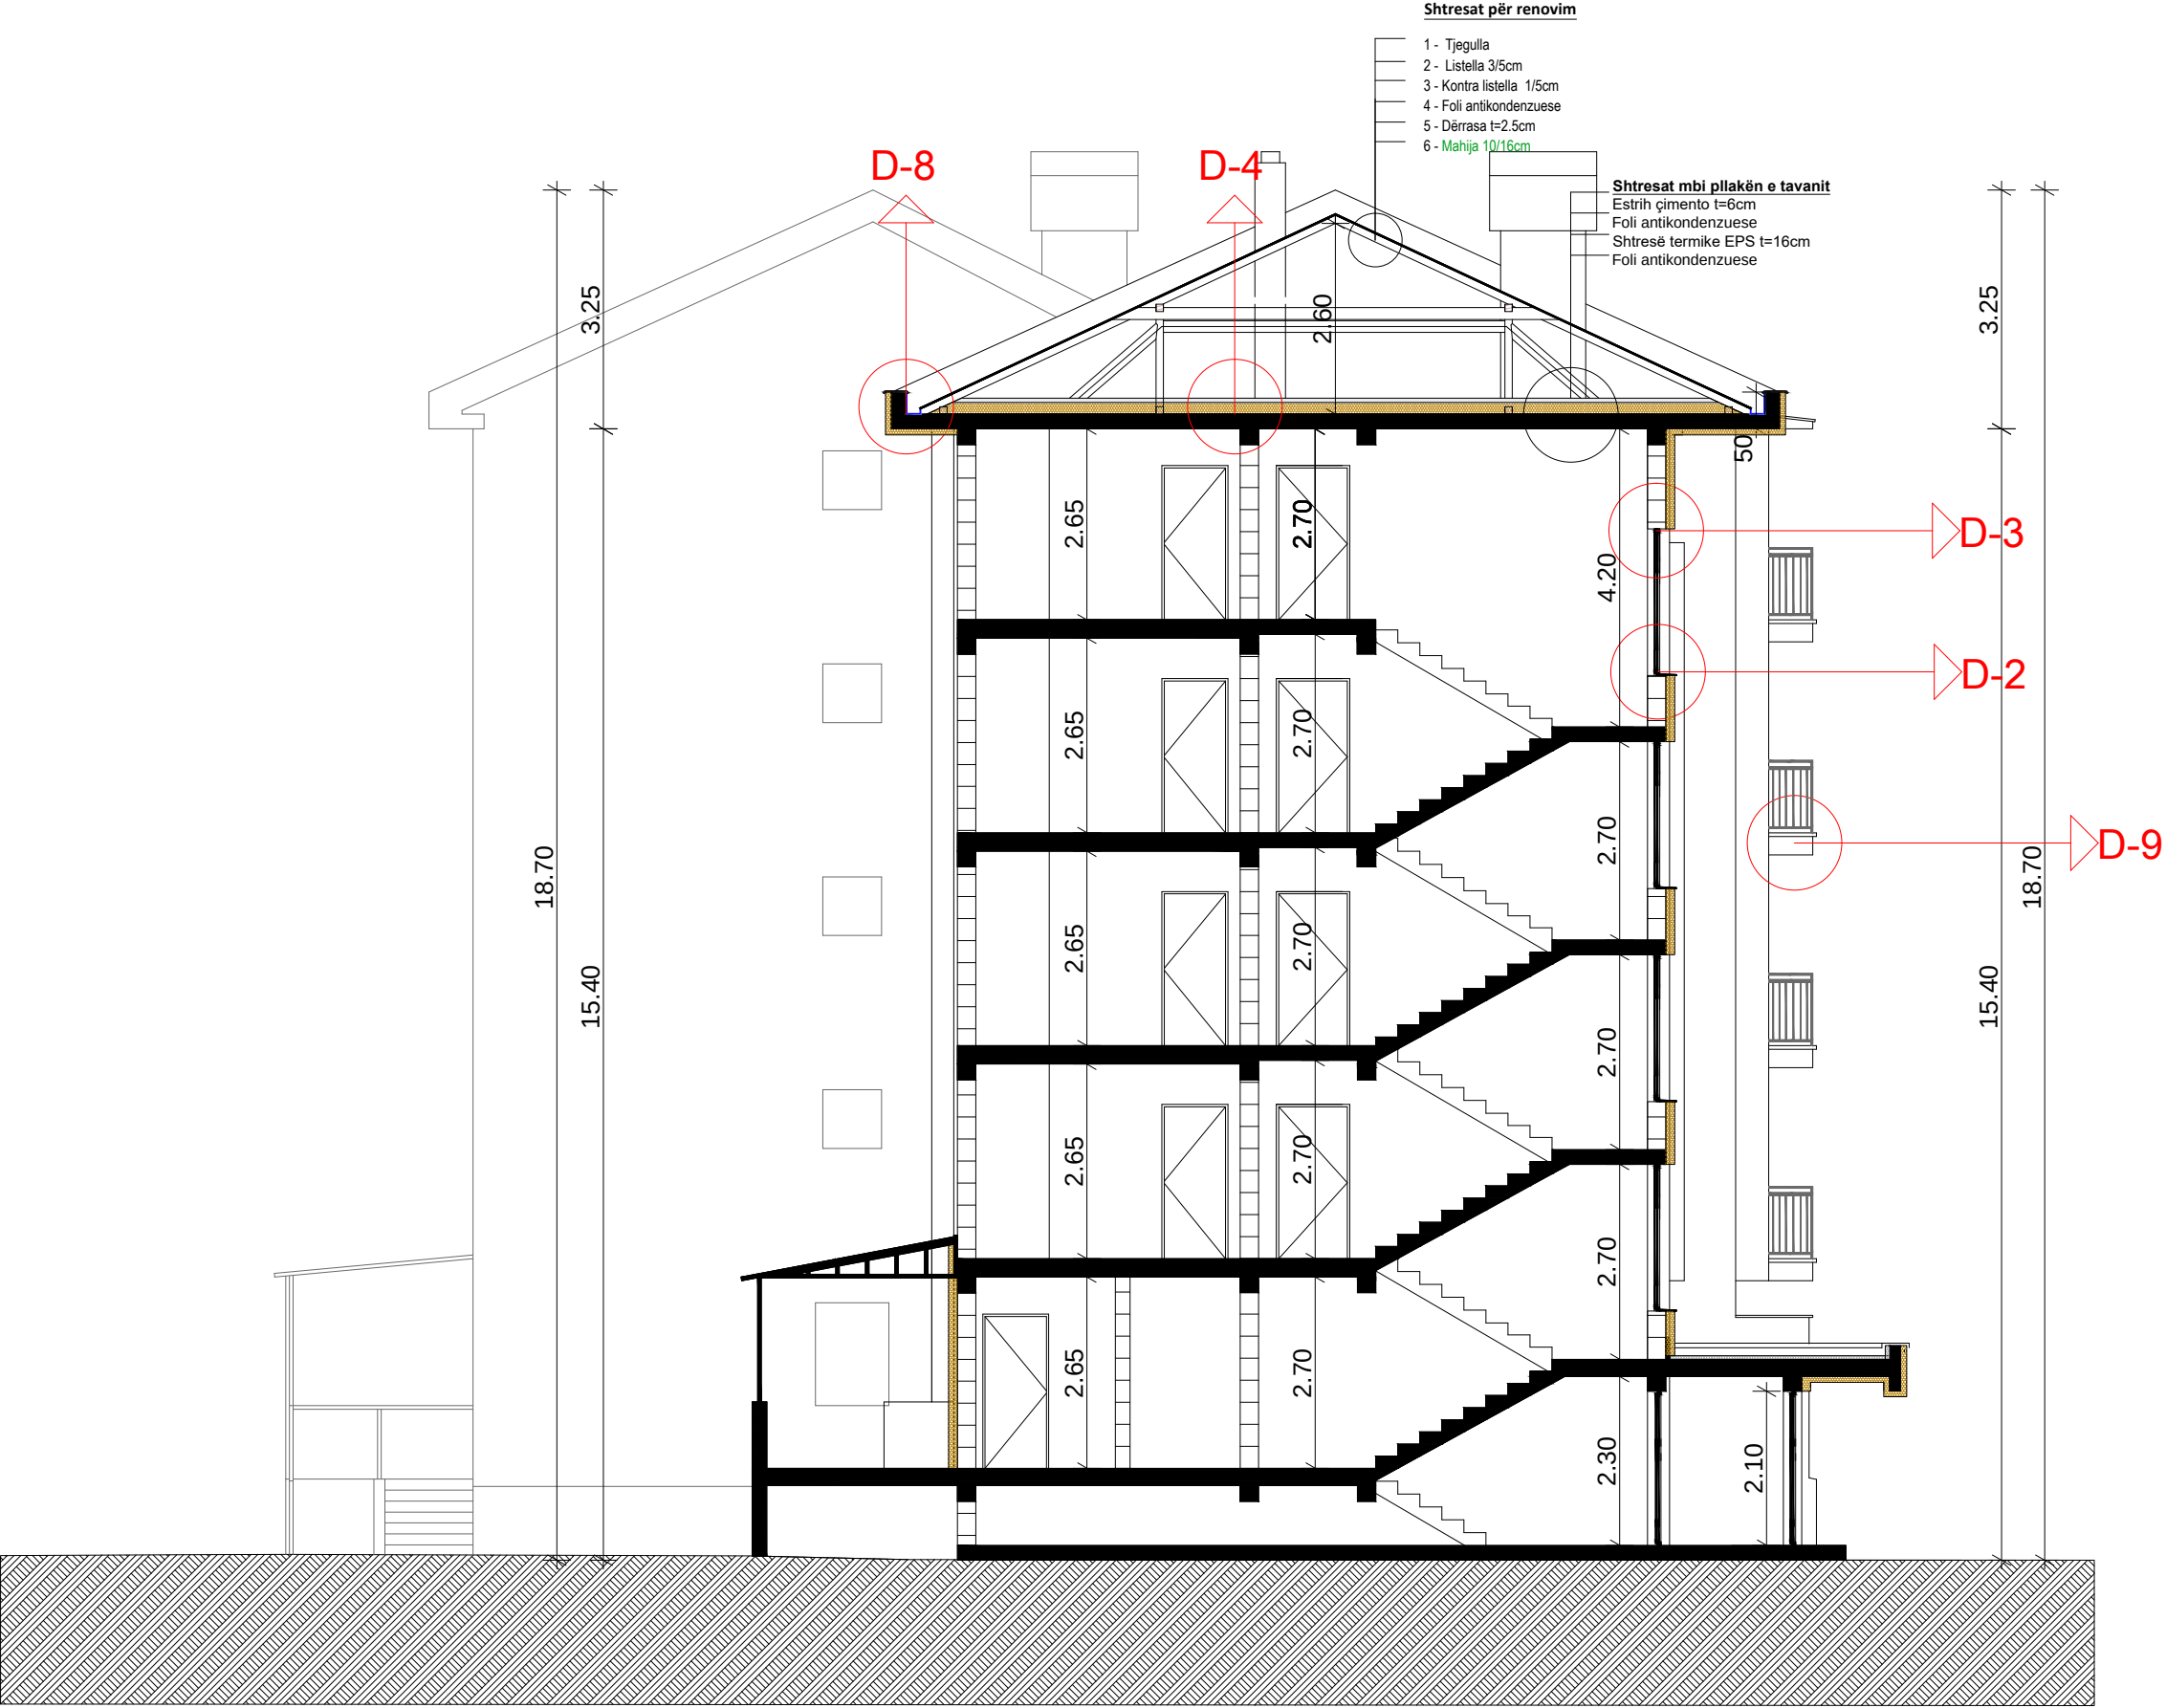

Projekti:

Angazhimi i Kompanive për kryerje të punëve ndërtimore për implementimin e masave të Eficiencës së Energjisë në ndërtesat shumë banesore sociale

Nr. Prokurimit : VET-FKEE2020-24-1699-5-1-1/C70 LOT 5

Kompania punëkryese:



ALL TYPES OF CONSTRUCTION

ATC COM SHPK & DAJTING SHPK

nnpatccom@gmail.com

Emri i ndërtesës:

Ndërtesa shumë-banesore sociale II_15,

Klinë - Lot 5


Faza e projektimit:

Arkitektura

Emri i vizatimit:

Prerja A-A


Punuar nga:	Kontrolluar nga:
BSc Liridon Sejdiu	IDA. Njomza Hoti
Datë:	Rishikim:
08/2025	
Shkalla e zvogëlimit:	Nr. i faqes:
P=1:100	07

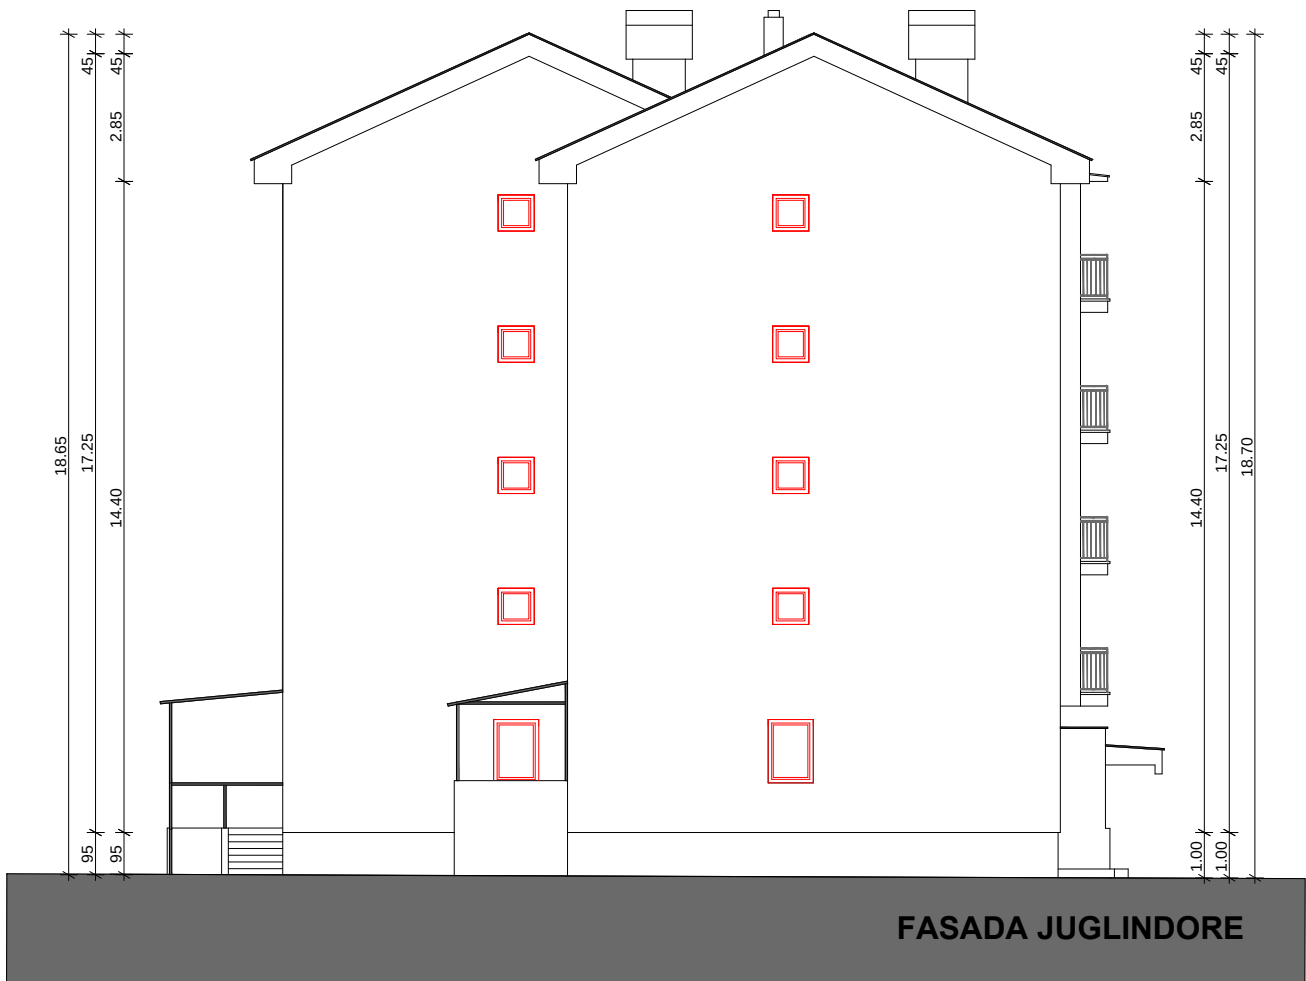

Përshkrimi renovimit

- Ndërrimi i dritareve
- Ndërrimi i dyerve
- Dyer/dritare ekzistuese e barnatores

 REPUBLIKA E KOSOVËS / REPUBLIC OF KOSOVO Fondi i Kosovës për Eficiencë të Energjisë Kosovo Energy Efficiency Fund	
Projekti: Angazhimi i Kompanive për kryerje të punëve ndërtimore për implementimin e masave të Eficiencës së Energjisë në ndërtesat shumë banesore sociale	
Nr. Prokurimit : VET-FKEE2020-24-1699-5-1-1/C70 LOT 5	
Kompania punëkryetare:  ATC COM SHPK & DAIJING SHPK nmpatcom@gmail.com	
Emri i ndërtesës: Ndërtesa shumë-banesore sociale II_15, Klinë - Lot 5	
Faza e projektimit: Arkitektura	
Emri i vizatimit: Fasada Veriore & Lindore	
Punuar nga: BSc Liridon Sejdiu	Kontrolluar nga: IDA. Njomza Hoti
Data: 08/2025	Rishikim:
Shkalla e zvogëlitimit: P=1:100	Nr. i faqes: 08

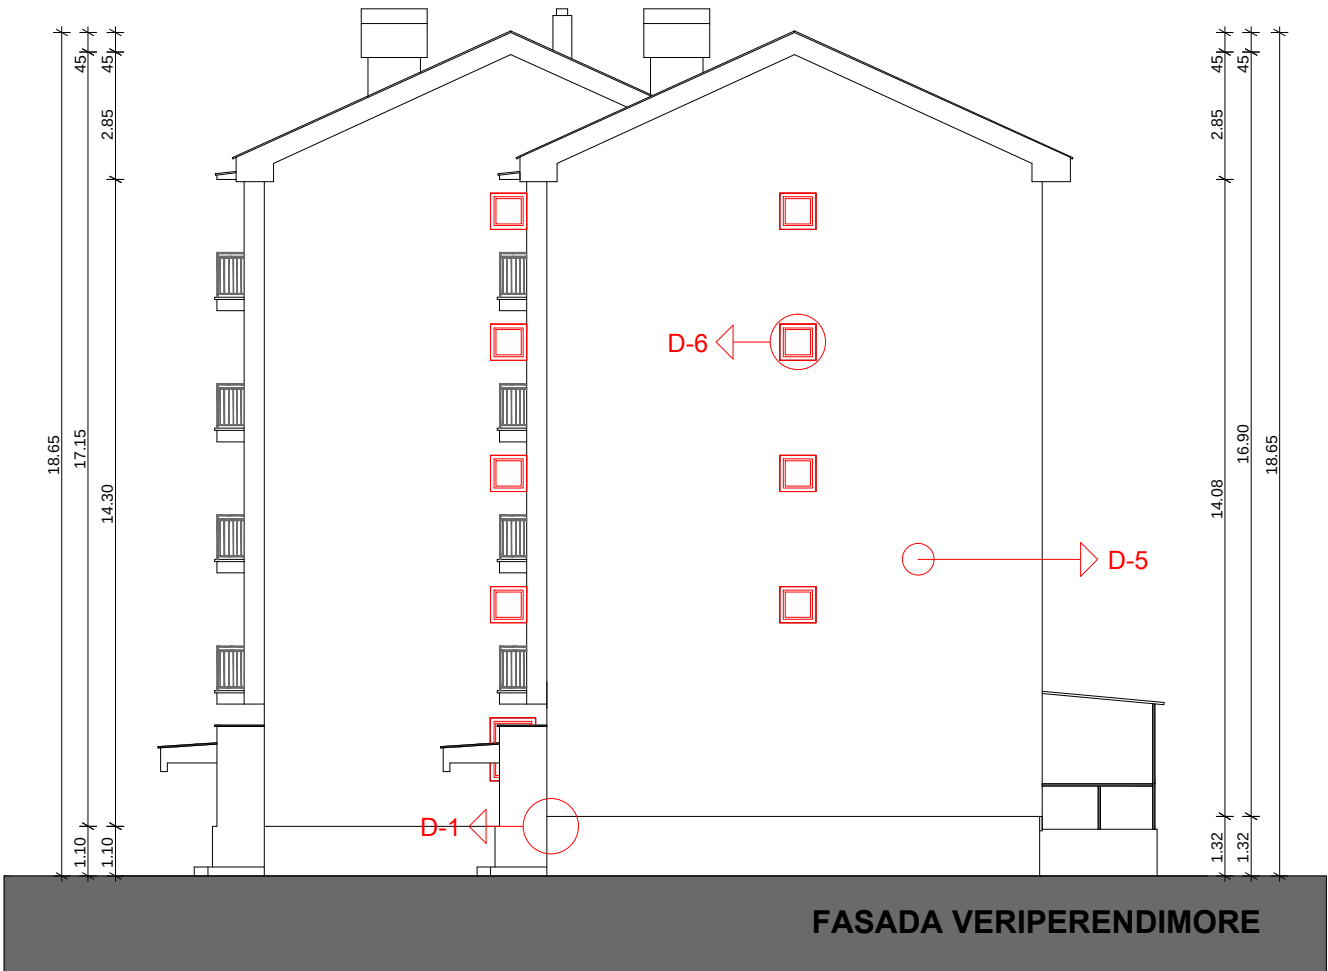

- Përshkrimi renovimit**
- Ndërrimi i dritareve
 - Ndërrimi i dyerve
 - Ngjyrosje dhe renovimi i derës ekzistuese



Projekti:
Angazhimi i Kompanive për kryerje të punëve ndërtimore për implementimin e masave të Eficiencës së Energjisë në ndërtesat shumë banesore sociale

Nr. Prokurimit : VET-FKEE2020-24-1699-5-1-1/C70 LOT 5



Emri i ndërtësit:
Ndërtesa shumë-banesore sociale II_15, Klinë - Lot 5

Faza e projektimit:
Arkitektura

Emri i vizatimit:
Fasada Jugore & Perëndimore

Punuar nga:
BSc Liridon Sejdiu

Kontrolluar nga:
IDA. Njomza Hoti

Data:
08/2025

Shkalla e zvogëlitimit:
P=1:100

Nr. / faqes:
09



FASADA VERILINDORE



FASADA JUGLINDORE



FASADA JUGPERENDIMORE



FASADA VERIPERENDIMORE

Vërejtje: Masat mbrojtëse kundër zjarrit duhet të instalohen në tërë perimetrin e ndërtesës, si unazë me lesh guri dhe lartësi h=60cm sipas paraqitjeve grafike

Përshkrimi renovimit

 Termoizolimi i mureve me Lesh Guri t=12cm



REPUBLIKA E KOSOVËS / REPUBLIC OF KOSOVO
Fondi i Kosovës për Eficiencë të Energjisë
Kosovo Energy Efficiency Fund

Projekti:
Angazhimi i Kompanive për kryerje të punëve ndërtimore për implementimin e masave të Eficiencës së Energjisë në ndërtesat shumë banesore sociale

Nr. Prokurimit : VET-FKEE2020-24-1699-S-1-1/C70 LOT 5

Kompania punëkryese:



ATC COM SHPK & DAJTING SHPK
nnpatcom@gmail.com

Emri i ndërtesës:
**Ndërtesa shumë-banesore sociale II_15,
Klinë - Lot 5**

Faza e projektit:
Arkitektura

Emri i vizatimit:
Mbrojtja nga zjarri

Punuar nga: BSc Liridon Sejdiu	Kontrolluar nga: IDA. Njomza Hoti
Data: 08/2025	Rishikim:
Shkalla e zvogëlimit: P=1:50	Nr. i faqes: 10

