
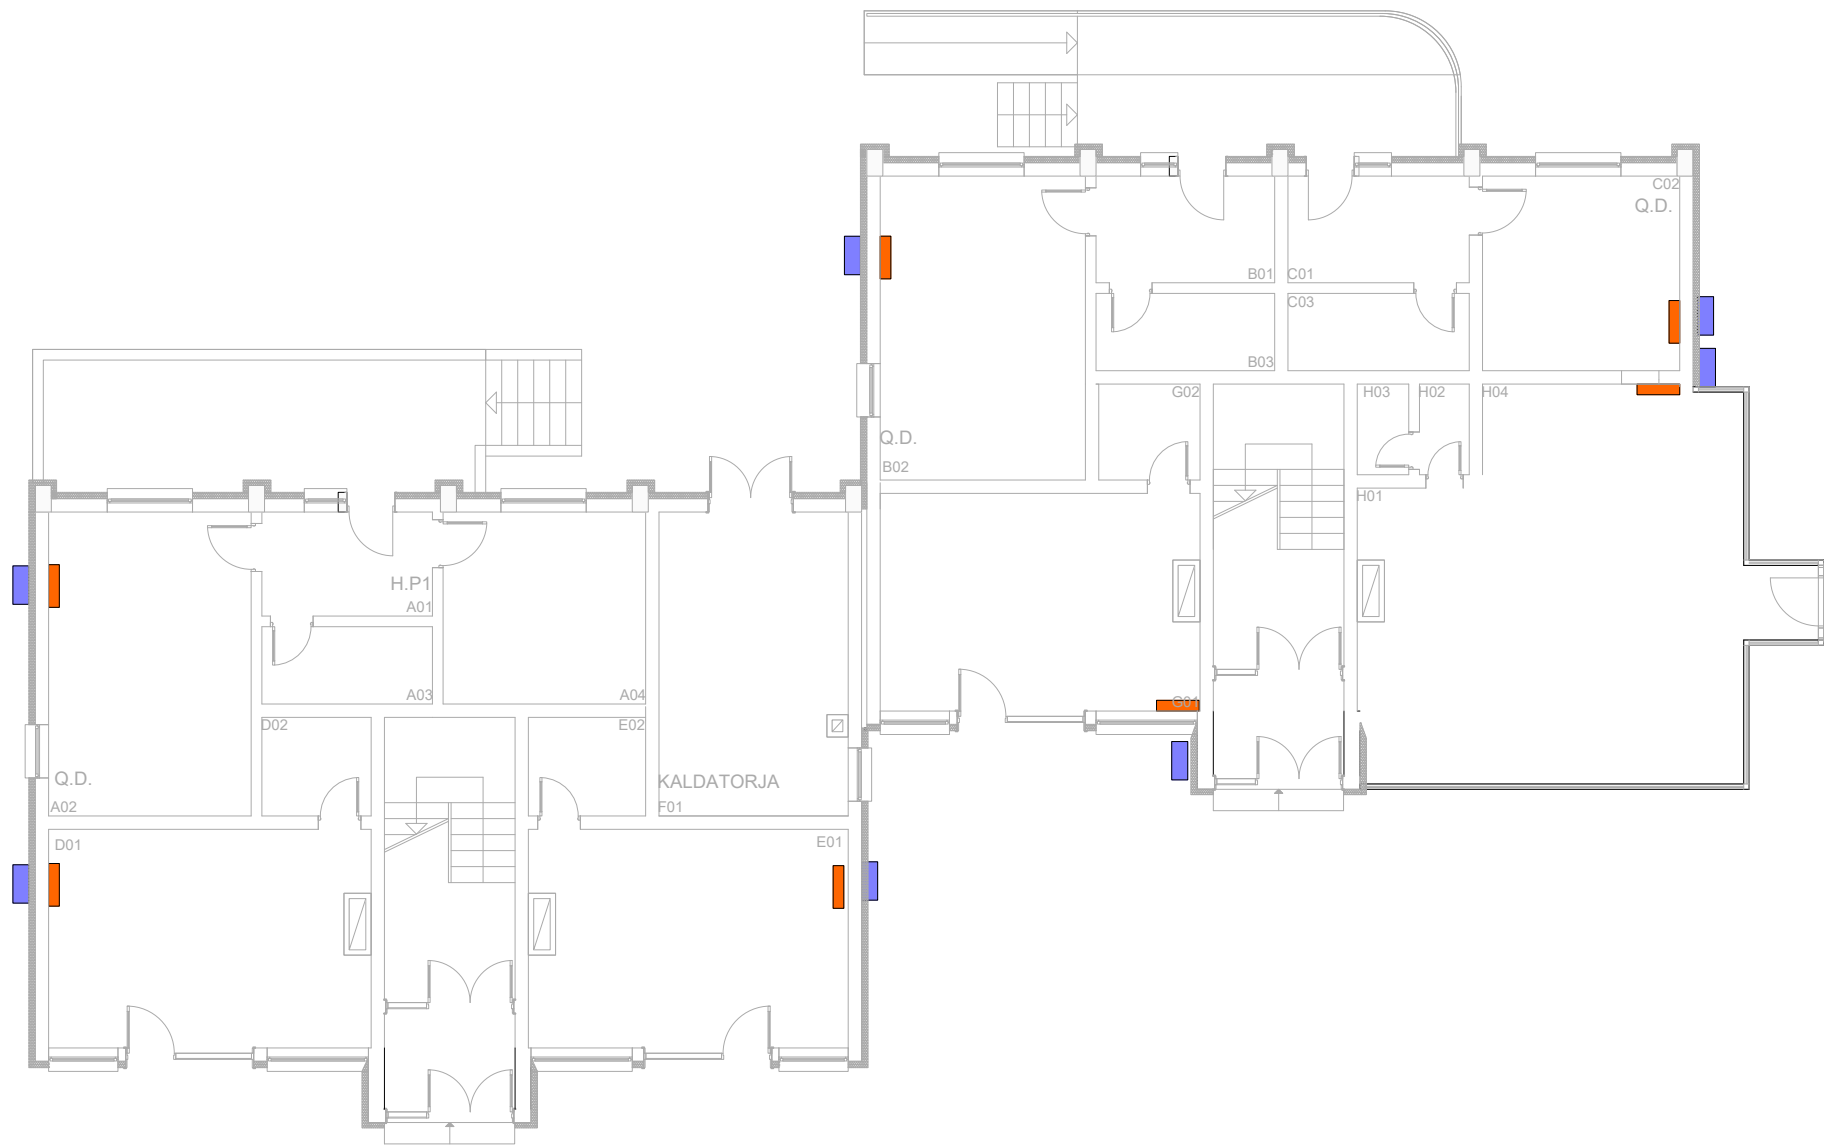


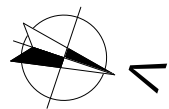

FKEE FUNDI I KOSOVËS PËR EFICIENCËN E ENERGJISË KOSOVO ENERGY EFFICIENCY FUND REPUBLIKA E KOSOVËS / REPUBLIC OF KOSOVO Fondi i Kosovës për Eficiencë të Energjisë Kosovo Energy Efficiency Fund	
Projekti: Angazhimi i Kompanive për kryerje të punëve ndërtimore për implementimin e masave të Eficiencës së Energjisë në ndërtesat shumë-banesore sociale	
Nr.Prokurimit:VET-FKEE2020-24-1699-5-1-1/C70	
Kompania pun kryese: ATC COM ALL TYPES OF CONSTRUCTION ATC COM SHPK & DAJTING SHPK nnpatcom@gmail.com	
Emri i ndërtesës: Ndërtesa shumë-banesore sociale II_15, Klinë - Lot 5	
Faza e projektimit: Makineria	
Emri i vizatimit: Përdhesa	
Punuar nga: BSc Liridon Sejdiu	Kontrolluar nga: IDA. Njomza Hoti
Data: 08/2025	Rishikim:
Shkalla e zvogëlimit: P=1:100	Nr. i faqes: 02

Description renovation / Përshkrimi renovimit



12000 BTU/hr - Indoor Unit/Njësia e brendshme
(WxDxH) (835x208x295)

12000 BTU/hr - Outdoor Unit/Njësia e jashtme
(WxDxH) (720x270x495)

Liquid Pipe/ Gypi i lëngut

Gas Pipe/ Gypi i gazit

Condensate Pipe/ Gypi i kondenzatit

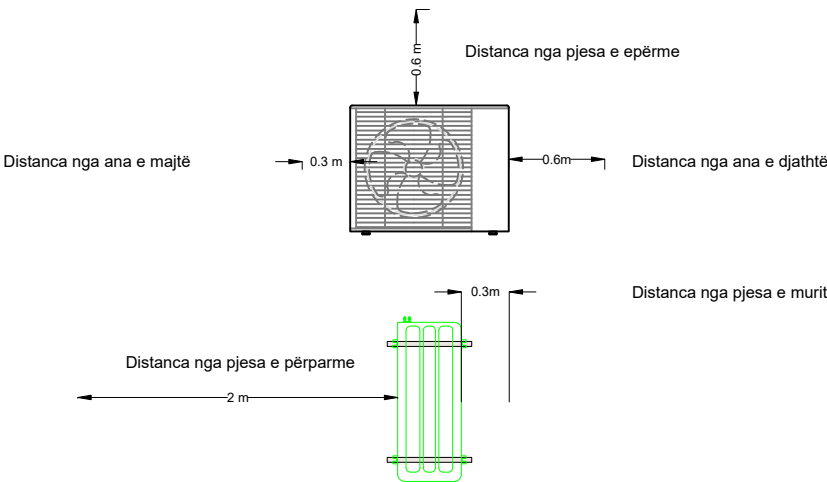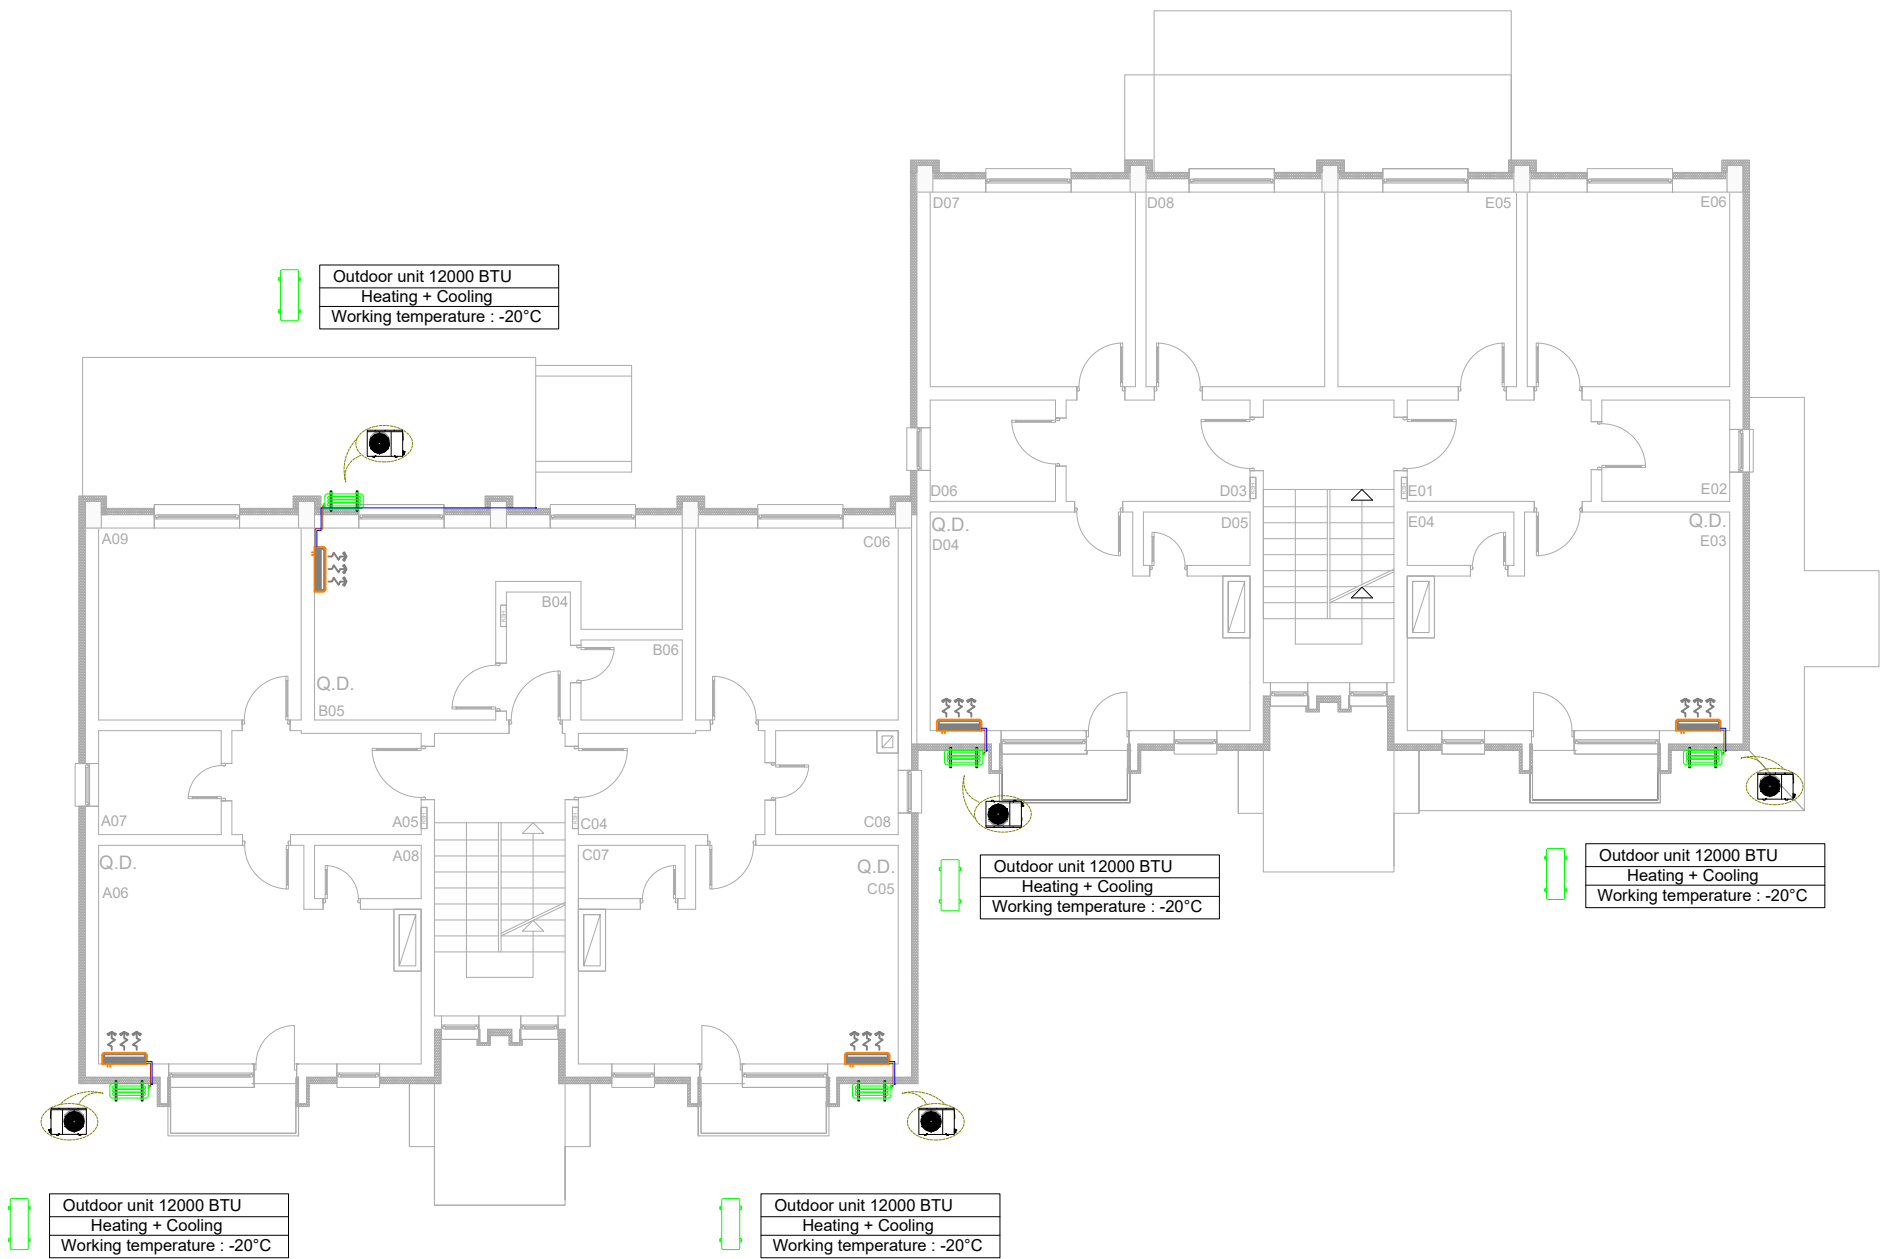

 REPUBLIKA E KOSOVËS / REPUBLIC OF KOSOVO Fondi i Kosovës për Eficiencë të Energjisë Kosovo Energy Efficiency Fund	
Projekti: Angazhimi i Kompanive për kryerje të punëve ndërtimore për implementimin e masave të Eficiencës së Energjisë në ndërtesat shumë banesore sociale	
Nr.Prokurimit: VET-FKEE2020-24-1699-S-1-1/C70 Lot 5	
 Kompania pun kryese:	ATC COM SHPK & DAJTING SHPK nnpatccom@gmail.com
Emri i ndërtuesit: Ndërtesa shumë-banesore sociale II_15, Klinë - Lot 5	
Faza e projektimit: Makineria	
Emri i vizatimit: Kati karakteristik	
Punuar nga: BSc Liridon Sejdiu	Kontrolluar nga: IDA. Njomza Hoti
Data: 08/2025	Rishikim:
Shkalla e zvogëlimit: P=1:100	Nr. i faqes: 02