



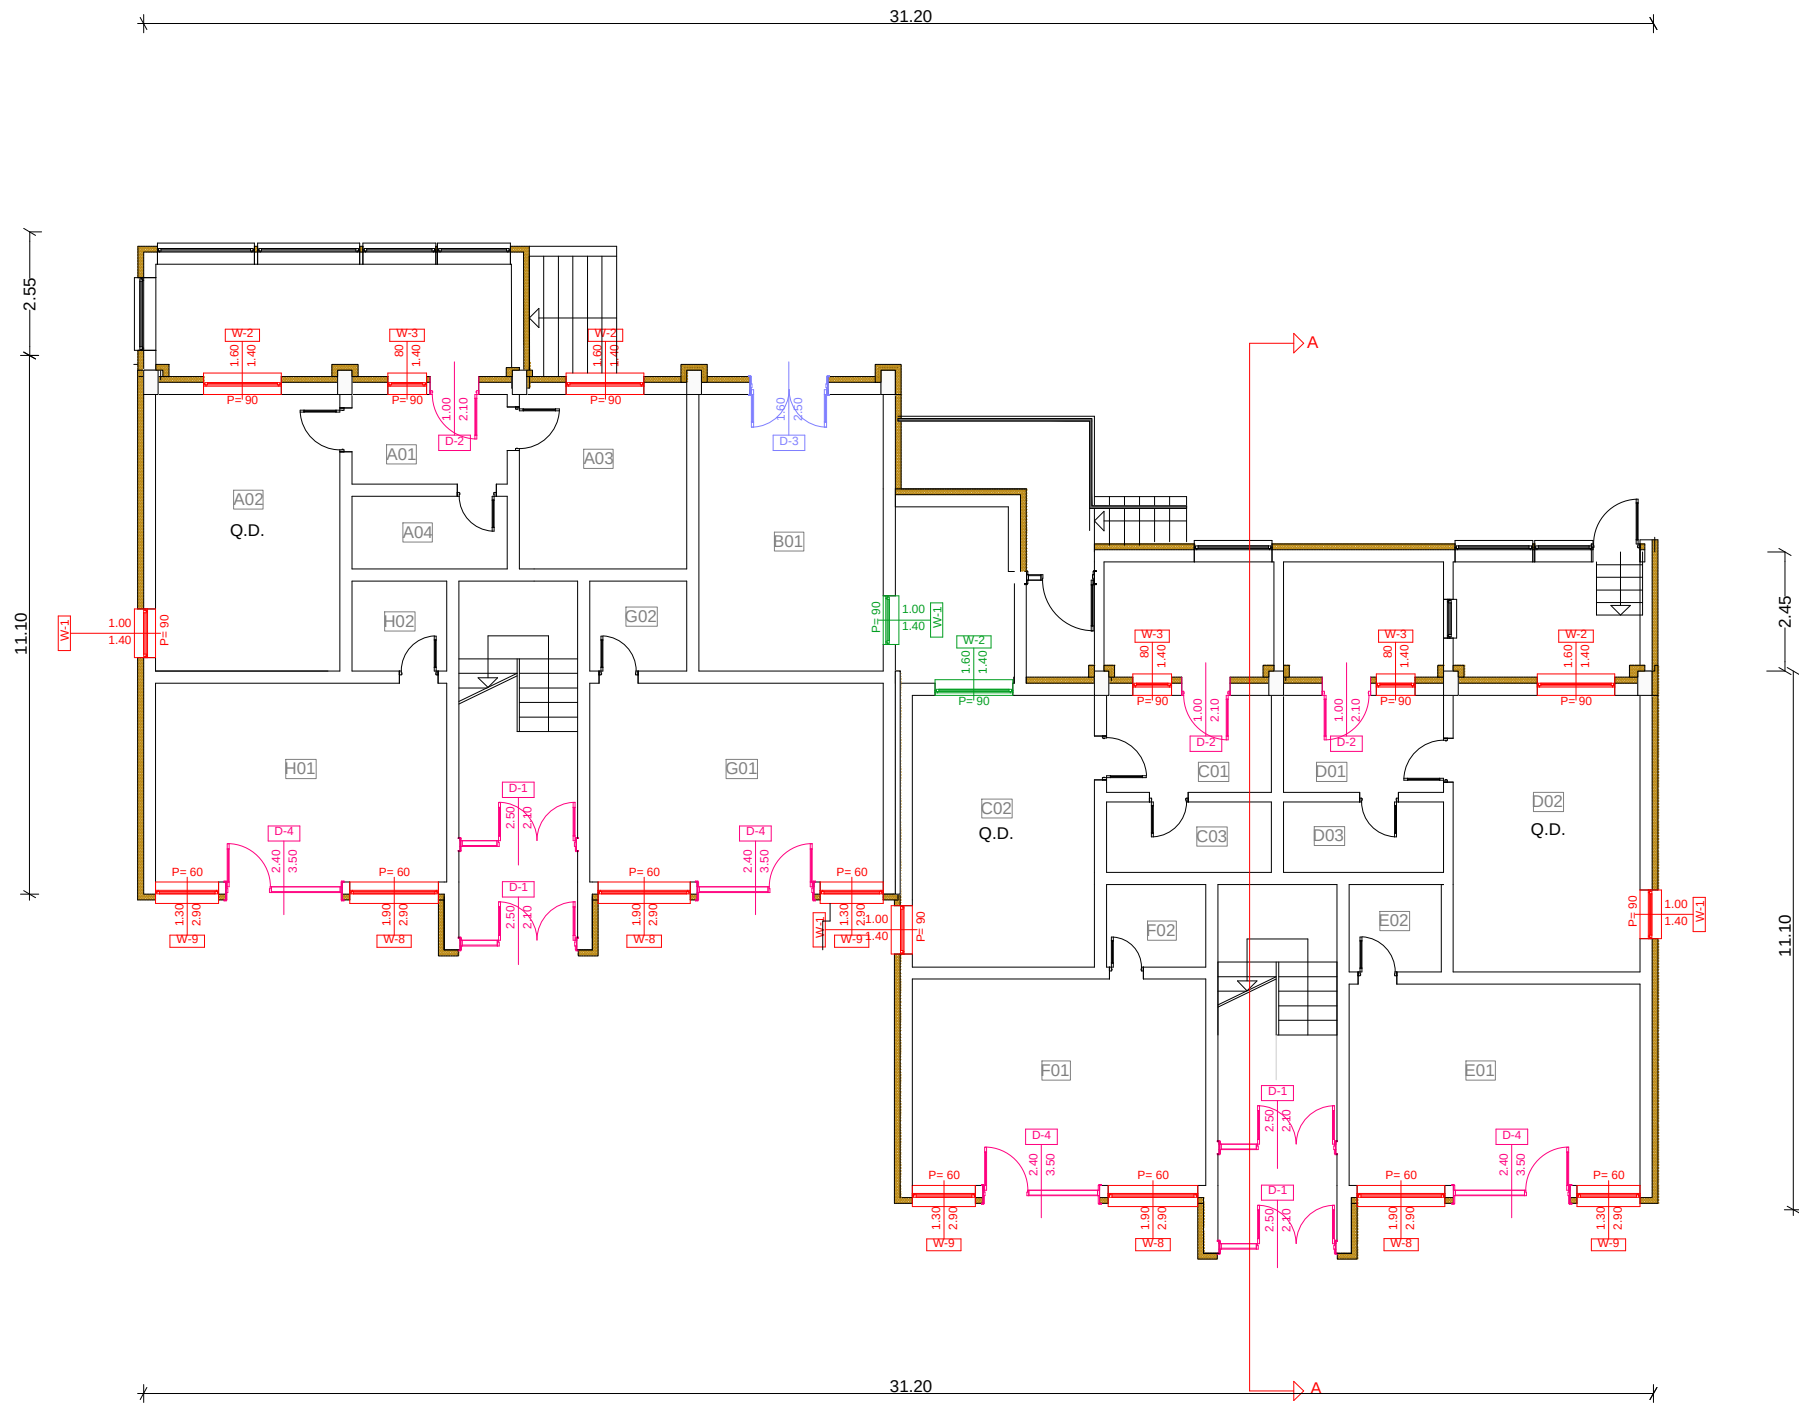

Përshkrimi renovimit

- Termoizolimi i mureve me EPS t=12cm
- Ndërimi i dritareve
- Ndërimi i dyerve
- Dritare të reja
- Ngjyrosje dhe renovimi i derës ekzistuese

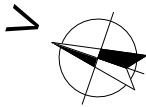

REPUBLIKA E KOSOVËS / REPUBLIC OF KOSOVO
Fondi i Kosovës për Eficiencë të Energjisë
Kosovo Energy Efficiency Fund

Projekti:
Angazhimi i Kompanive për kryerje të punëve ndërtimore për implementimin e masave të Eficiencës së Energjisë në ndërtesat shumë banesore sociale

Nr. i kontratës: VET-FKEE2020-23-3696-2-1-1/C35_Lot 5



ATC COM SHPK & DAITING SHPK
ngpatccom@gmail.com

Emri i ndërtuesit:
**Ndërtesa shumë banesore sociale III,
Klinë - Lot 5**

Faza e projektimit:
Arkitektura

Emri i vizatimit:
Përdhesa

Punuar nga: BSc Liridon Sejdiu	Kontrolluar nga: IDA. Njomza Hoti
Data: 08/2025	Rishikim:
Shkalla e zvogëlimit: P=1:100	Nr. i faqes: 02

650x420mm