



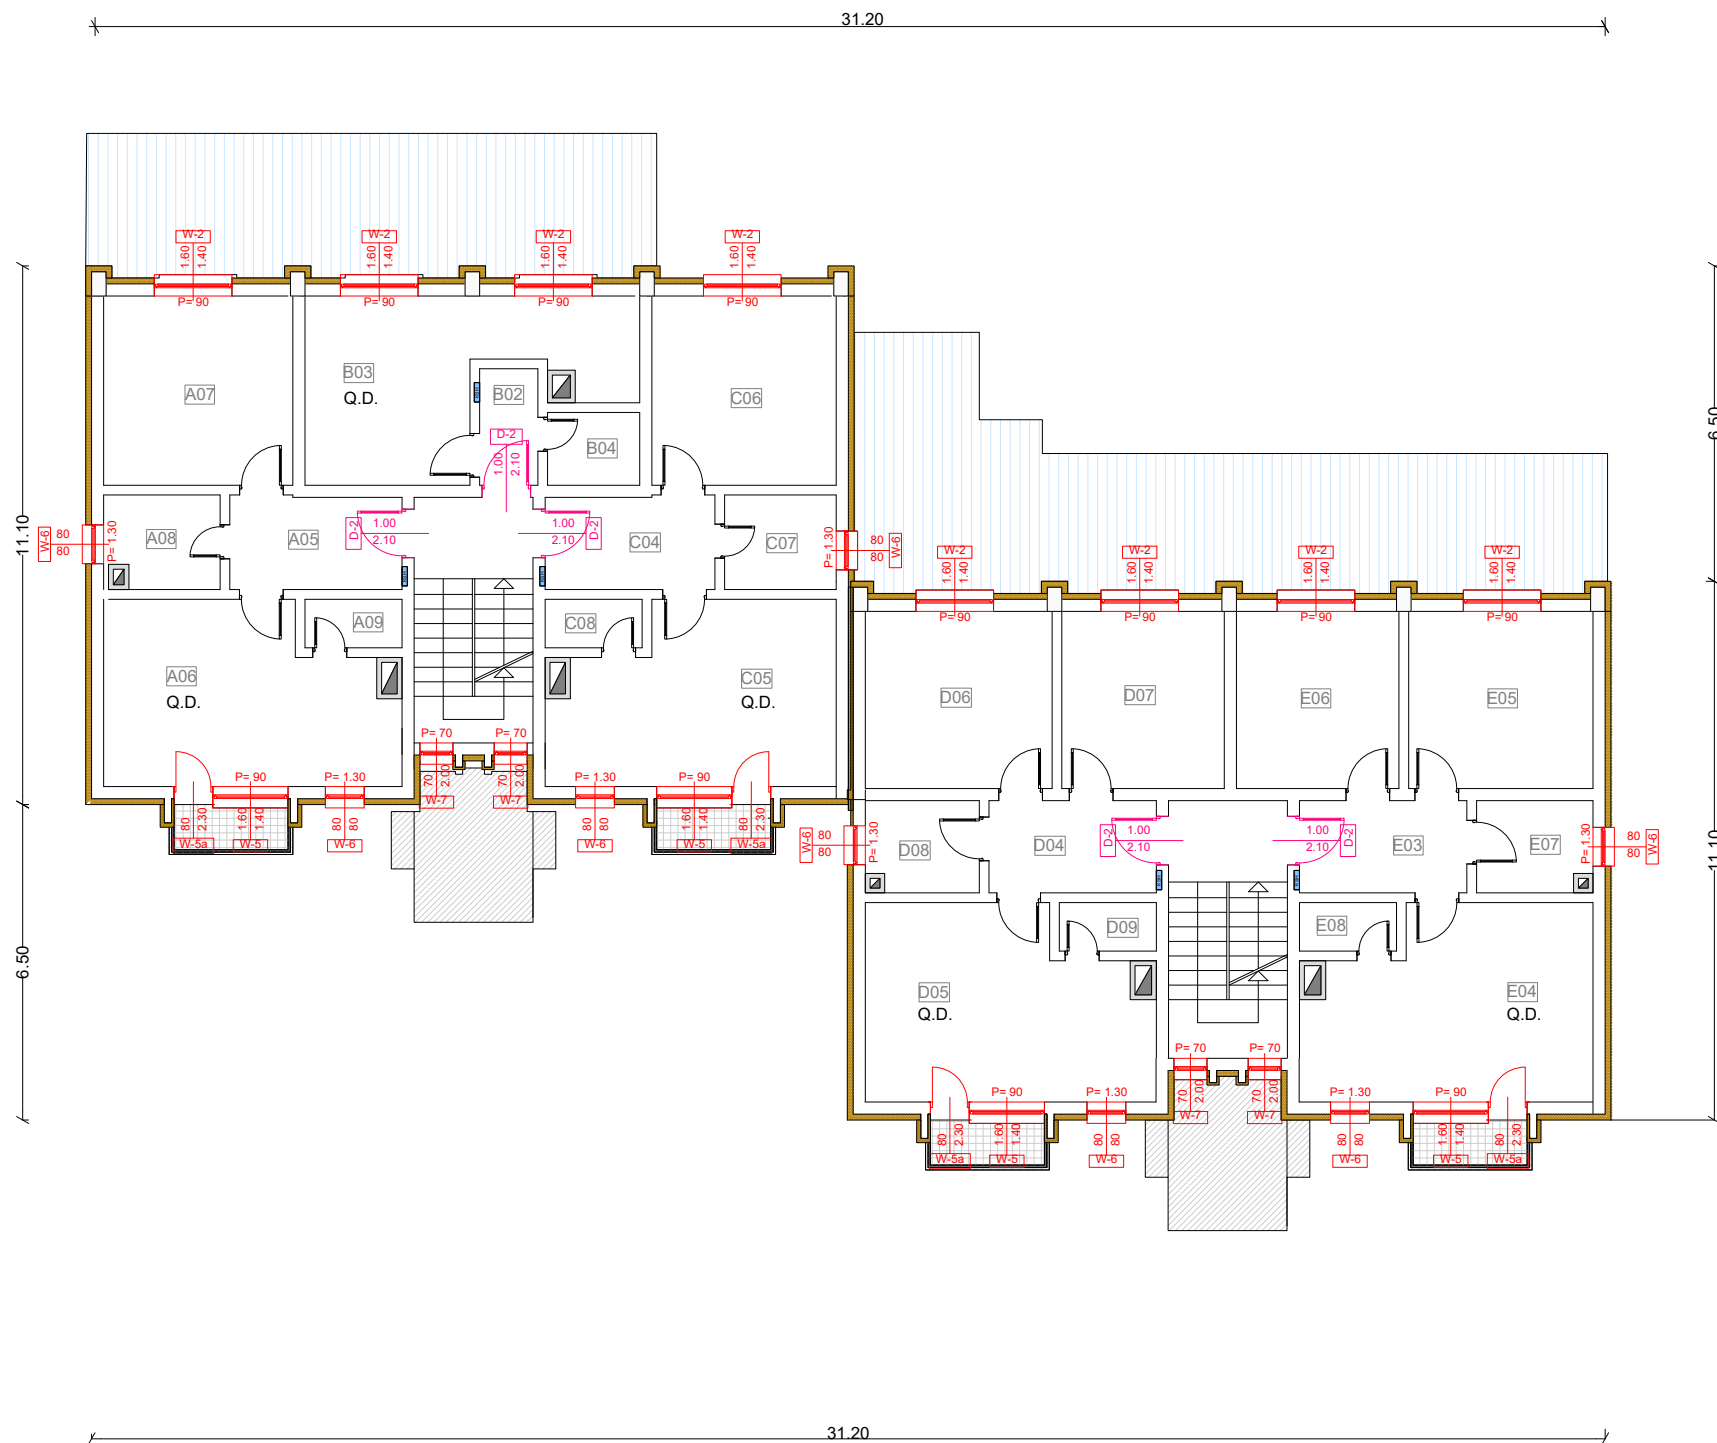

Përshkrimi i renovimit

- Termoizolimi i mureve me EPS t=12cm
- Ndërrimi i dritareve
- Ndërrimi i dyerve
- Renovimi i kulmit të strehës
- Kulmet e anekseve

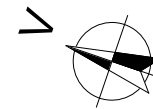

REPUBLIKA E KOSOVËS / REPUBLIC OF KOSOVO
Fondi i Kosovës për Eficiencë të Energjisë
Kosovo Energy Efficiency Fund

Nr. i kontratës: VET-FKEE2020-23-3896-2-1-1/C35_Lot 5

Kompania punëkryese:



ATC COM SHPK & DATING SHPK
mpatccom@gmail.com

Emri i ndërtuesit:

**Ndërtesa shumë banesore sociale III,
Klinë - Lot 5**

Faza e projektimit:

Arkitektura

Emri i vizatimit:

Kati I

Punuar nga:	Kontrolluar nga:
BSc Liridon Sejdiu	IDA. Njomza Hoti
Data:	Rishikim:
08/2025	
Shkalla e zvogëlimit:	Nr. i faqes:
P=1:100	03