
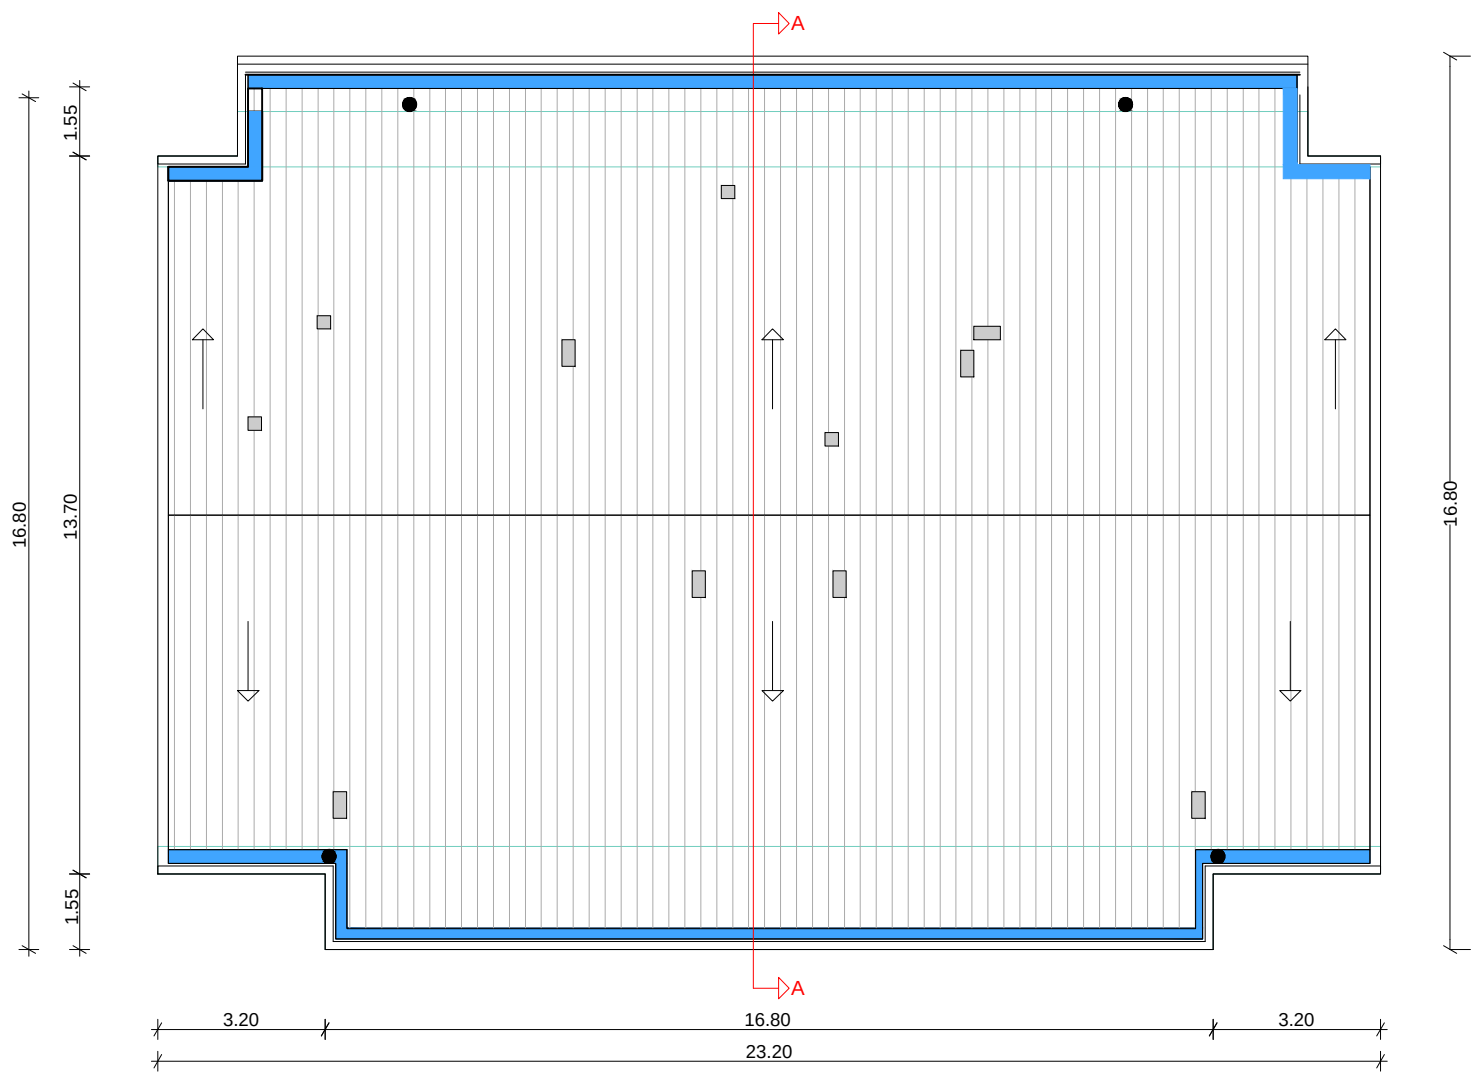


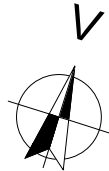

Përshkrimi renovimit

-  Ndërrimi i mbulesës dhe termoizolimi i kulmit me EPS t=16cm
-  Ndërrimi i ulluqeve horizontale
-  Ndërrimi i ulluqeve vertikale

FKEE FUNDI I KOSOVËS PËR EFIÇIENCË TË ENERGISË FOND FUNDI I KOSOVËS PËR EFIÇIENCË TË ENERGISË Kosovo Energy Efficiency Fund	
Projekti: Angazhimi i Kompanive për kryerje të punëve ndërtimore për implementimin e masave të Eficiencës së Energjisë në ndërtesat shumë banesore sociale	
Nr. Prokurimit : VET-FKEE2020-24-1699-5-1-UC70 LOT 5 Kompania punekryese ATC ALL TYPES OF CONSTRUCTION COM ATC COM SHPK & DAJTING SHPK nnpstccom@gmail.com	
Emri i ndërtesës: Ndertesa shume banesor Social I, Klinë	
Faza e projektimit: Arkitektura	
Emri i vizatimit: Kulmi	
Punuar nga: BSc Liridon Sejdiu	Kontrolluar nga: IDA. Njomza Hoti
Date: 08/2025	Rishikim:
Shkalla e zvogëlimit: P=1:100	Nr. i faqes: 04