



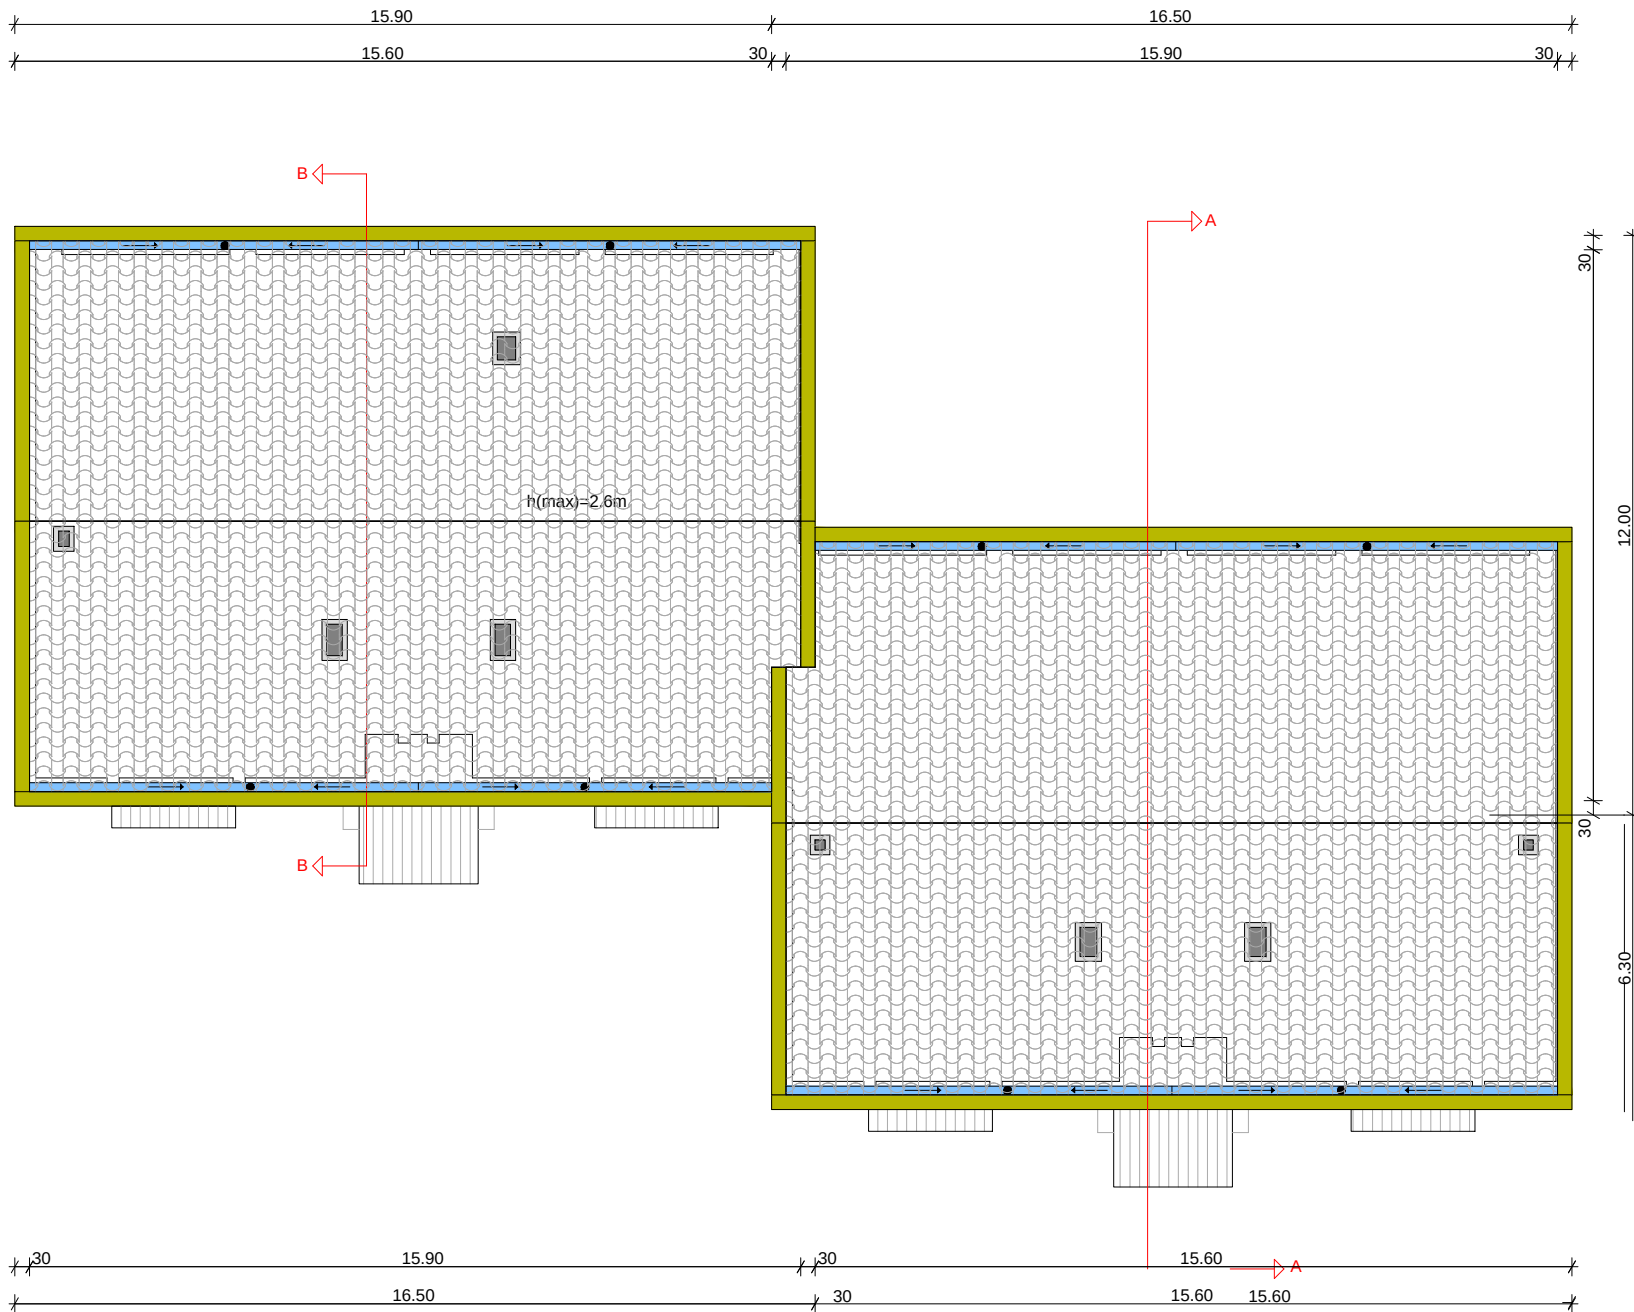

Përshkrimi i renovimit

- Renovimi dhe termoizolimi i kulmit me EPS t=16cm
- Ndërrimi i ulluqeve horizontale
- Ndërrimi i ulluqeve vertikale
- Ndërrimi i pikores

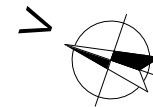

REPUBLIKA E KOSOVËS / REPUBLIC OF KOSOVO
Fondi i Kosovës për Eficiencë të Energjisë
Kosovo Energy Efficiency Fund

Projekti:

Angazhimi i Kompanive për kryerje të punëve ndërtimore për implementimin e masave të Eficiencës së Energjisë në ndërtesat shumë banesore sociale

Nr. i kontratës: VET-FKEE2020-23-3896-2-1-1/C35_Lot 5

Kompania punëkryese



ATC COM SHPK & DARTING SHPK
nngatccom@gmail.com

Emri i ndërtesës:

**Ndërtesa shumë banesore sociale III,
Klinë - Lot 5**

Faza e projektimit:

Arkitektura

Emri i vizatimit:

Kulmi

Punuar nga:

BSc Liridon Sejdiu

Kontrolluar nga:

IDA. Njomza Hoti

Data:

08/2025

Rishikim:

Shkalla e zvogëlimit:

P=1:100

Nr. i faqes:

05