

REPUBLIKA E KOSOVËS / REPUBLIC OF KOSOVO
Fondi i Kosovës për Eficiencë të Energjisë
Kosovo Energy Efficiency Fund

Projekti:
Angazhimi i Kompanive për kryerje të punëve ndërtimore për implementimin e masave të Eficiencës së Energjisë në ndërtesat shumë banesore sociale

Nr. i kontratës: VET-FKEE2020-23-3696-2-1-1/C35_Lot 5

Kompania punëkryese





ATC COM SHPK & DAJTING SHPK
nnpattcom@gmail.com

Emri i ndërtesës:
**Ndërtesa shumë banesore sociale III,
Klinë - Lot 5**

Faza e projektimit:
Arkitektura

Emri i vizatimit:
Lokacioni i ndërtesës

Punuar nga: BSc Liridon Sejdiu	Kontrolluar nga: IDA. Njomza Hoti
Datë: 08/2025	Rishikim:
Shkalla e zvogëlimit:	Nr. i faqes: 01

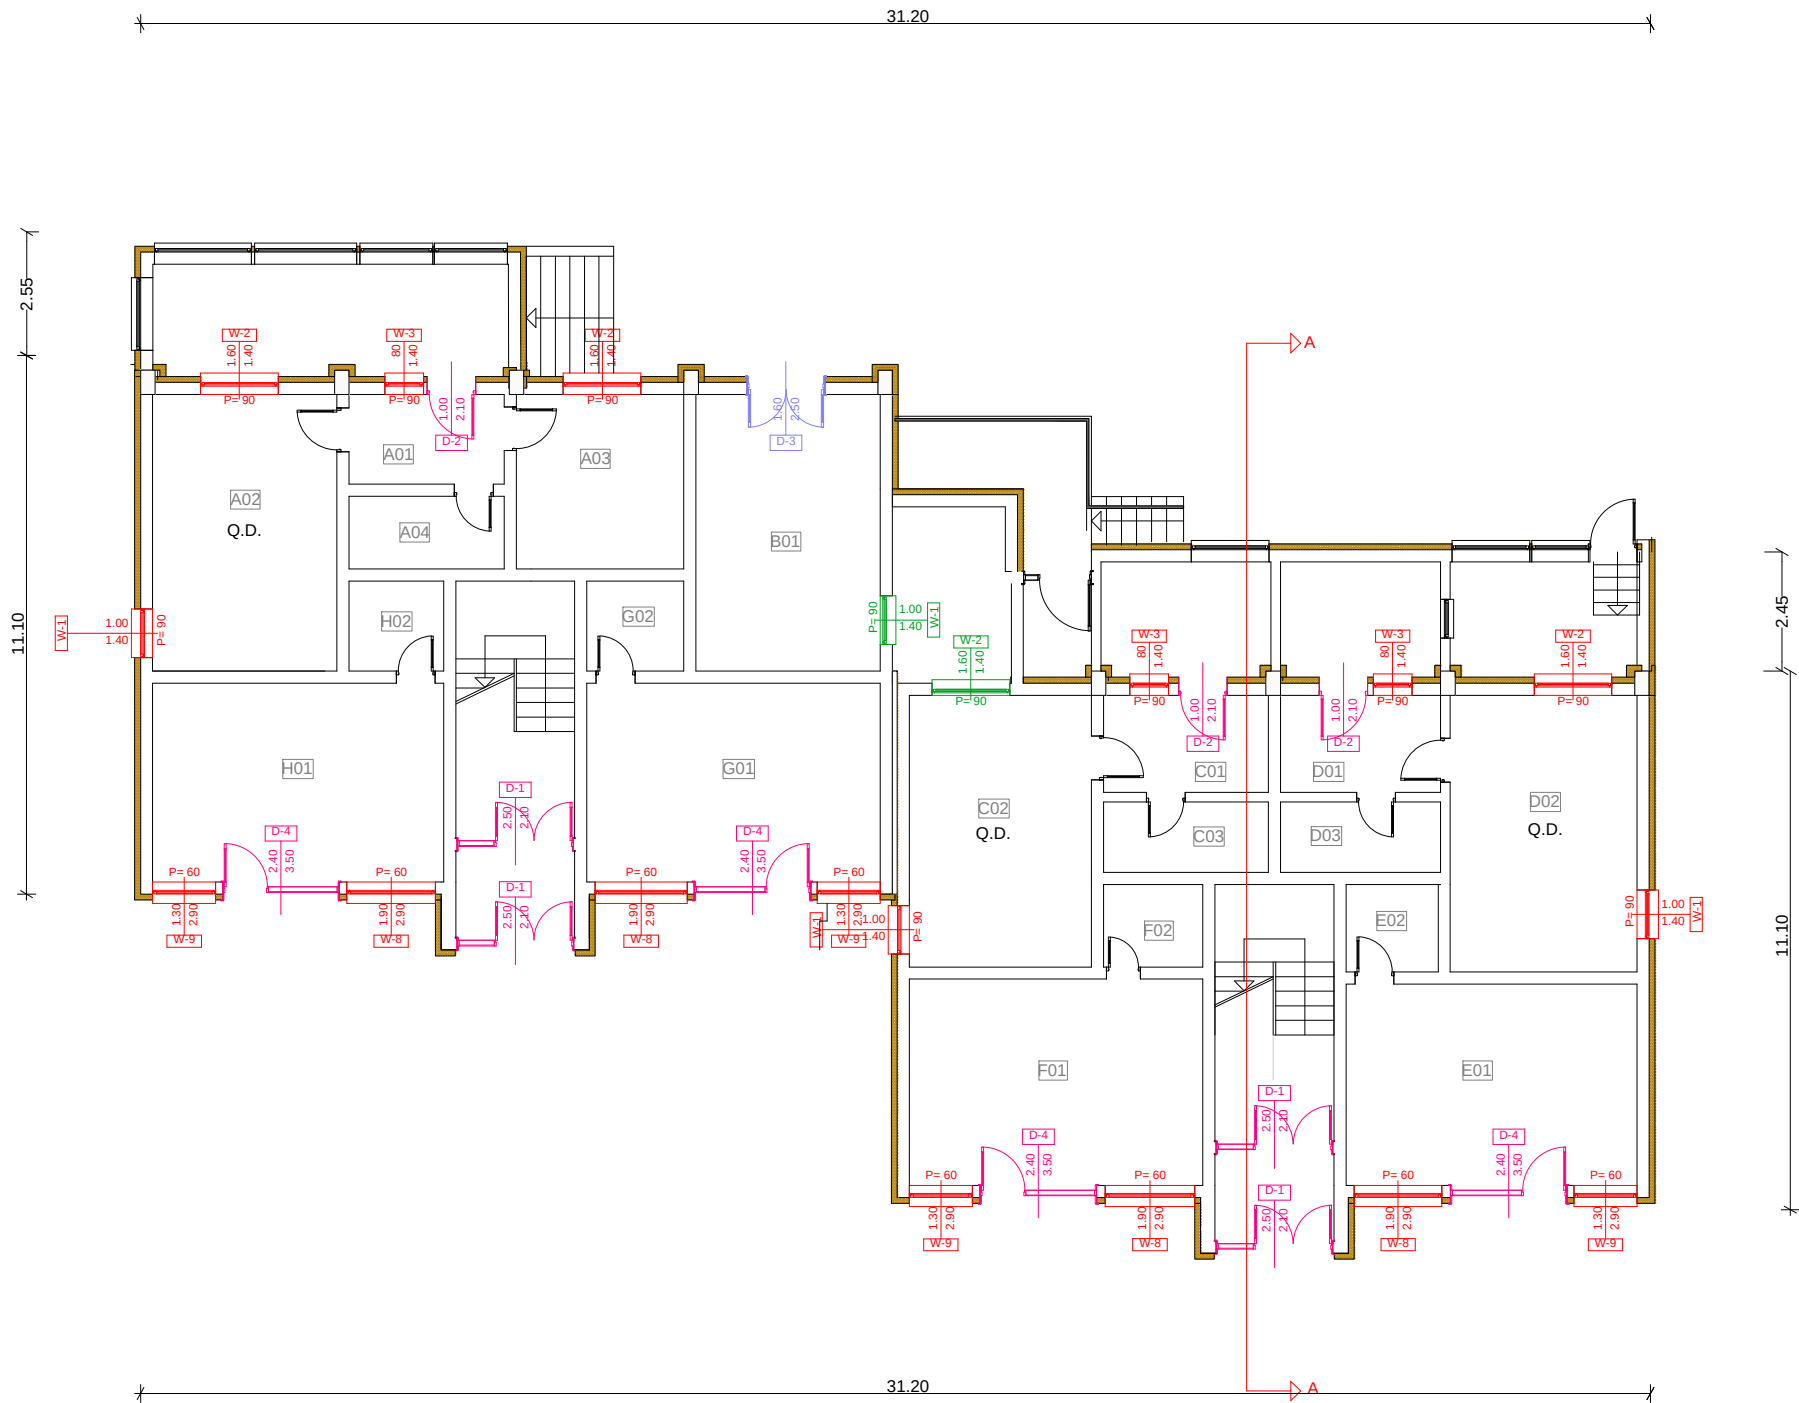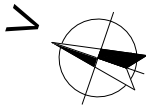

Përshkrimi renovimit

- Termoizolimi i mureve me EPS t=12cm
- Ndërrimi i dritareve
- Ndërrimi i dyerve
- Dritare të reja
- Ngjyrosje dhe renovimi i derës ekzistuese



REPUBLIKA E KOSOVËS / REPUBLIC OF KOSOVO
Fondi i Kosovës për Eficiencë të Energjisë
Kosovo Energy Efficiency Fund

Projekti:
Angazhimi i Kompanive për kryerje të punëve ndërtimore për implementimin e masave të Eficiencës së Energjisë në ndërtesat shumë banesore sociale

Nr. i kontratës: VET-FKEE2020-23-3696-2-1-1/C35_Lot 5



ATC
ALL
TYPE OF
CONSTRUCTION



ATC COM SHPK & DAITING SHPK
nngatccom@gmail.com

Emri i ndërtuesit:
**Ndërtesa shumë banesore sociale III,
Klinë - Lot 5**

Faza e projektimit:
Arkitektura

Emri i vizatimit:
Përdhesa

Punuar nga: BSc Liridon Sejdiu	Kontrolluar nga: IDA. Njomza Hoti
Data: 08/2025	Rishikim:
Shkalla e zvogëlimit: P=1:100	Nr. i faqes: 02

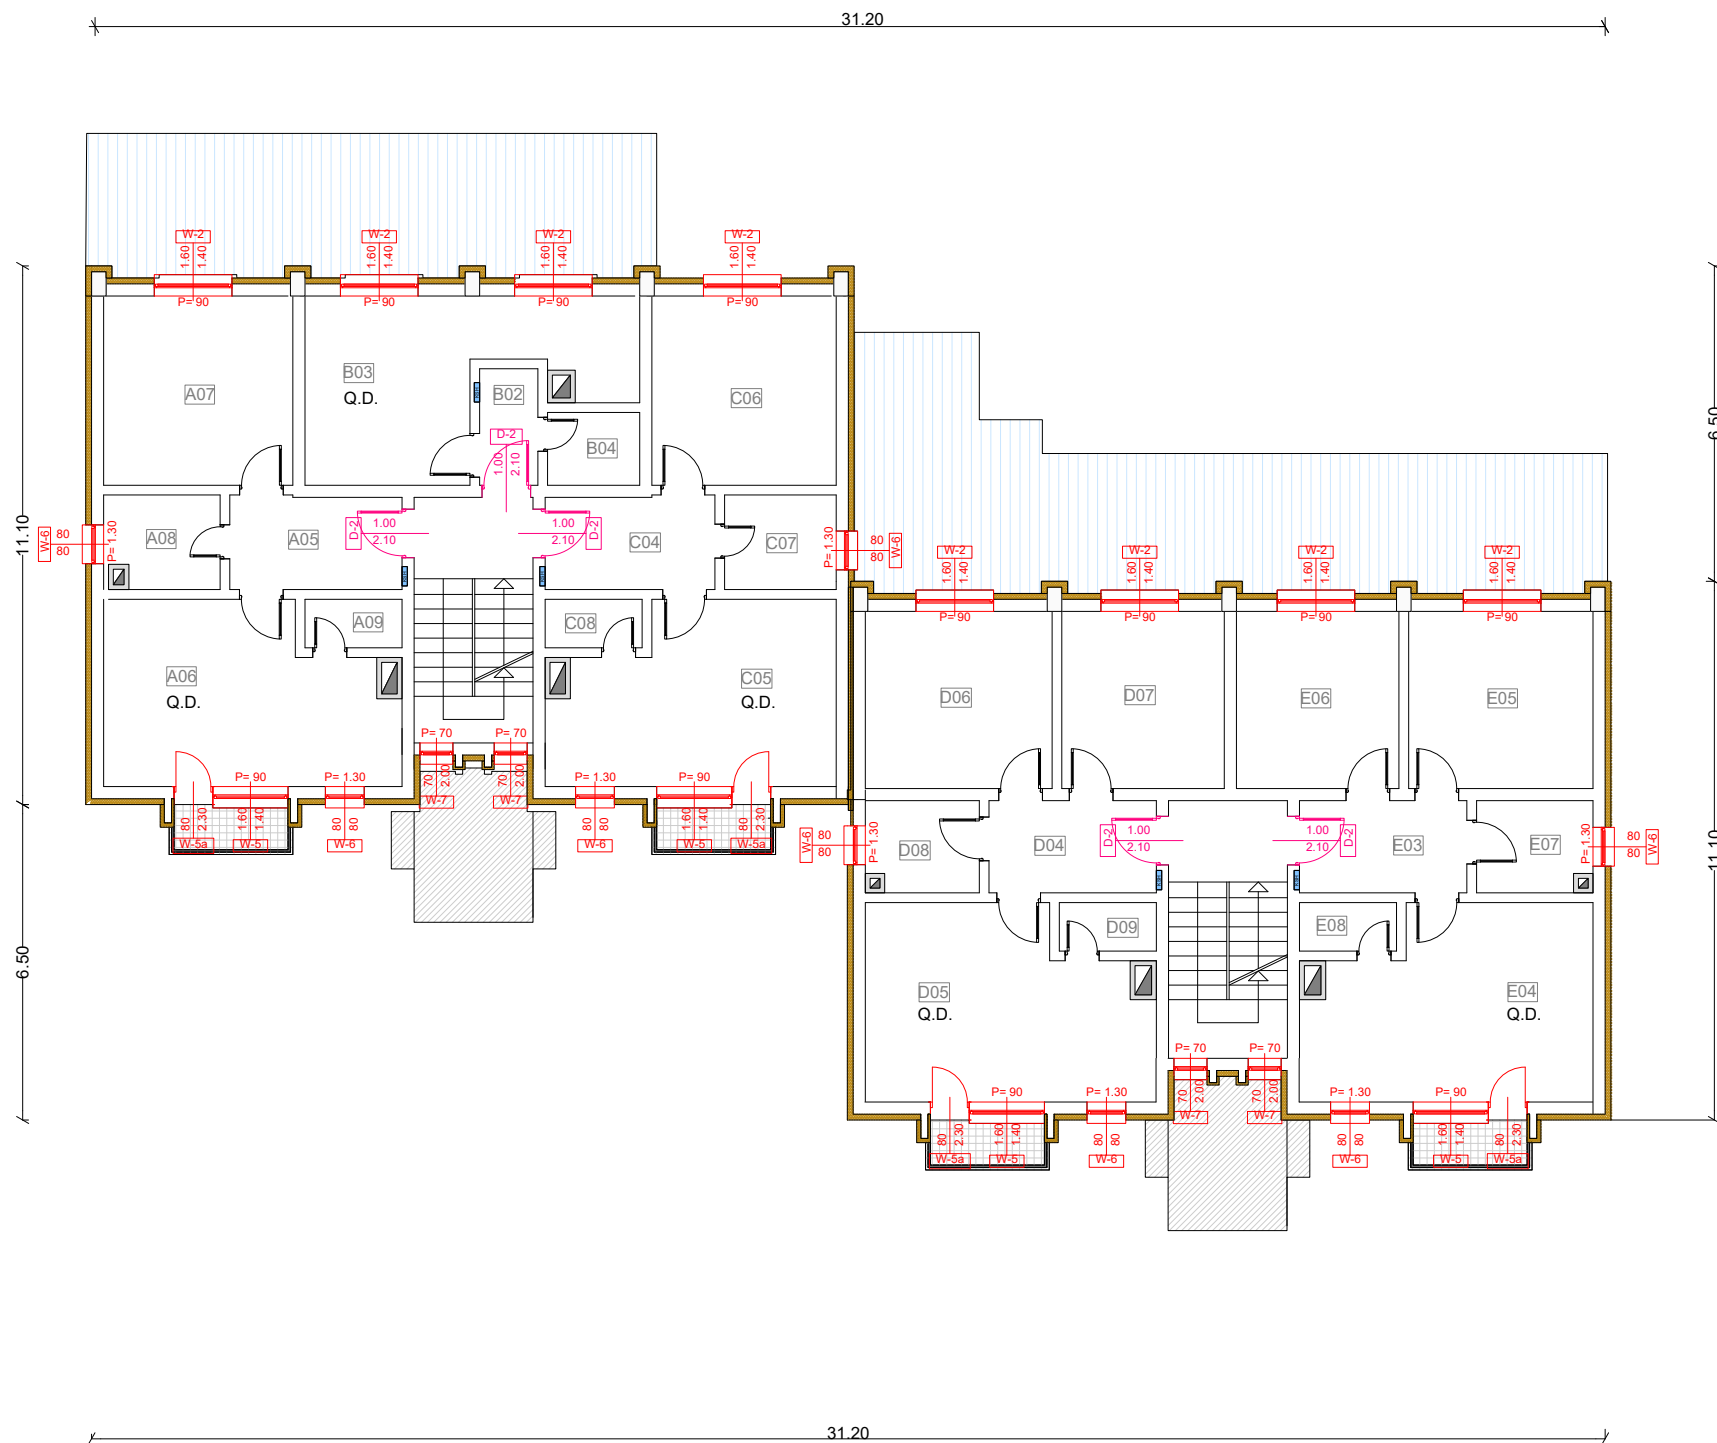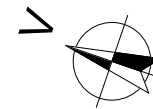

Përshkrimi i renovimit

- Termoizolimi i mureve me EPS t=12cm
- Ndërrimi i dritareve
- Ndërrimi i dyerve
- Renovimi i kulmit të strehës
- Kulmet e anekseve



REPUBLIKA E KOSOVËS / REPUBLIC OF KOSOVO
Fondi i Kosovës për Eficiencë të Energjisë
Kosovo Energy Efficiency Fund

Nr. i kontratës: VET-FKEE2020-23-3896-2-1-1/C35_Lot 5

Kompania punëkryese:



ATC COM SHPK & DATING SHPK
mpatccom@gmail.com

Emri i ndërtuesit:

**Ndërtesa shumë banesore sociale III,
Klinë - Lot 5**



Faza e projektimit:

Arkitektura

Emri i vizatimit:

Kati I



Punuar nga:	Kontrolluar nga:
BSc Liridon Sejdiu	IDA. Njomza Hoti
Data:	Rishikim:
08/2025	
Shkalla e zvogëlimit:	Nr. i faqes:
P=1:100	03

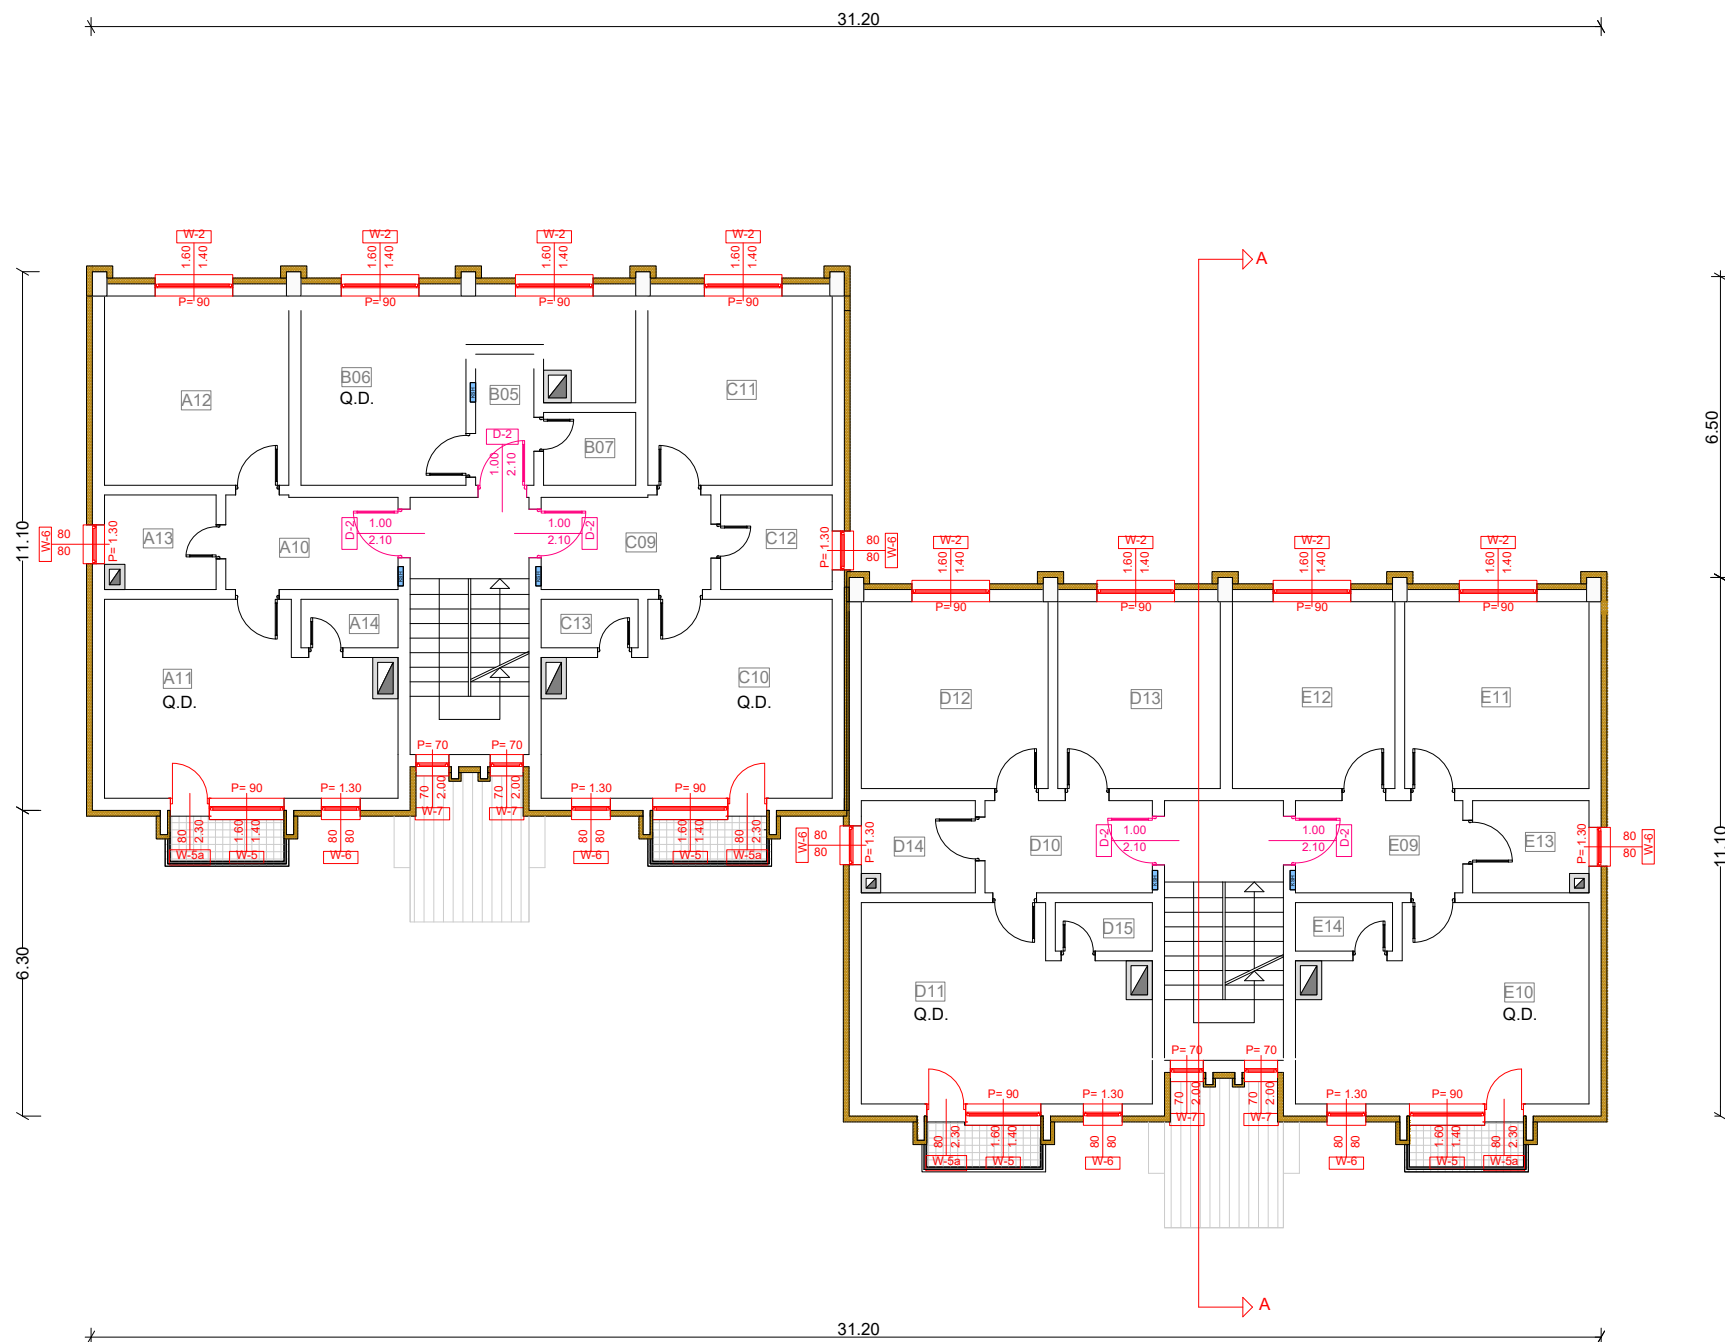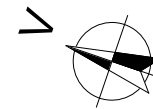

Përshkrimi i renovimit

- Termoizolimi i mureve me EPS t=12cm
- Ndërrimi i dritareve
- Ndërrimi i derve
- Renovimi i ballkoneve



 REPUBLIKA E KOSOVËS / REPUBLIC OF KOSOVO Fondi i Kosovës për Eficiencë të Energjisë Kosovo Energy Efficiency Fund	
Projekti: Angazhimi i Kompanive për kryerje të punëve ndërtimore për implementimin e masave të Eficiencës së Energjisë në ndërtësat shumë banesore sociale	
Nr. i kontratës: VET-FKEE2020-23-3896-2-1-1/C35_Lot 5	
Kompania punëkyese:  ATC COM SHPK & DATING SHPK mngatccom@gmail.com	
Emri i ndërtësatit: Ndërtësa shumë banesore sociale III, Klinë - Lot 5	
Faza e projektimit: Arkitektura	
Emri i vizatimit: Kati II-IV	
Punuar nga: BSc Liridon Sejdiu	Kontrolluar nga: IDA. Njomza Hoti
Data: 08/2025	Rishikim:
Shkalla e zvogëlimit: P=1:100	Nr. i faqes: 04

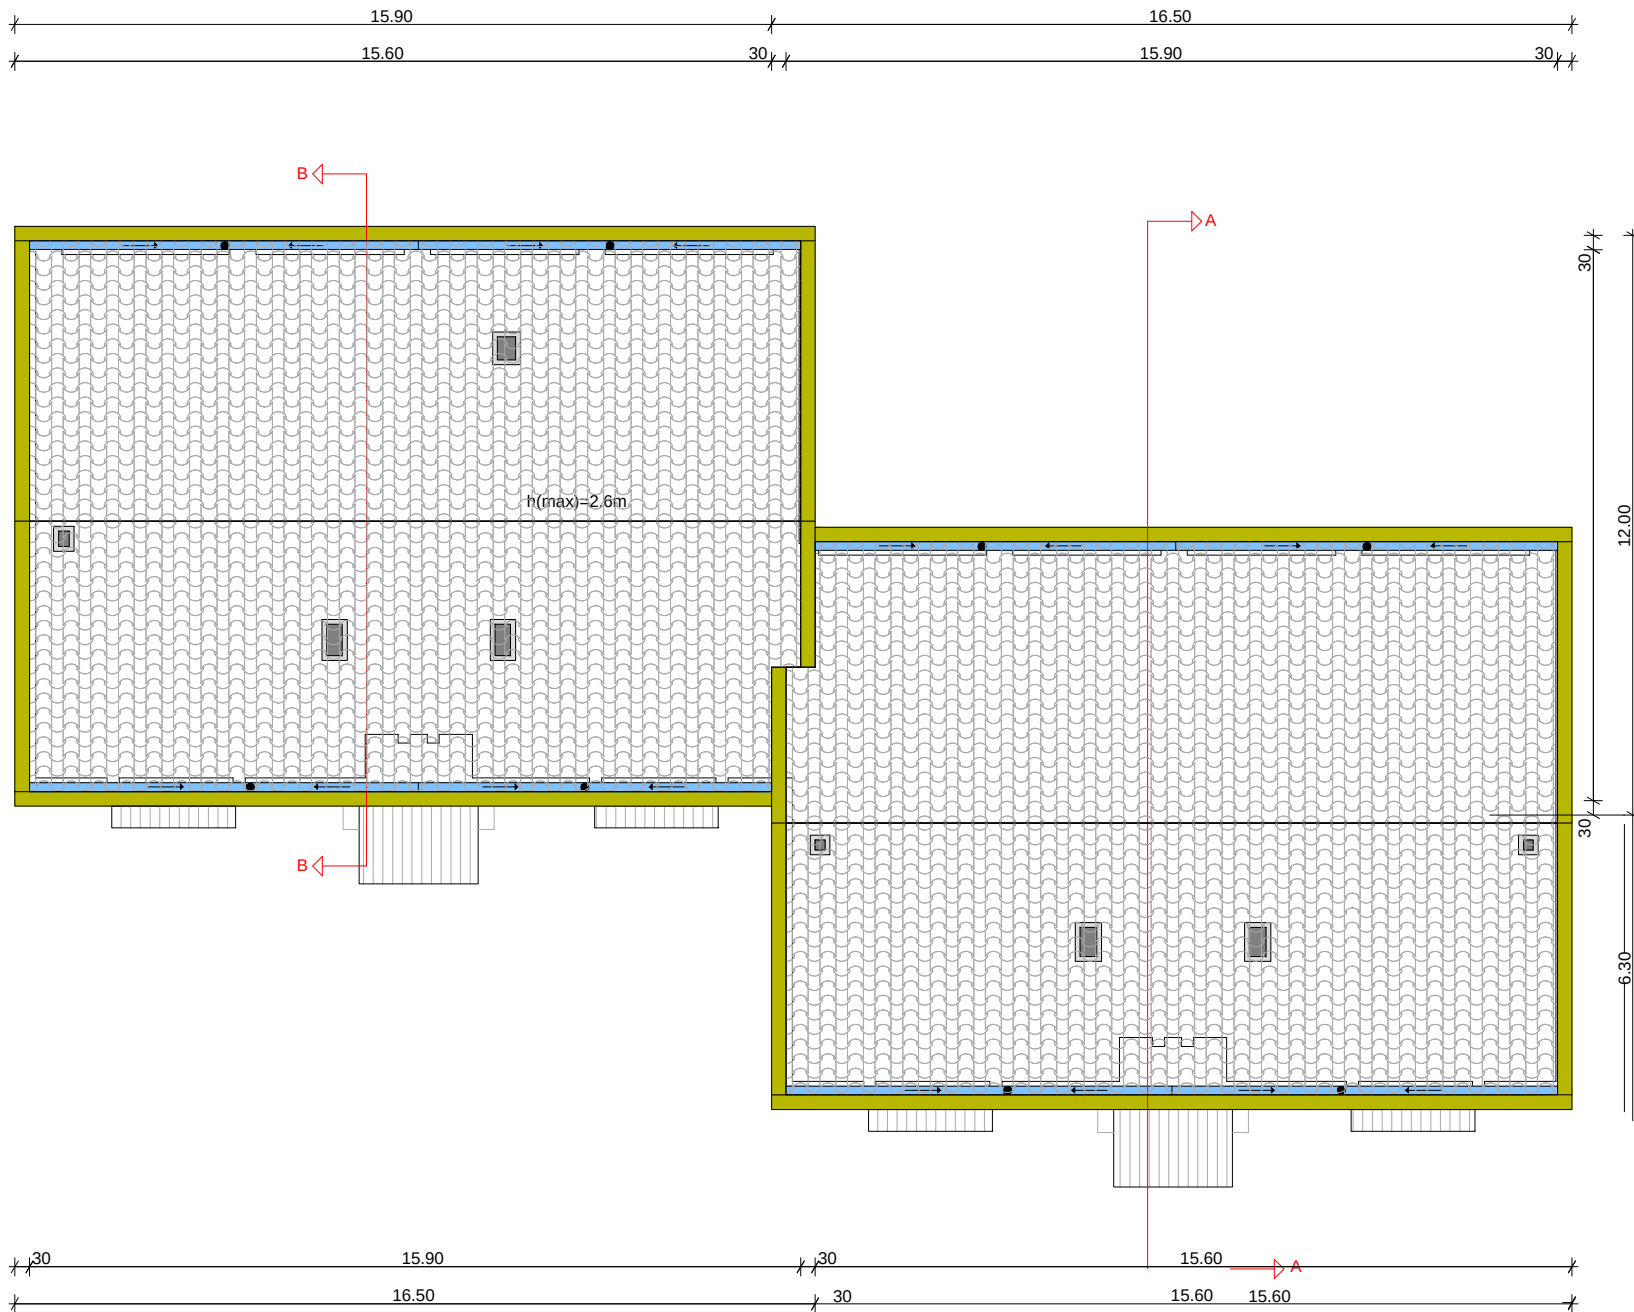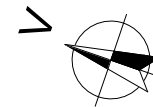

Përshkrimi i renovimit


- Renovimi dhe termoizolimi i kulmit me EPS t=16cm
- Ndërrimi i ulluqeve horizontale
- Ndërrimi i ulluqeve vertikale
- Ndërrimi i pikores
- Ndërrimi i llamarinës së ballkonave

 REPUBLIKA E KOSOVËS / REPUBLIC OF KOSOVO Fondi i Kosovës për Eficiencë të Energjisë Kosovo Energy Efficiency Fund	
Projekti: Angazhimi i Kompanive për kryerje të punëve ndërtimore për implementimin e masave të Eficiencës së Energjisë në ndërtesat shumë banesore sociale	
Nr. i kontratës: VET-FKEE2020-23-3896-2-1-1/C35_Lot 5	
Kompania punëkryese  ATC COM SHPK & DAITING SHPK nngatccom@gmail.com	
Emri i ndërtesës: Ndërtesa shumë banesore sociale III, Klinë - Lot 5	
Faza e projektimit: Arkitektura	
Emri i vizatimit: Kulmi	
Punuar nga: BSc Liridon Sejdiu	Kontrolluar nga: IDA. Njomza Hoti
Data: 08/2025	Rishikim:
Shkalla e zvogëlimit: P=1:100	Nr. i faqes: 05

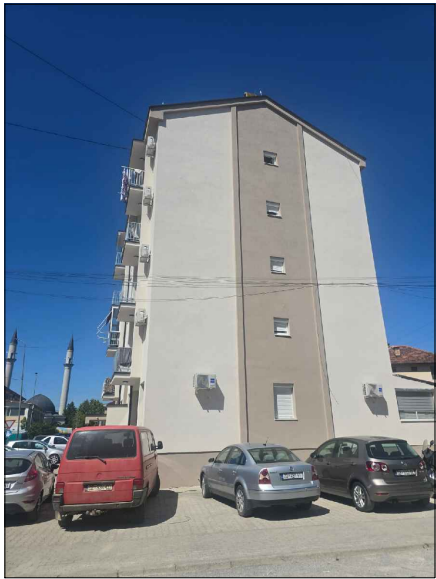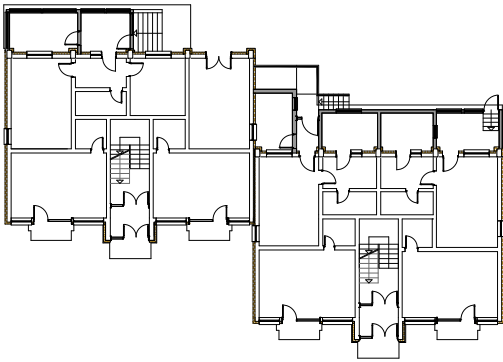

 REPUBLIKA E KOSOVËS / REPUBLIC OF KOSOVO Fondi i Kosovës për Eficiencë të Energjisë Kosovo Energy Efficiency Fund	
Projekti: Angazhimi i Kompanive për kryerje të punëve ndërtimore për implementimin e masave të Eficiencës së Energjisë në ndërtesat shumë banesore sociale	
Nr. i kontratës: VET-FKEE2020-23-3696-2-1-1/C35_Lot 5	
Kompania punekryese  ATC COM SHPK & DAJTING SHPK nnpatccom@gmail.com	
Emri i ndërtesës: Ndërtesa shumë banesore sociale III, Klinë - Lot 5	
Faza e projektimit: Arkitektura	
Emri i vizatimit: Fotot e ndërtesës	
Punuar nga: BSc Liridon Sejdiu	Kontrolluar nga: IDA. Njomza Hoti
Datë: 08/2025	Rishikim:
Shkalla e zvogëlimit:	Nr. i faqes: 06



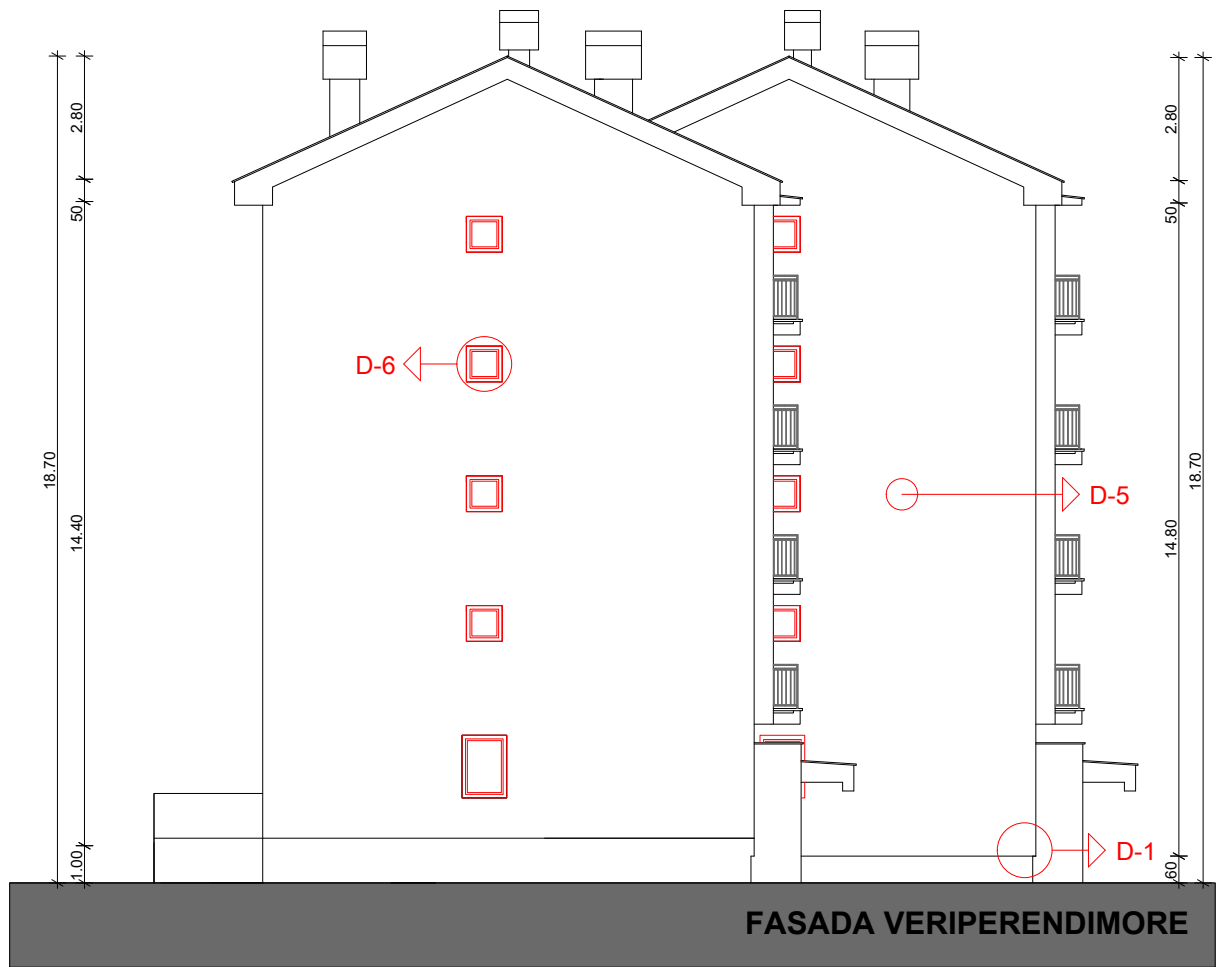

Përshkrimi renovimit

- Ndërrimi i dritareve
- Ndërrimi i derve

 REPUBLIKA E KOSOVËS / REPUBLIC OF KOSOVO Fondi i Kosovës për Eficiencë të Energjisë Kosovo Energy Efficiency Fund	
Projekti: Angazhimi i Kompanive për kryerje të punëve ndërtimore për implementimin e masave të Eficiencës së Energjisë në ndërtesat shumë banesore sociale	
Nr. i kontratës: VET-FKEE2020-23-3696-2-1-1/C35_Lot 5	
Kompania punëkryese:  ATC COM SHPK & DAITING SHPK regatcom@gmail.com	
Emri i ndërtesës: Ndërtesa shumë banesore sociale III, Klinë - Lot 5	
Faza e projektimit: Arkitektura	
Emri i vizatimit: Fasada Jugperëndimore & Veriperëndimore	
Punuar nga: BSc Liridon Sejdlu	Kontrolluar nga: IDA, Njomza Hoti
Datë: 08/2025	Rishikim:
Shkalla e zvogëlimit: P=1:100	Nr. i faqes: 08




- Përshkrimi renovimit**
- Ndërimi i dritareve
 - Ndërimi i dymve
 - Dritare të reja
 - Ngjyrosje dhe renovimi i derës ekzistuese

 REPUBLIKA E KOSOVËS / REPUBLIC OF KOSOVO Fondi i Kosovës për Eficiencë të Energjisë Kosovo Energy Efficiency Fund	
Projekti: Angazhimi i Kompanive për kryerje të punëve ndërtimore për implementimin e masave të Eficiencës së Energjisë në ndërtesat shumë banesore sociale	
Nr. i kontraktit: VET-FKKEE2020-23-3696-2-1-1-1C35_Lot 5	
Kompania punëkryesë:  ATC COM SHPK & DAJTING SHPK regatcom@gmail.com	
Emri i ndërtesës: Ndërtesa shumë banesore sociale III, Klinë - Lot 5	
Faza e projektimit: Arkitektura	
Emri i vizatimit: Fasada Verilindore & Juglindore	
Punuar nga: BSc Liridon Sejdlu	Kontrolluar nga: IDA, Njomza Hoti
Data: 08/2025	Rishikim:
Shkalla e zvogëlimit: P=1:100	Nr. i faqes: 09




FASADA JUGPERENDIMORE

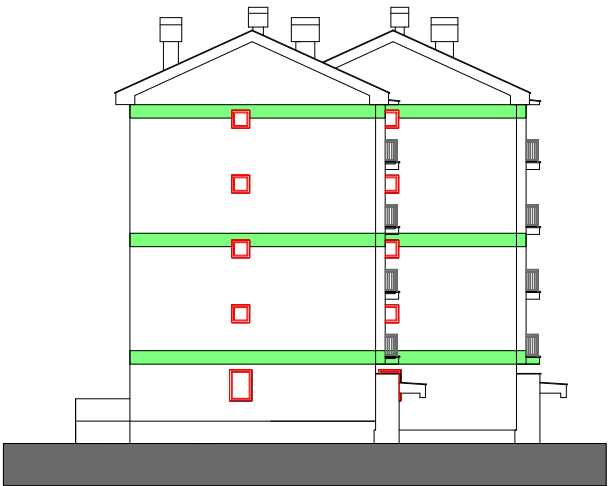

FASADA VERIPERENDIMORE



FASADA VERILINDORE

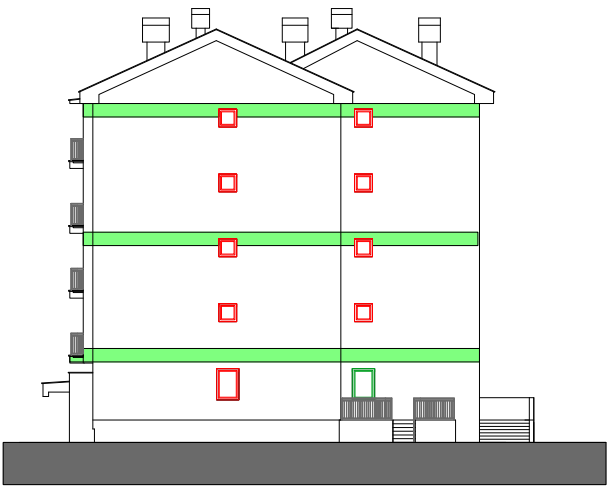





FASADA JUGLINDORE





Vërejtje: Masat mbrojtëse kundër zjarrit duhet të instalohen në tërë perimetrin e ndërtesës, si unazë me lësh guri dhe lartësi h=60cm sipas paraqitjeve grafike





Përshkrimi renovimit

Termoizolimi i mureve me Lësh Guri t=12cm

REPUBLIKA E KOSOVËS / REPUBLIC OF KOSOVO Fondi i Kosovës për Eficiencë të Energjisë Kosovo Energy Efficiency Fund	
Projekti: Angazhimi i Kompanive për kryerje të punëve ndërtimore për implementimin e masave të Eficiencës së Energjisë në ndërtesat shumë banesore sociale	
Nr. i kontratës: VET-FKEE2020-23-3696-2-1-1/C35_Lot 5	
Kompania punëkryese: ATC COM SHPK & DAITING SHPK engatcom@gmail.com	
Emri i ndërtesës: Ndërtesa shumë banesore sociale III, Klinë - Lot 5	
Faza e projektimit: Arkitektura	
Emri i vizatimit: Mbrojtja nga zjarri	
Punuar nga: BSc Liridon Sejdlu	Kontrolluar nga: IDA, Njomza Hoti
Data: 08/2025	Rishikim:
Shkalla e zvogëlimit: P=1:50	Nr. i faqes: 10

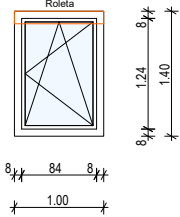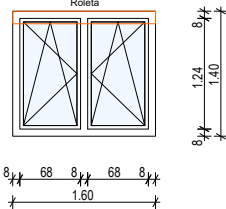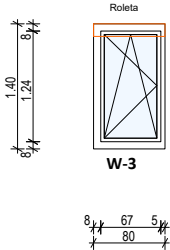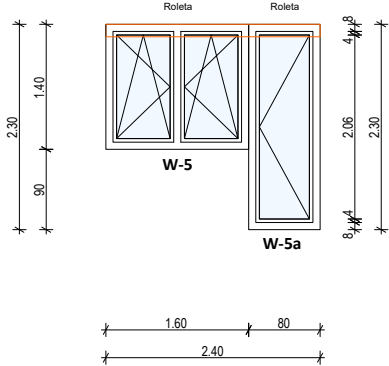SKEMAT E DRITAREVE					
Pos_W-1	Pos_W-2		Pos_W-3		Pos_W-5 Pos_W-5a
					
Pozicioni: W-1, dim. 1.00x1.40m	Sasia: 4	Pozicioni: W-2, dim. 1.60x1.40m	Sasia: 36	Pozicioni: W-3, dim. 0.70x1.40m	Sasia: 3
Pozicioni: W-5, dim. 1.60x1.40m	Sasia: 16	Pozicioni: W-5a, dim. 0.80x2.30m	Sasia: 16		

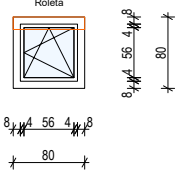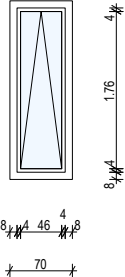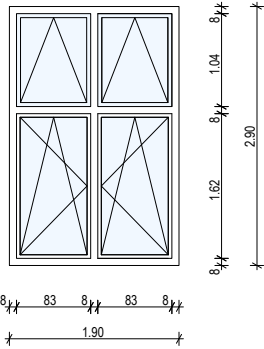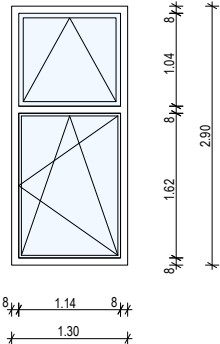SKEMAT E DRITAREVE					
Pos_W-6	Pos_W-7		Pos_W-8		Pos_W-9
					
Pozicioni: W-6, dim. 0.80x0.80m	Sasia: 32	Pozicioni: W-7, dim. 0.70x2.00m	Sasia: 16	Pozicioni: W-8, dim. 1.90x2.90m	Sasia: 4
Pozicioni: W-9, dim. 1.30x2.90m	Sasia: 4				

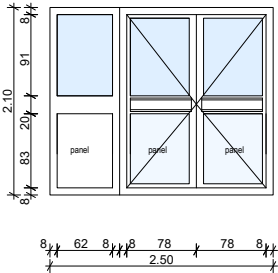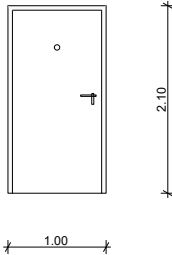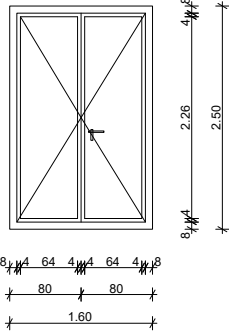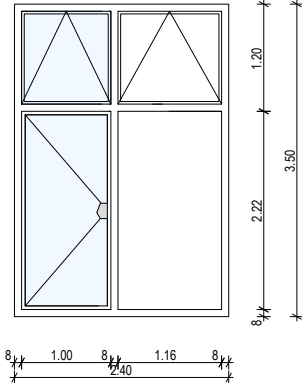SKEMA E DYERVE TË JASHTME					
Pos_D-1	Pos_D-2		Pos_D-3		Pos_D-4
					
Pozicioni: D-1, dim. 2.50x2.10m	Sasia: 4	Pozicioni: D-2, dim. 1.00x2.10m	Sasia: 22	Pozicioni: D-3, dim. 1.60x2.50m	Sasia: 1
Pozicioni: D-4, dim. 2.40x3.50m	Sasia: 4				

**FKEE**
FOND I KOSOVËS PËR EFIÇIENCËN E ENERGISË
Kosovo Energy Efficiency Fund

Projekti:
Angazhimi i Kompanive për kryerje të punëve ndërtimore për implementimin e masave të Eficiencës së Energjisë në ndërtesat shumë banesore sociale

Nr. i kontratës: VET-FKEE/2020-23-3696-2-1-1C38, Lot 5

**ATC**
ALL TRADING & CONSTRUCTION

ATC COM SHPK & DAITING SHPK
nnpotcom@gmail.com

Emri i ndërtuesit:
Ndërtesa shumë banesore sociale III, Klinë - Lot 5

Faza e projektimit:
Arkitektura

Emri i vizatimit:
Skemat e dymve dhe dritareve

Punuar nga:
BSc Liridon Sejdiu

Kontrolluar nga:
IDA. Njomza Hoti

Data:
08/2025

Rishikim:

Shkalla e zvogëlimit:
P=1:50

Nr. i faqes:
11