



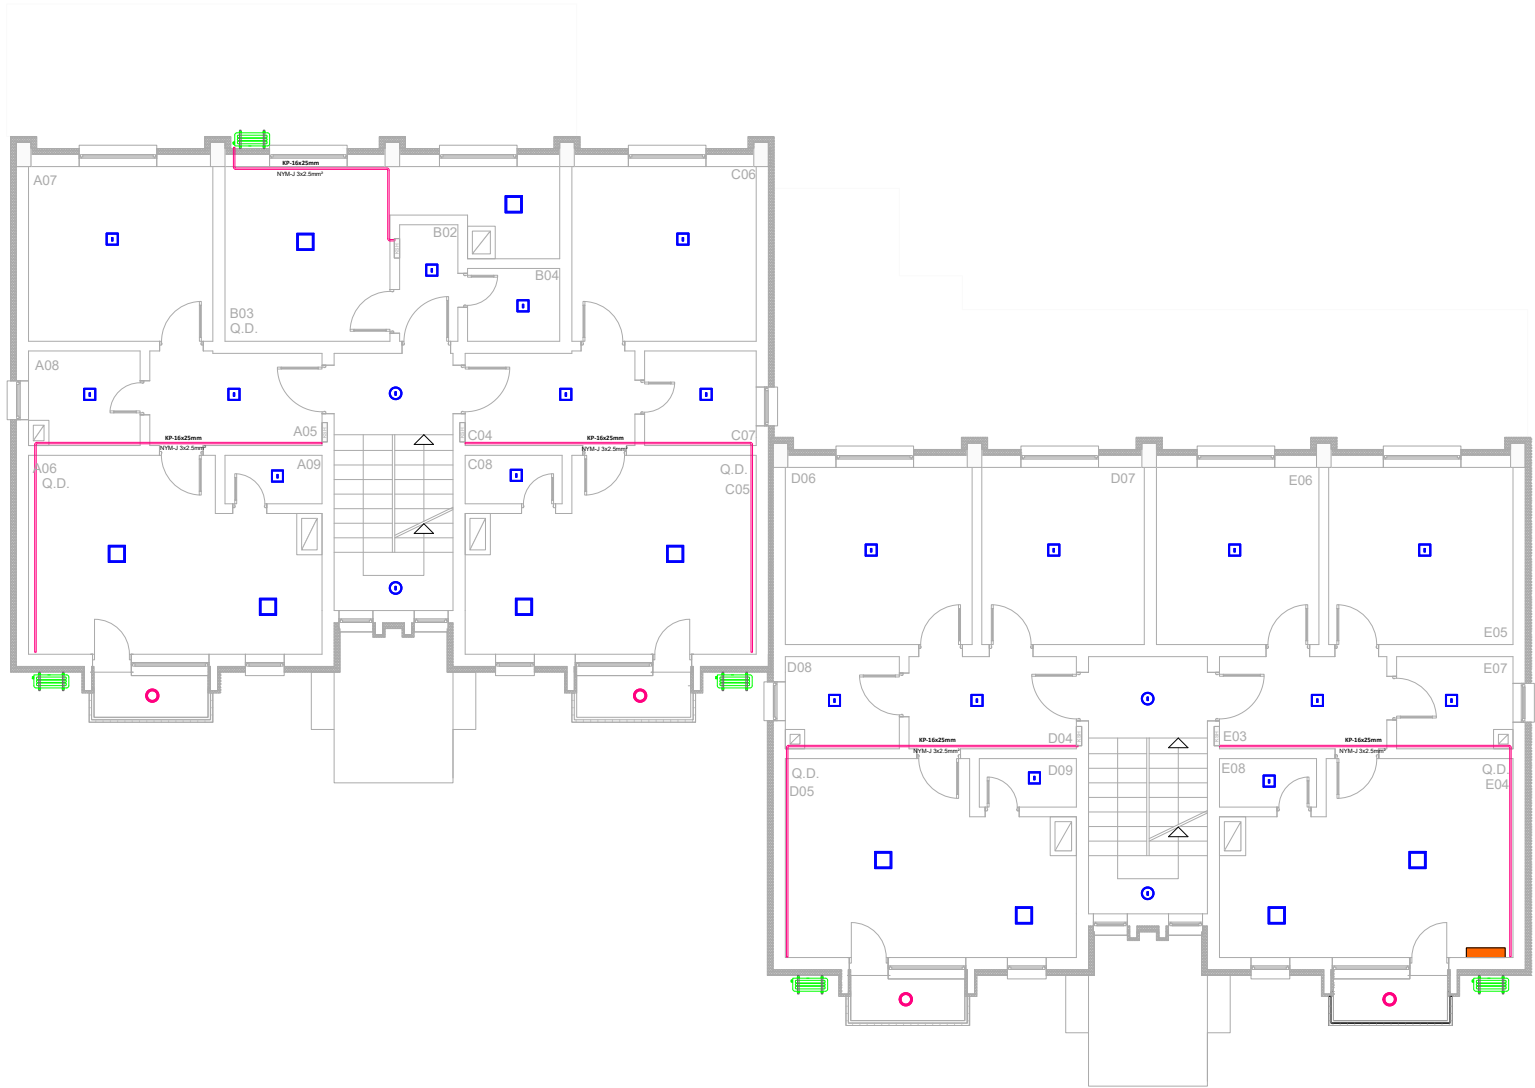

NDRËCHESIT E RI		
Lloji i Drites		Numerimi
	LED panel 24W ,2400lm ,IP44 295x295mm. Per monim ne tavan betoni.	10
	LED panel 18W ,1800lm ,IP44 225x225mm. Per monim ne tavan betoni.	20
	LED panel 12W me sensor, 1440lm, IP 44. Per monim ne tavan betoni.	4
	LED panel 12W Poqi E27,1000lm,IP65, Ø275mm. Per montim në plafon betoni	4

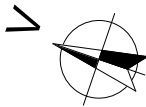

REPUBLIKA E KOSOVËS / REPUBLIC OF KOSOVO
Fondi i Kosovës për Eficiencë të Energjisë
Kosovo Energy Efficiency Fund

Projekti:

Angazhimi i Kompanive për kryerje të punëve ndërtimore për implementimin e masave të Eficiencës së Energjisë në ndërtesat shumë banesore sociale

Nr. i kontratës: VET-FKEE2020-23-3896-2-1-1/C35_Lot 5

Kompania punëkryese:



ATC COM SHPK & DAIJING SHPK
mngatccom@gmail.com

Emri i ndërtesës:

**Ndërtesa shumë banesore sociale III,
Klinë - Lot 5**


Faza e projektimit:

ELEKTRIKE

Emri i vizatimit:

Kati 1

Punuar nga:	Kontrolluar nga:
BSc Liridon Sejdiu	IDA. Njomza Hoti
Datë:	Rishikim:
08/2025	
Shkalla e zvogëlimit:	Nr. i faqes:
P=1:100	02

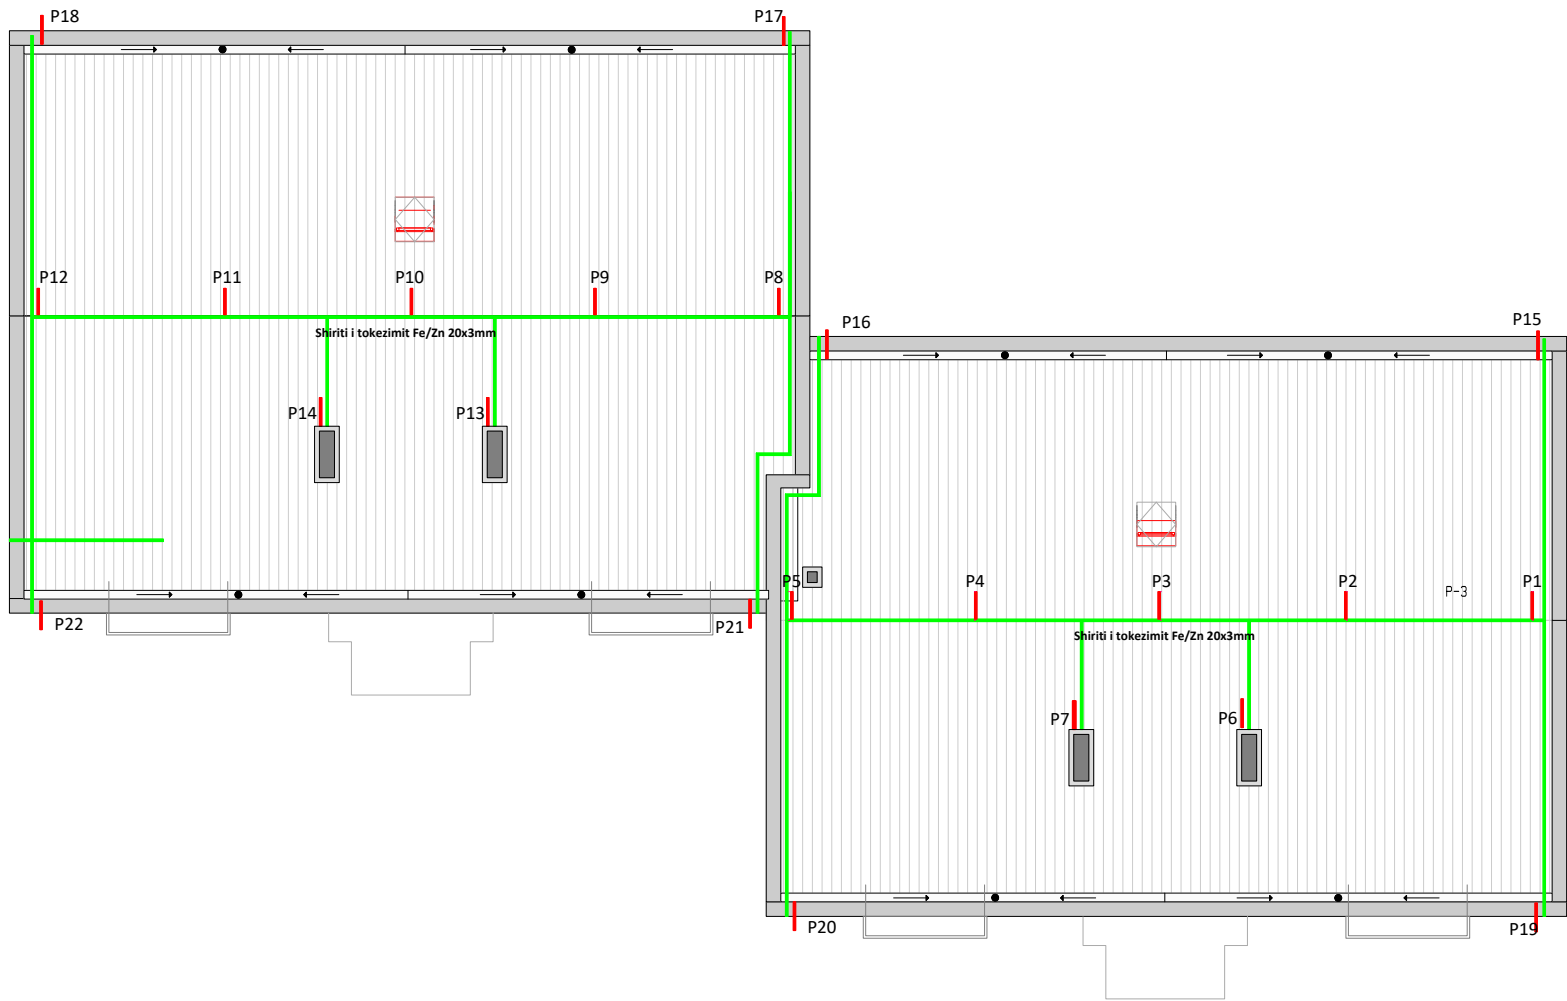

	Pranues i rrufesë l=0.50m.
	Shirit i tokëzimit Fe/Zn 20x3mm



REPUBLIKA E KOSOVËS / REPUBLIC OF KOSOVO
Fondi i Kosovës për Eficiencë të Energjisë
Kosovo Energy Efficiency Fund

Projekti:

Angazhimi i Kompanive për kryerje të punëve ndërtimore për implementimin e masave të Eficiencës së Energjisë në ndërtuesat shumë banesore sociale

Nr. i kontratës: VET-FKEE2020-23-3896-2-1-1/C35_Lot 5

Kompania punëkryese:



ATC COM SHPK & DAITING SHPK
mpatccom@gmail.com

Emri i ndërtuesat:

Ndërtesa shumë banesore sociale III,
Klinë - Lot 5



Faza e projektimit:

ELEKTRIKE

Emri i vizatimit:

Kulmi

Punuar nga:	Kontrolluar nga:
BSc Liridon Sejdiu	IDA. Njomza Hoti
Data:	Rishikim:
08/2025	
Shkalla e zvogëlimit:	Nr. i faqes:
P=1:100	03

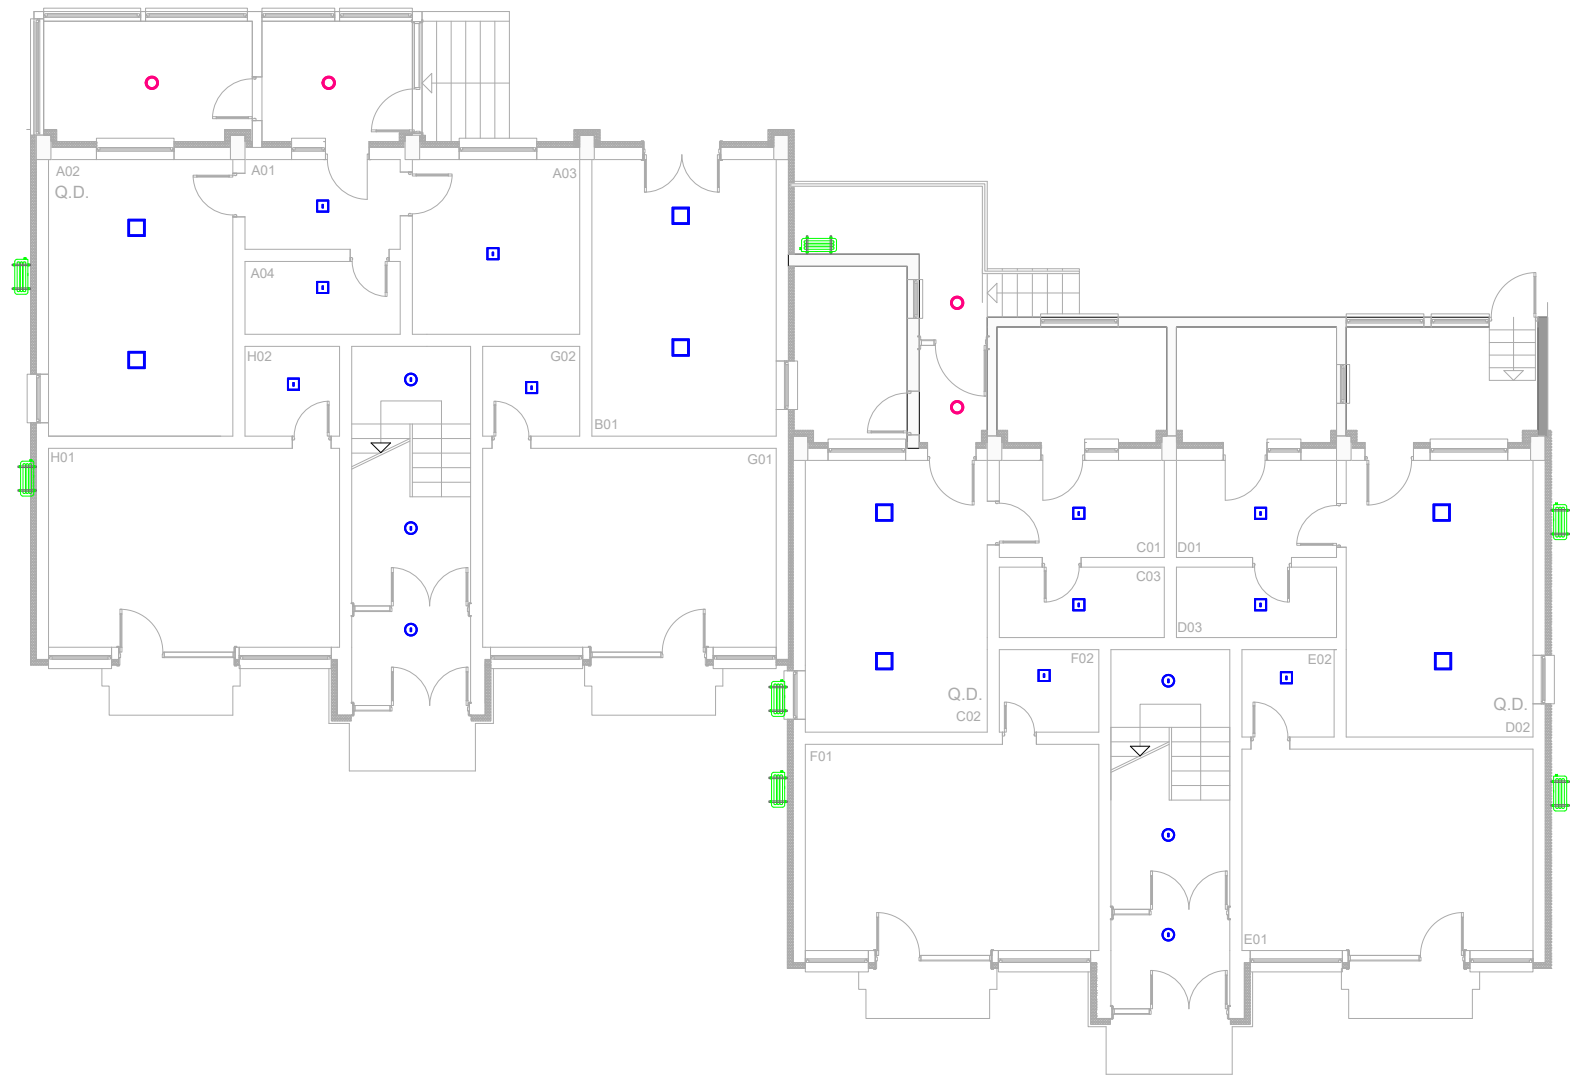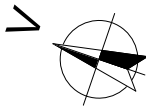

NDRIÇESIT E RI		
Lloji i Drites		Numerimi
	LED panel 24W ,2400lm ,IP44 295x295mm. Per montim ne tavan betoni.	8
	LED panel 18W ,1800lm ,IP44 225x225mm. Per montim ne tavan betoni.	12
	LED panel 12W me sensor, 1440lm, IP 44. Per montim ne tavan betoni.	6
	LED panel 12W Poqi E27,1000lm,IP65, Ø275mm. <i>Per montim ne pilafon betoni</i>	4



REPUBLIKA E KOSOVËS / REPUBLIC OF KOSOVO
Fondi i Kosovës për Eficiencë të Energjisë
Kosovo Energy Efficiency Fund

Projekti:
Angazhimi i Kompanive për kryerje të punëve ndërtimore për
implementimin e masave të Eficiencës së Energjisë në ndërtesat
shumë banesore sociale

Nr. i kontratës: VET-FKEE2020-23-3896-2-1-1/C35_Lot 5



ALL
TYPES OF
CONSTRUCTION

ATC COM SHPK & DATING SHPK
mngatccom@gmail.com

Emri i ndërtesës:
**Ndërtesa shumë banesore sociale III,
Klinë - Lot 5**

Faza e projektimit:
ELEKTRIKE

Emri i vizatimit:
Përdhesa

Punuar nga: BSc Liridon Sejdiu	Kontrolluar nga: IDA. Njomza Hoti
Datë: 08/2025	Rishikim:
Shkalla e zvogëlimit: P=1:100	Nr. i faqes: 01