



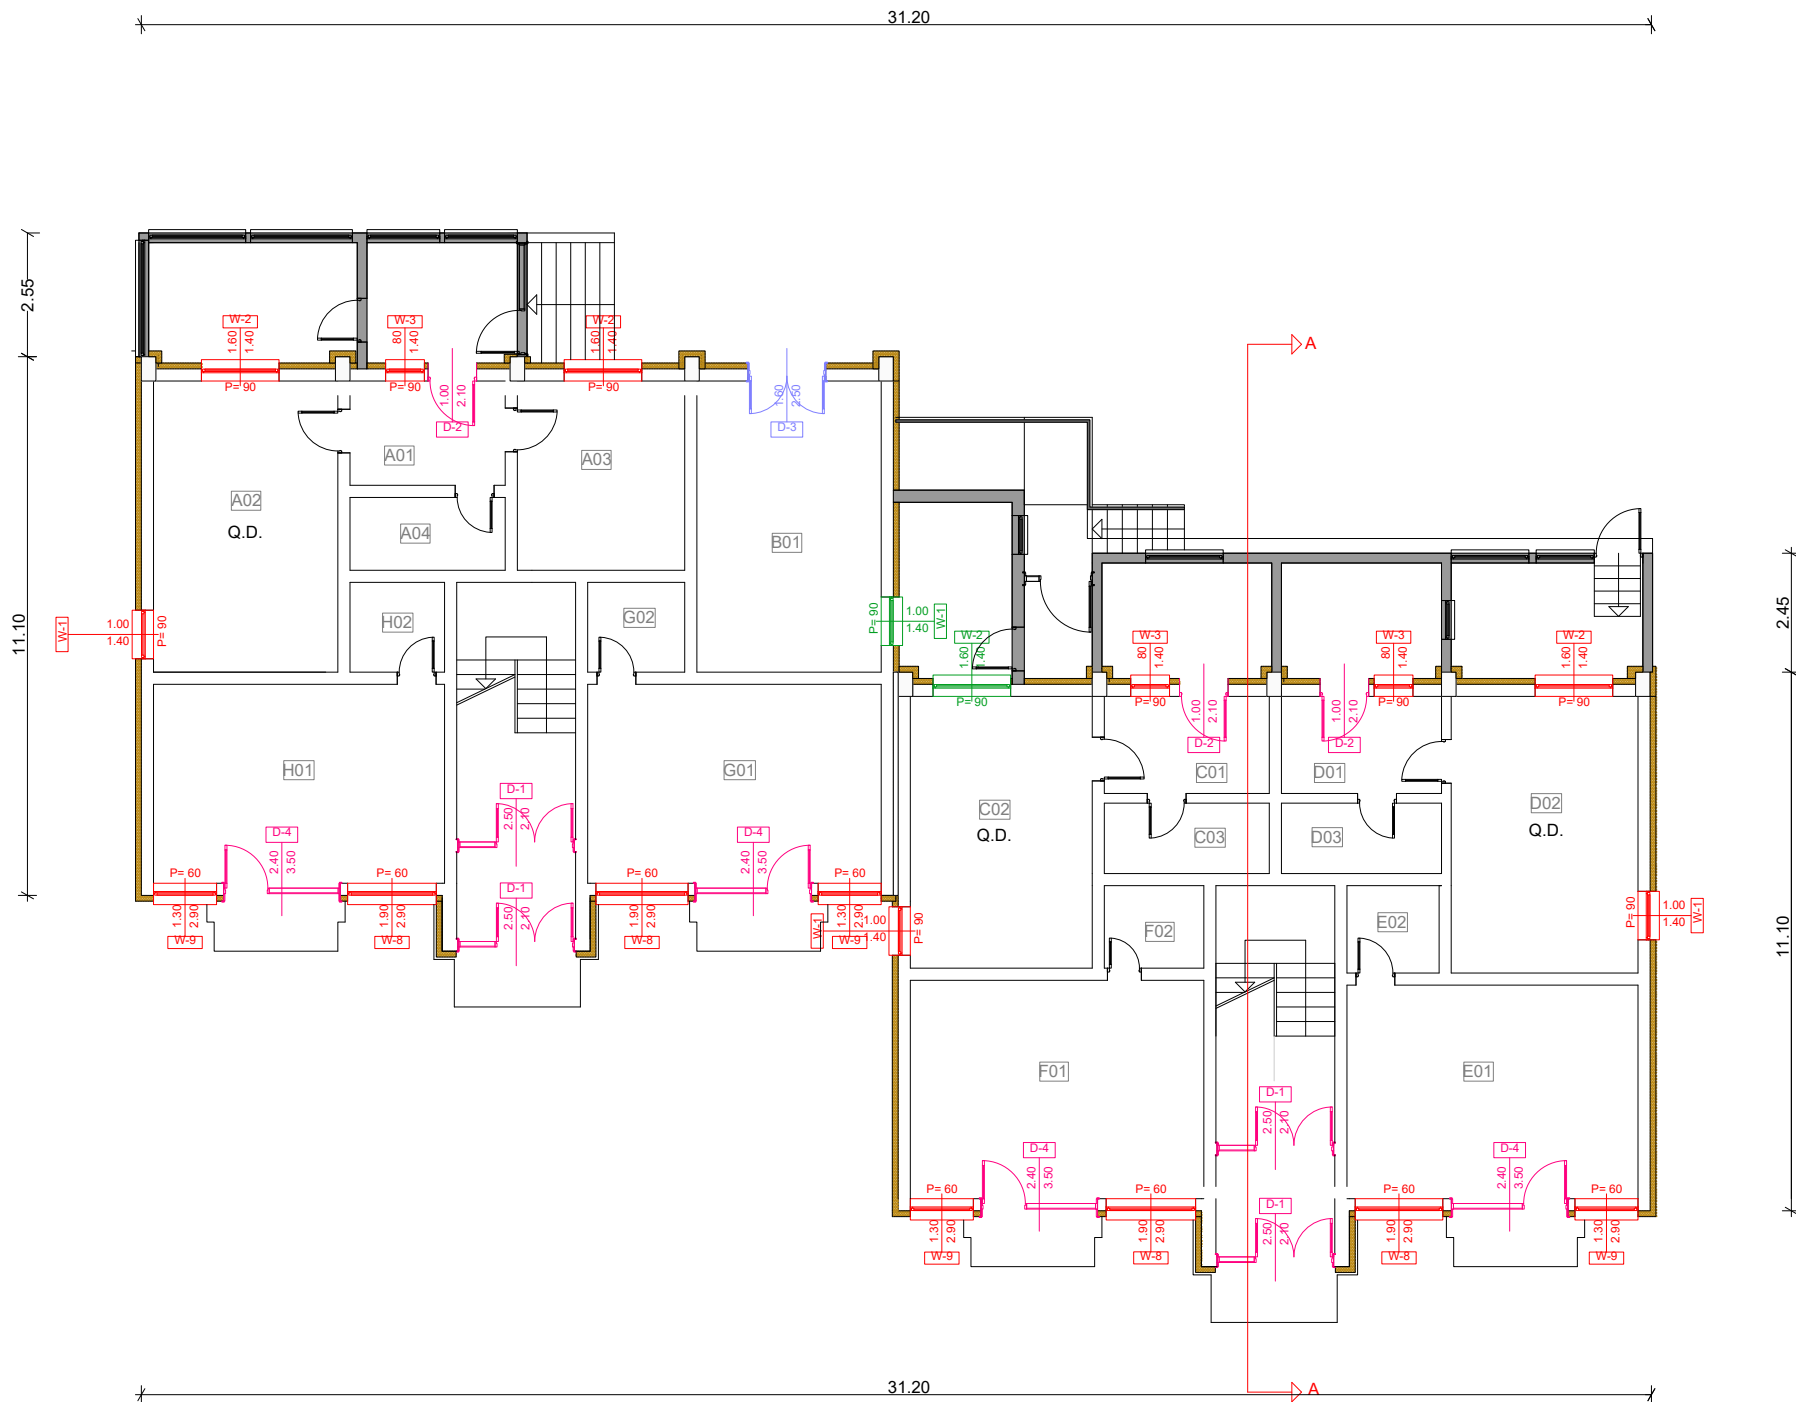

**Përshkrimi renovimit**

- Termoizolimi i mureve me EPS t=12cm
- Ndërrimi i dritareve
- Ndërrimi i dyerve
- Dritare të reja
- Ngjyrosje dhe renovimi i derës ekzistuese

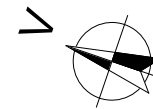

**REPUBLIKA E KOSOVËS / REPUBLIC OF KOSOVO**  
Fondi i Kosovës për Eficiencë të Energjisë  
Kosovo Energy Efficiency Fund

Projekti:

Angazhimi i Kompanive për kryerje të punëve ndërtimore për implementimin e masave të Eficiencës së Energjisë në ndërtesat shumë banesore sociale

Nr. i kontratës: VET-FKEE2020-23-3896-2-1-1/C35\_Lot 5



ATC COM SHPK & DATING SHPK  
mpatccom@gmail.com

Kompania punëkyese:

Emri i ndërtuesit:

**Ndërtesa shumë banesore sociale III,  
Klinë - Lot 5**

Faza e projektimit:

Arkitektura

Emri i vizatimit:

Përdhesa

|                       |                  |
|-----------------------|------------------|
| Punuar nga:           | Kontrolluar nga: |
| BSc Liridon Sejdiu    | IDA. Njomza Hoti |
| Data:                 | Rishikim:        |
| 08/2025               |                  |
| Shkalla e zvogëlimit: | Nr. i faqes:     |
| P=1:100               | 02               |